






1  
A-01  
EXTERIOR PERSPECTIVE  
SCALE: NTS.

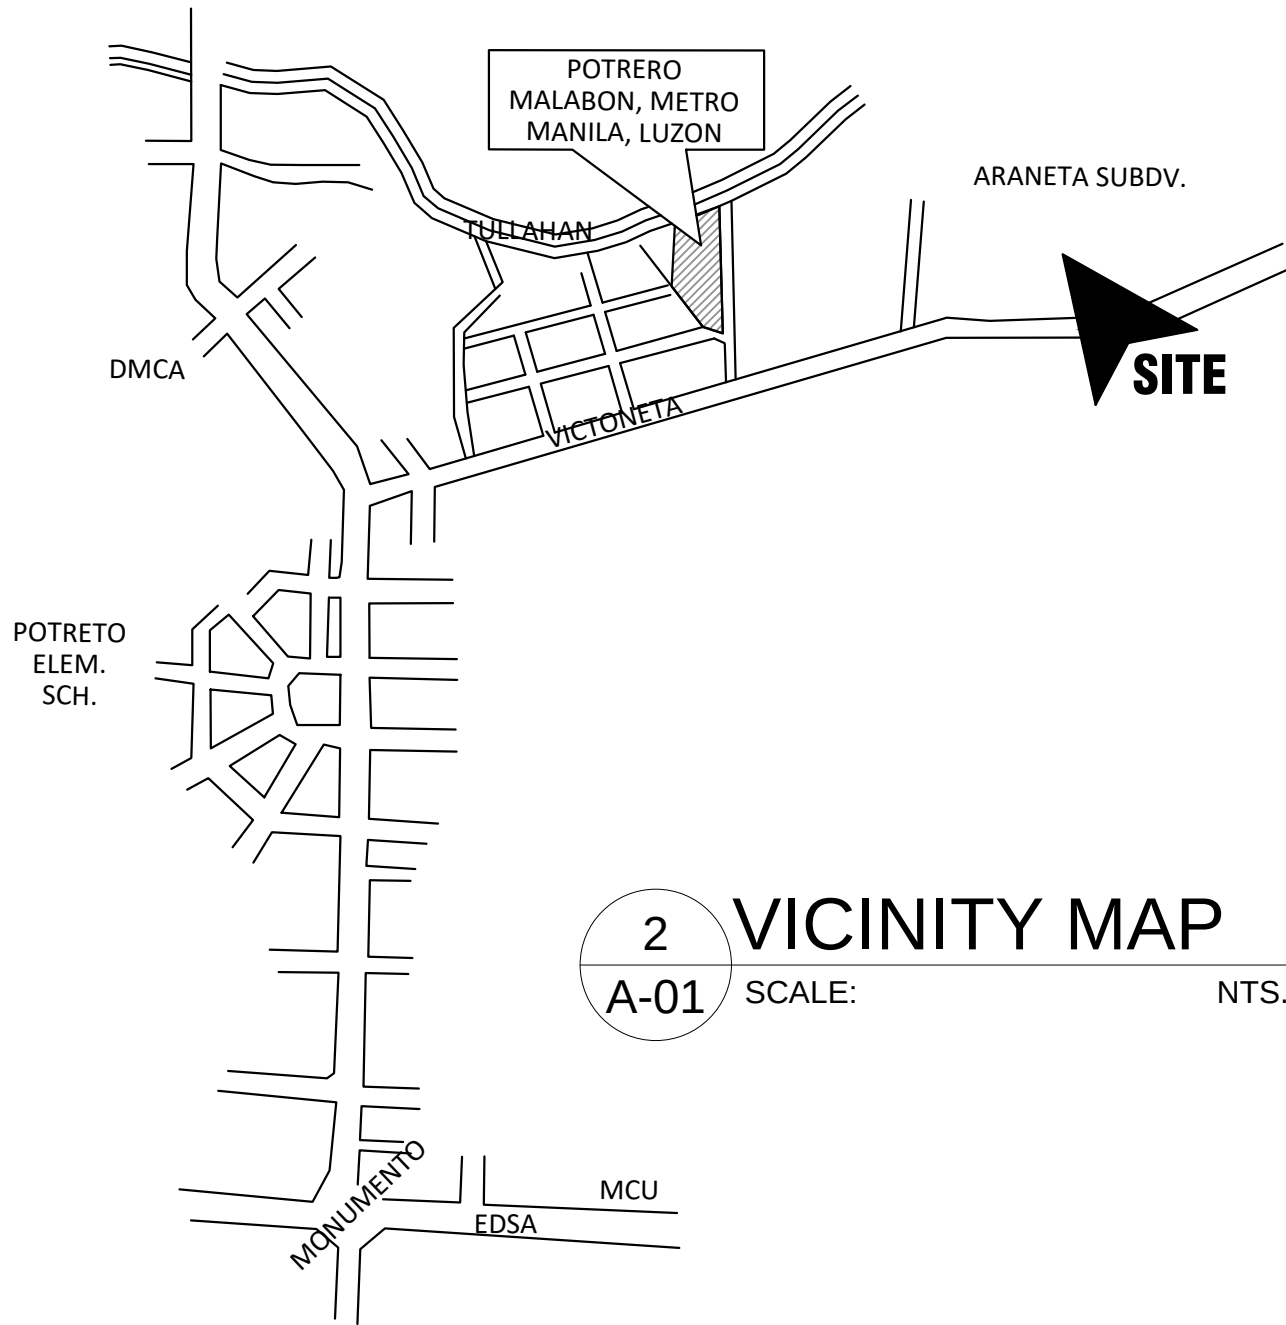


2  
A-01  
VICINITY MAP  
SCALE: NTS.

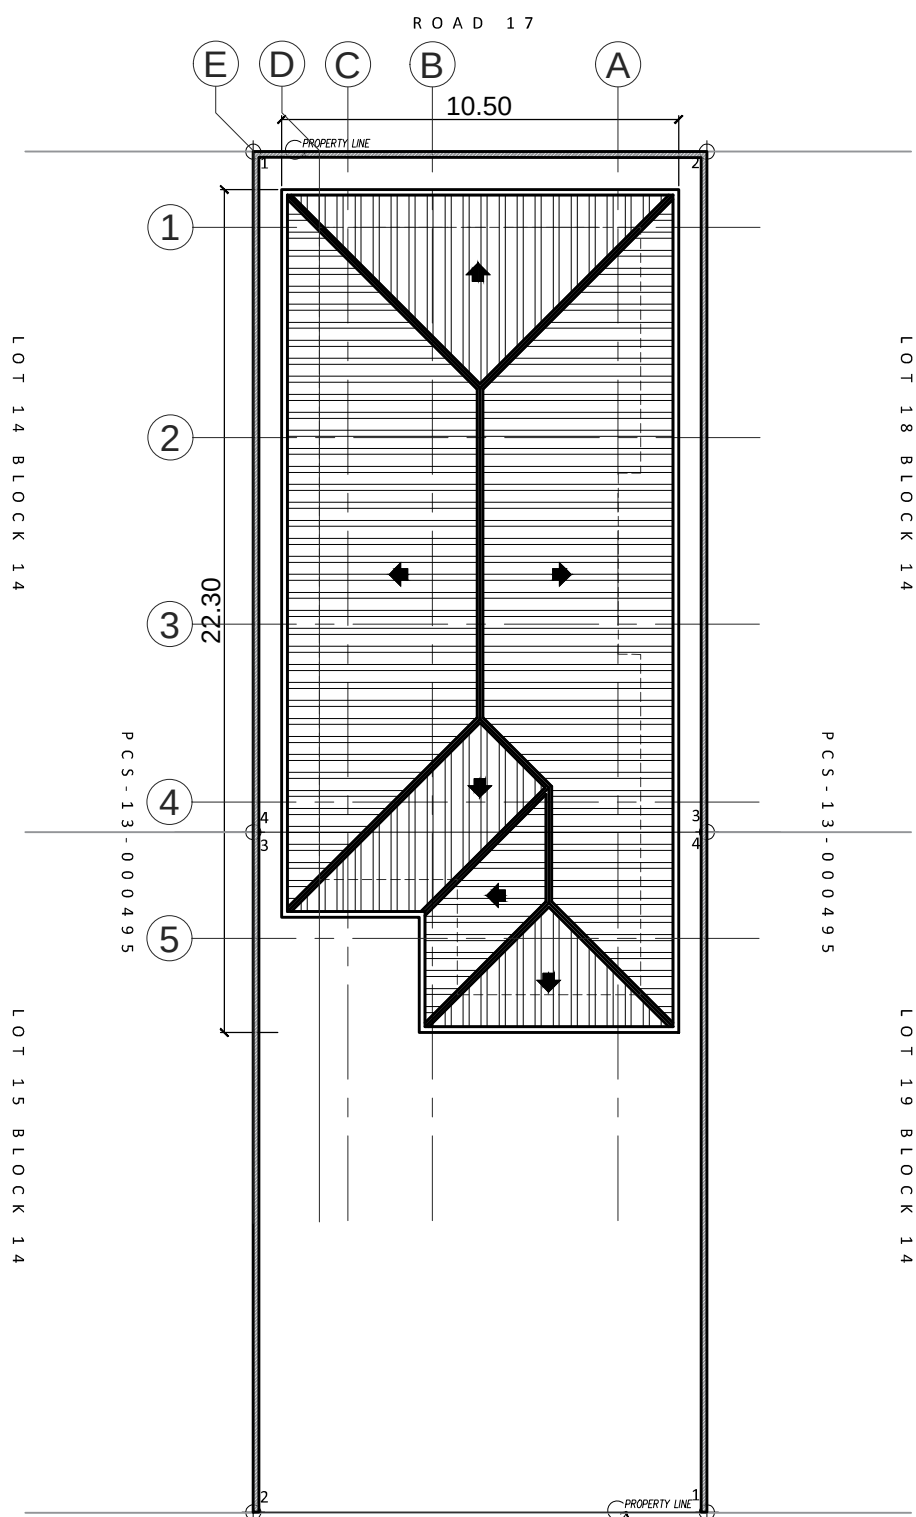

3  
A-01  
SITE DEVELOPMENT PLAN  
SCALE: 1:200 MTS.

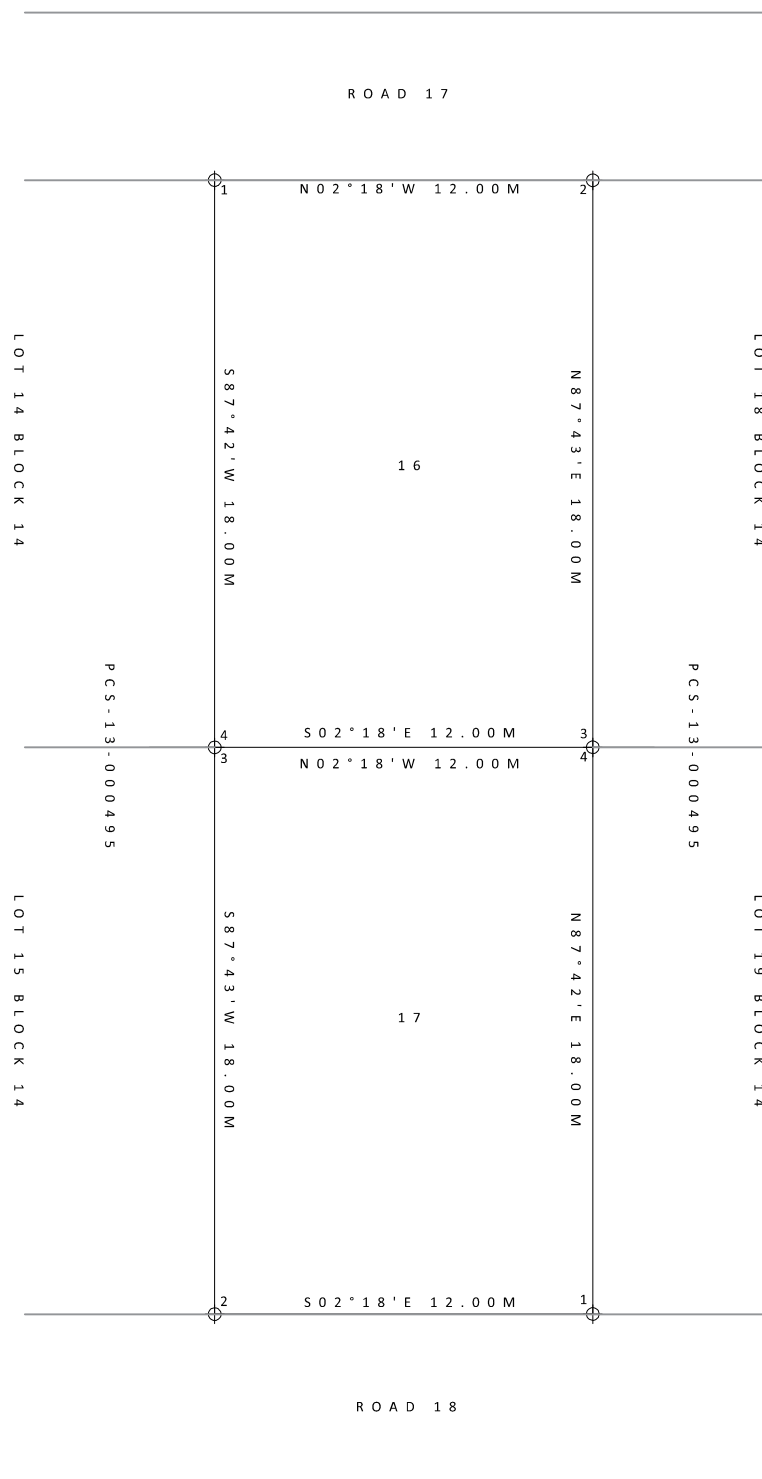

4  
A-01  
LOT PLAN  
SCALE: NTS.

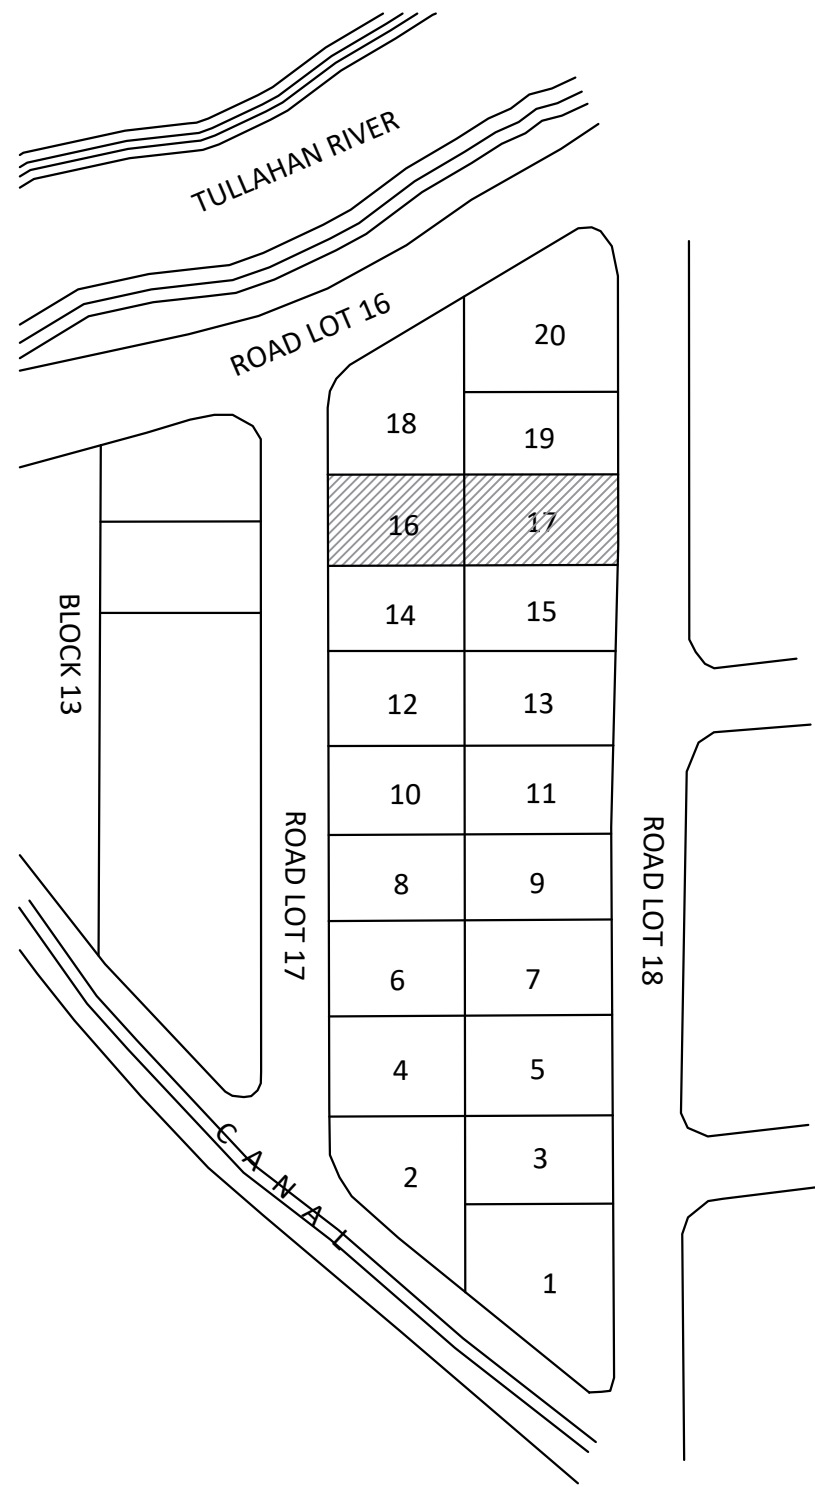

5  
A-01  
LOCATION MAP  
SCALE: NTS.

TABLE OF CONTENTS

| SHEET | CONTENT                                                                 |
|-------|-------------------------------------------------------------------------|
| A-01  | EXTERIOR PERSPECTIVE<br>VICINITY MAP<br>SDP<br>LOT PLAN<br>LOCATION MAP |
| A-02  | FLOOR PLAN                                                              |
| A-03  | FLOOR PLAN<br>ROOF PLAN                                                 |
| A-04  | CEILING PLAN                                                            |
| A-05  | DOORS & WINDOW SCHED.<br>DETAILS                                        |
| A-06  | ELEVATIONS<br>CROSS SECTION<br>LONGITUDINAL SECTION                     |

REPUBLIC OF THE PHILIPPINES  
DEPARTMENT OF PUBLIC WORKS & HIGHWAYS  
OFFICE OF THE BUILDING OFFICIAL

MALABON  
MUNICIPALITY/CITY

LAND USED AND ZONING

LINE AND GRADE

ARCHITECTURAL

STRUCTURAL

SANITARY

ELECTRICAL

MECHANICAL

MS. CINDY DE LUCIA

ARCHITECT

REANNE DENISE G. PE  
PRC NO. 43779 TIN: 339-409-843  
PTR NO: 0762964 DATE: 02/05/21  
PLACE: QUEZON CITY

IMPORTANT : THESE DRAWINGS, DESIGNS AND SPECIFICATIONS DULY SIGNED, STAMPED SEALED AS INSTRUMENT OF SERVICE, ARE THE PROPERTY AND DOCUMENTS OF THE ARCHITECT AND P.A.A.M.R.B.I.. WHETHER THE OBJECT FOR WHICH THEY ARE MADE IS EXECUTED OR NOT, IT SHALL BE UNLAWFULL FOR ANY PERSON W/OUT THE WRITTEN CONSENT OF P.A.A.M.R.B.I. TO DUPLICATE OR TO MAKE COPIES OF SAID DOCUMENTS FOR USE IN THE REPETITION OF AND FOR OTHER PROJECTS OR BUILDING, WHETHER EXECUTED PARTLY OR IN WHOLE. R.A. 545 Art. 4 Sec. 25

PROJECT TITLE  
**PROPOSED ARANETA RESIDENCE**  
LOCATION: LOT 16 AND 17, ARANETA VILLAGE, POTRERO, MALABON CITY, METRO MANILA.

NOTE: WRITTEN DIMENSIONS IN THIS DRAWINGS SHALL HAVE PRECEDENCE OVER SCALED DIMENSIONS. CONTRACTORS SHALL VERIFY AND BE RESPONSIBLE FOR ALL DIMENSIONS AT THE JOBSITE. THE DESIGNER MUST BE NOTIFIED IMMEDIATELY IN WRITING OF ANY VARIATIONS FROM THE DIMENSIONS AND THE CONDITIONS SHOWN BY THESE DOCUMENTS.

SHEET CONTENTS

**Perspective, Vicinity Map, SDP, Lot Plan  
and Location Map**

| R E V I S I O N S |               |
|-------------------|---------------|
|                   |               |
|                   |               |
|                   |               |
| DESIGNED BY: RDP  | DRAWN BY: RDP |
| CHECKED BY:       | APPROVED BY:  |

DRAWING NO.

1-5  
A-01

SHEET NO:

A-01