

LEGEND:

FF - 01 OUTDOOR STONE TILE

FF - 02 600 mm. X 600 mm. PORCELAIN TILE

FF - 03 300 mm. X 300 mm. NON- SKID CERAMIC TILE

FF - 04 800 mm. X 800 mm. NON- SKID CERAMIC TILE

FF - 05 WOOD PLANKS

FF - 06 600 mm. X 600 mm. NON- SKID CERAMIC TILE


FF - 07 600 mm. X 600 mm. NON- SKID CERAMIC TILE

FF - 08 VINYL WOOD PLANKS

FF - 09 VINYL WOOD TILES

1 SMOOTH PLASTER FINISH ON 150 mm. (6") THICK CHB

2 SMOOTH PLASTER FINISH ON 100 mm. (4") THICK DRY WALL

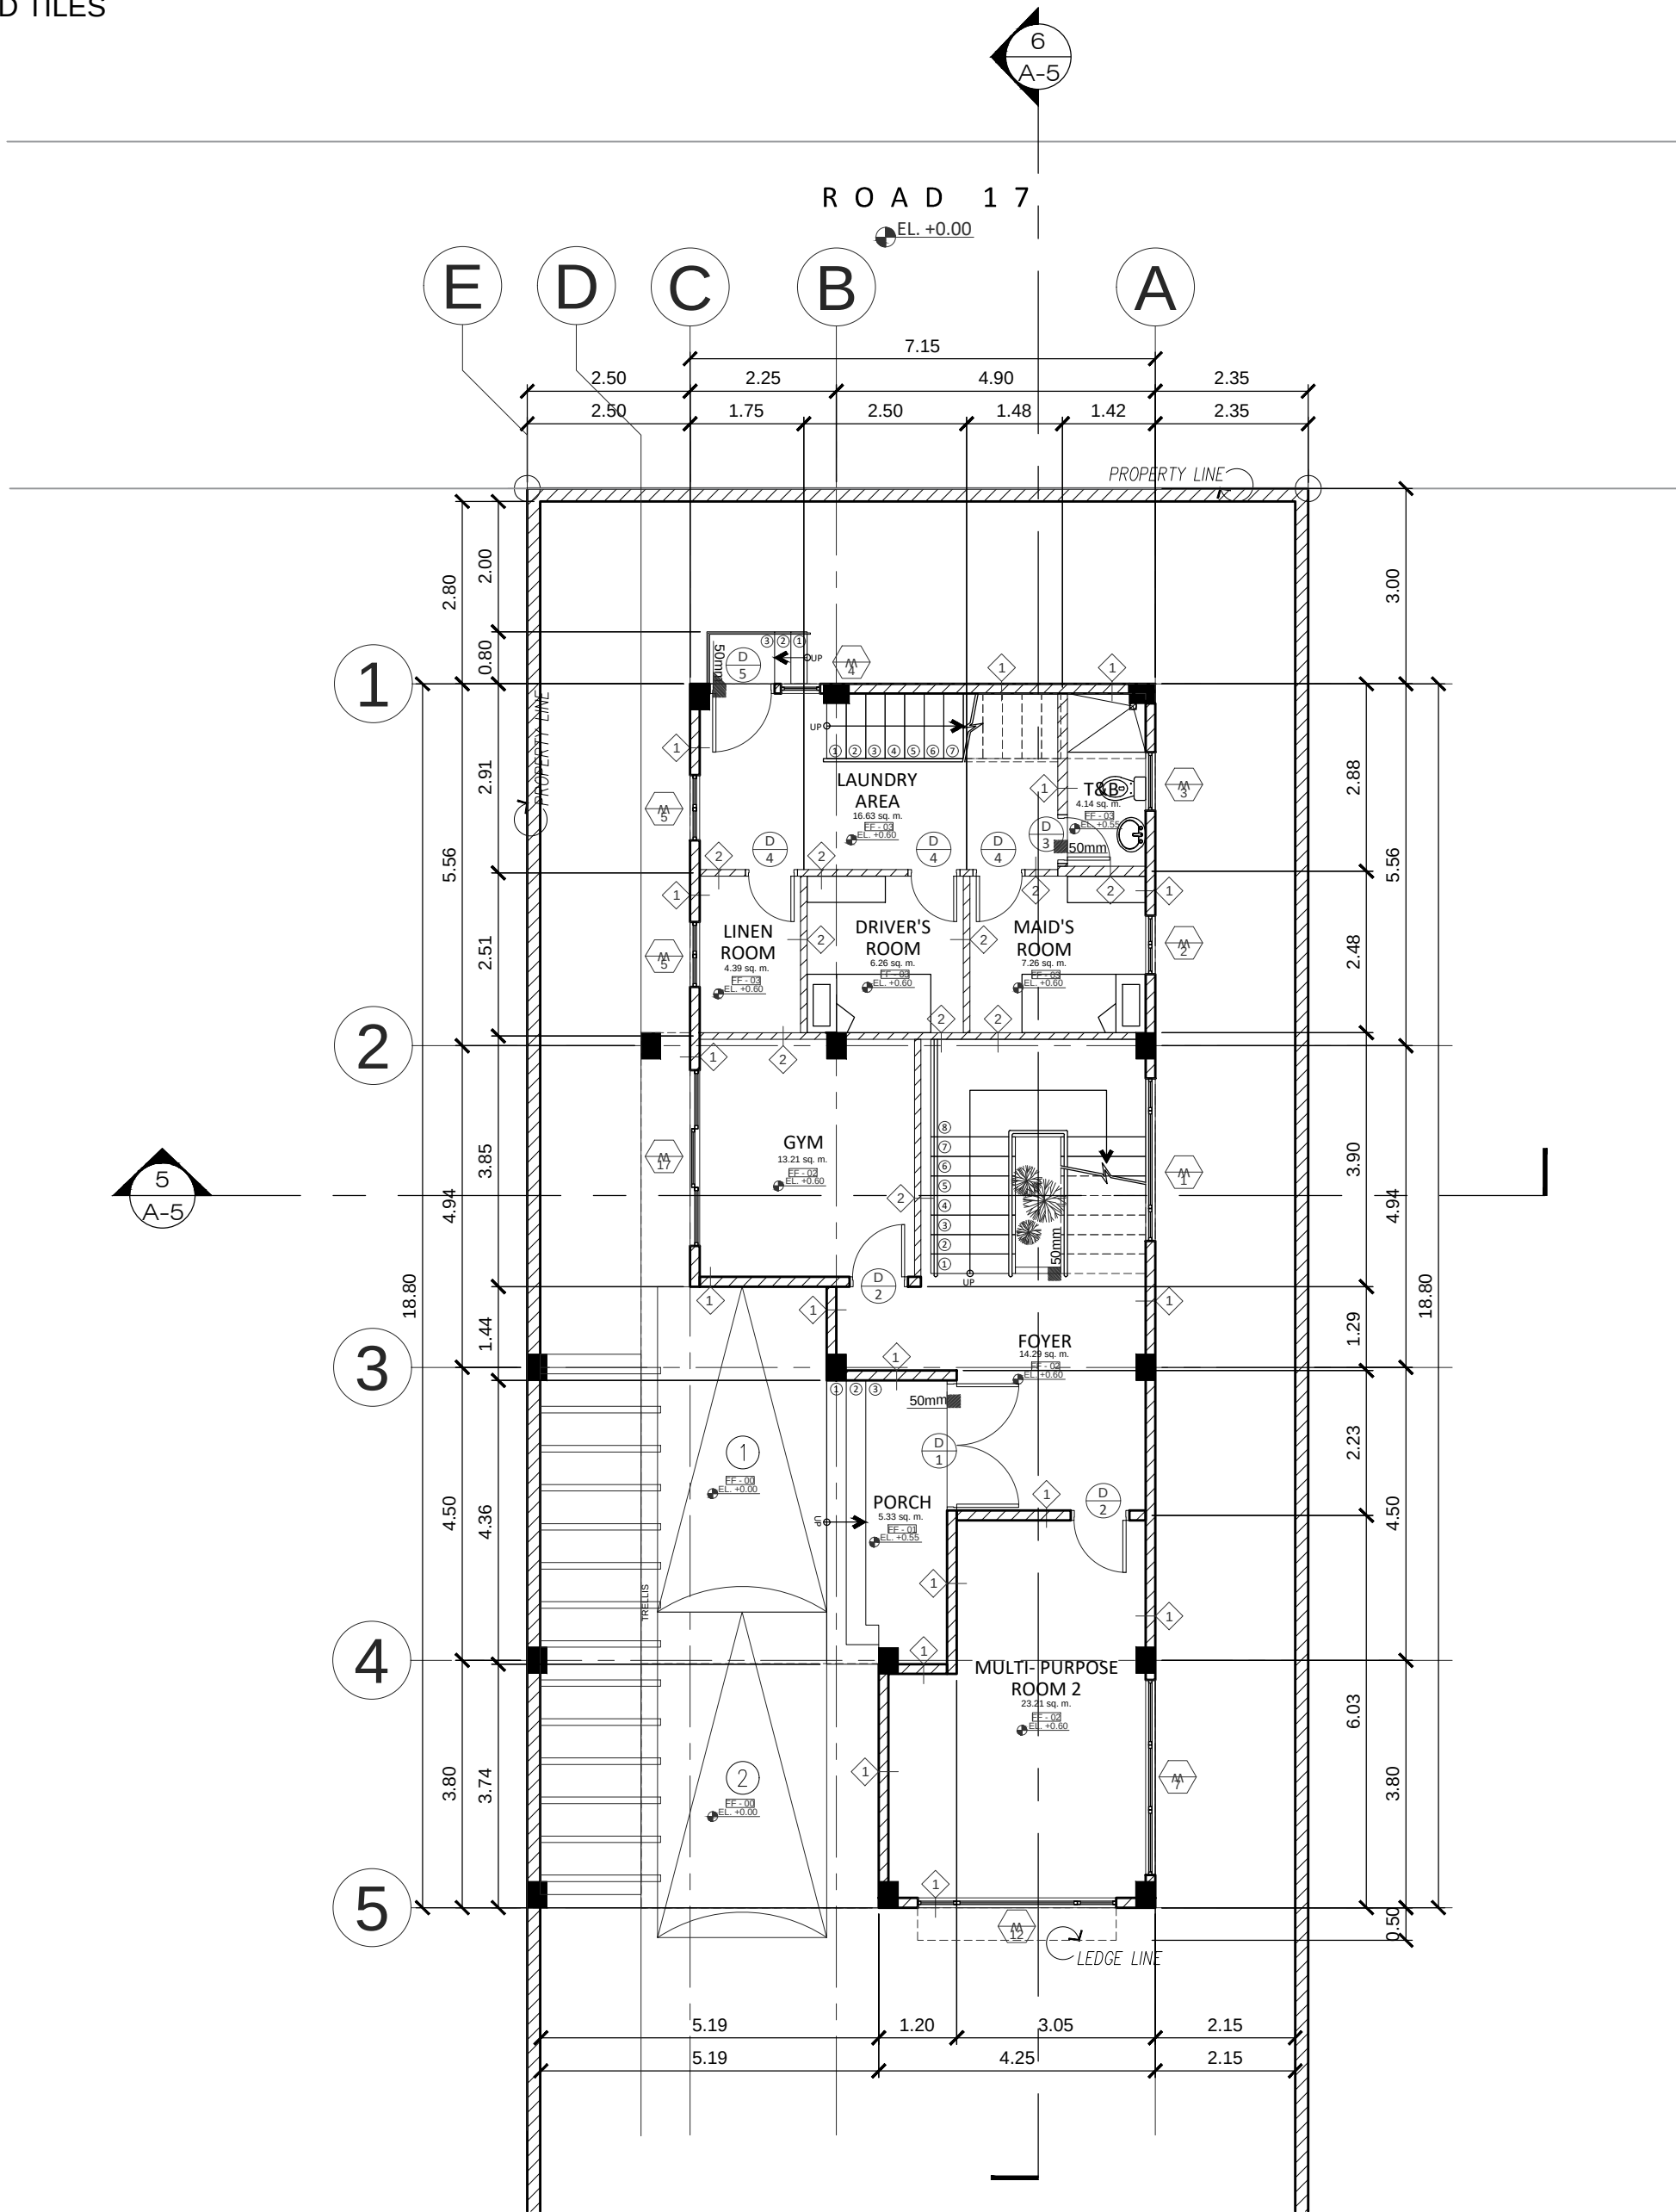


ARANETA RESIDENCE

1 GROUND FLOOR PLAN

SCALE:

1:100 MTS.

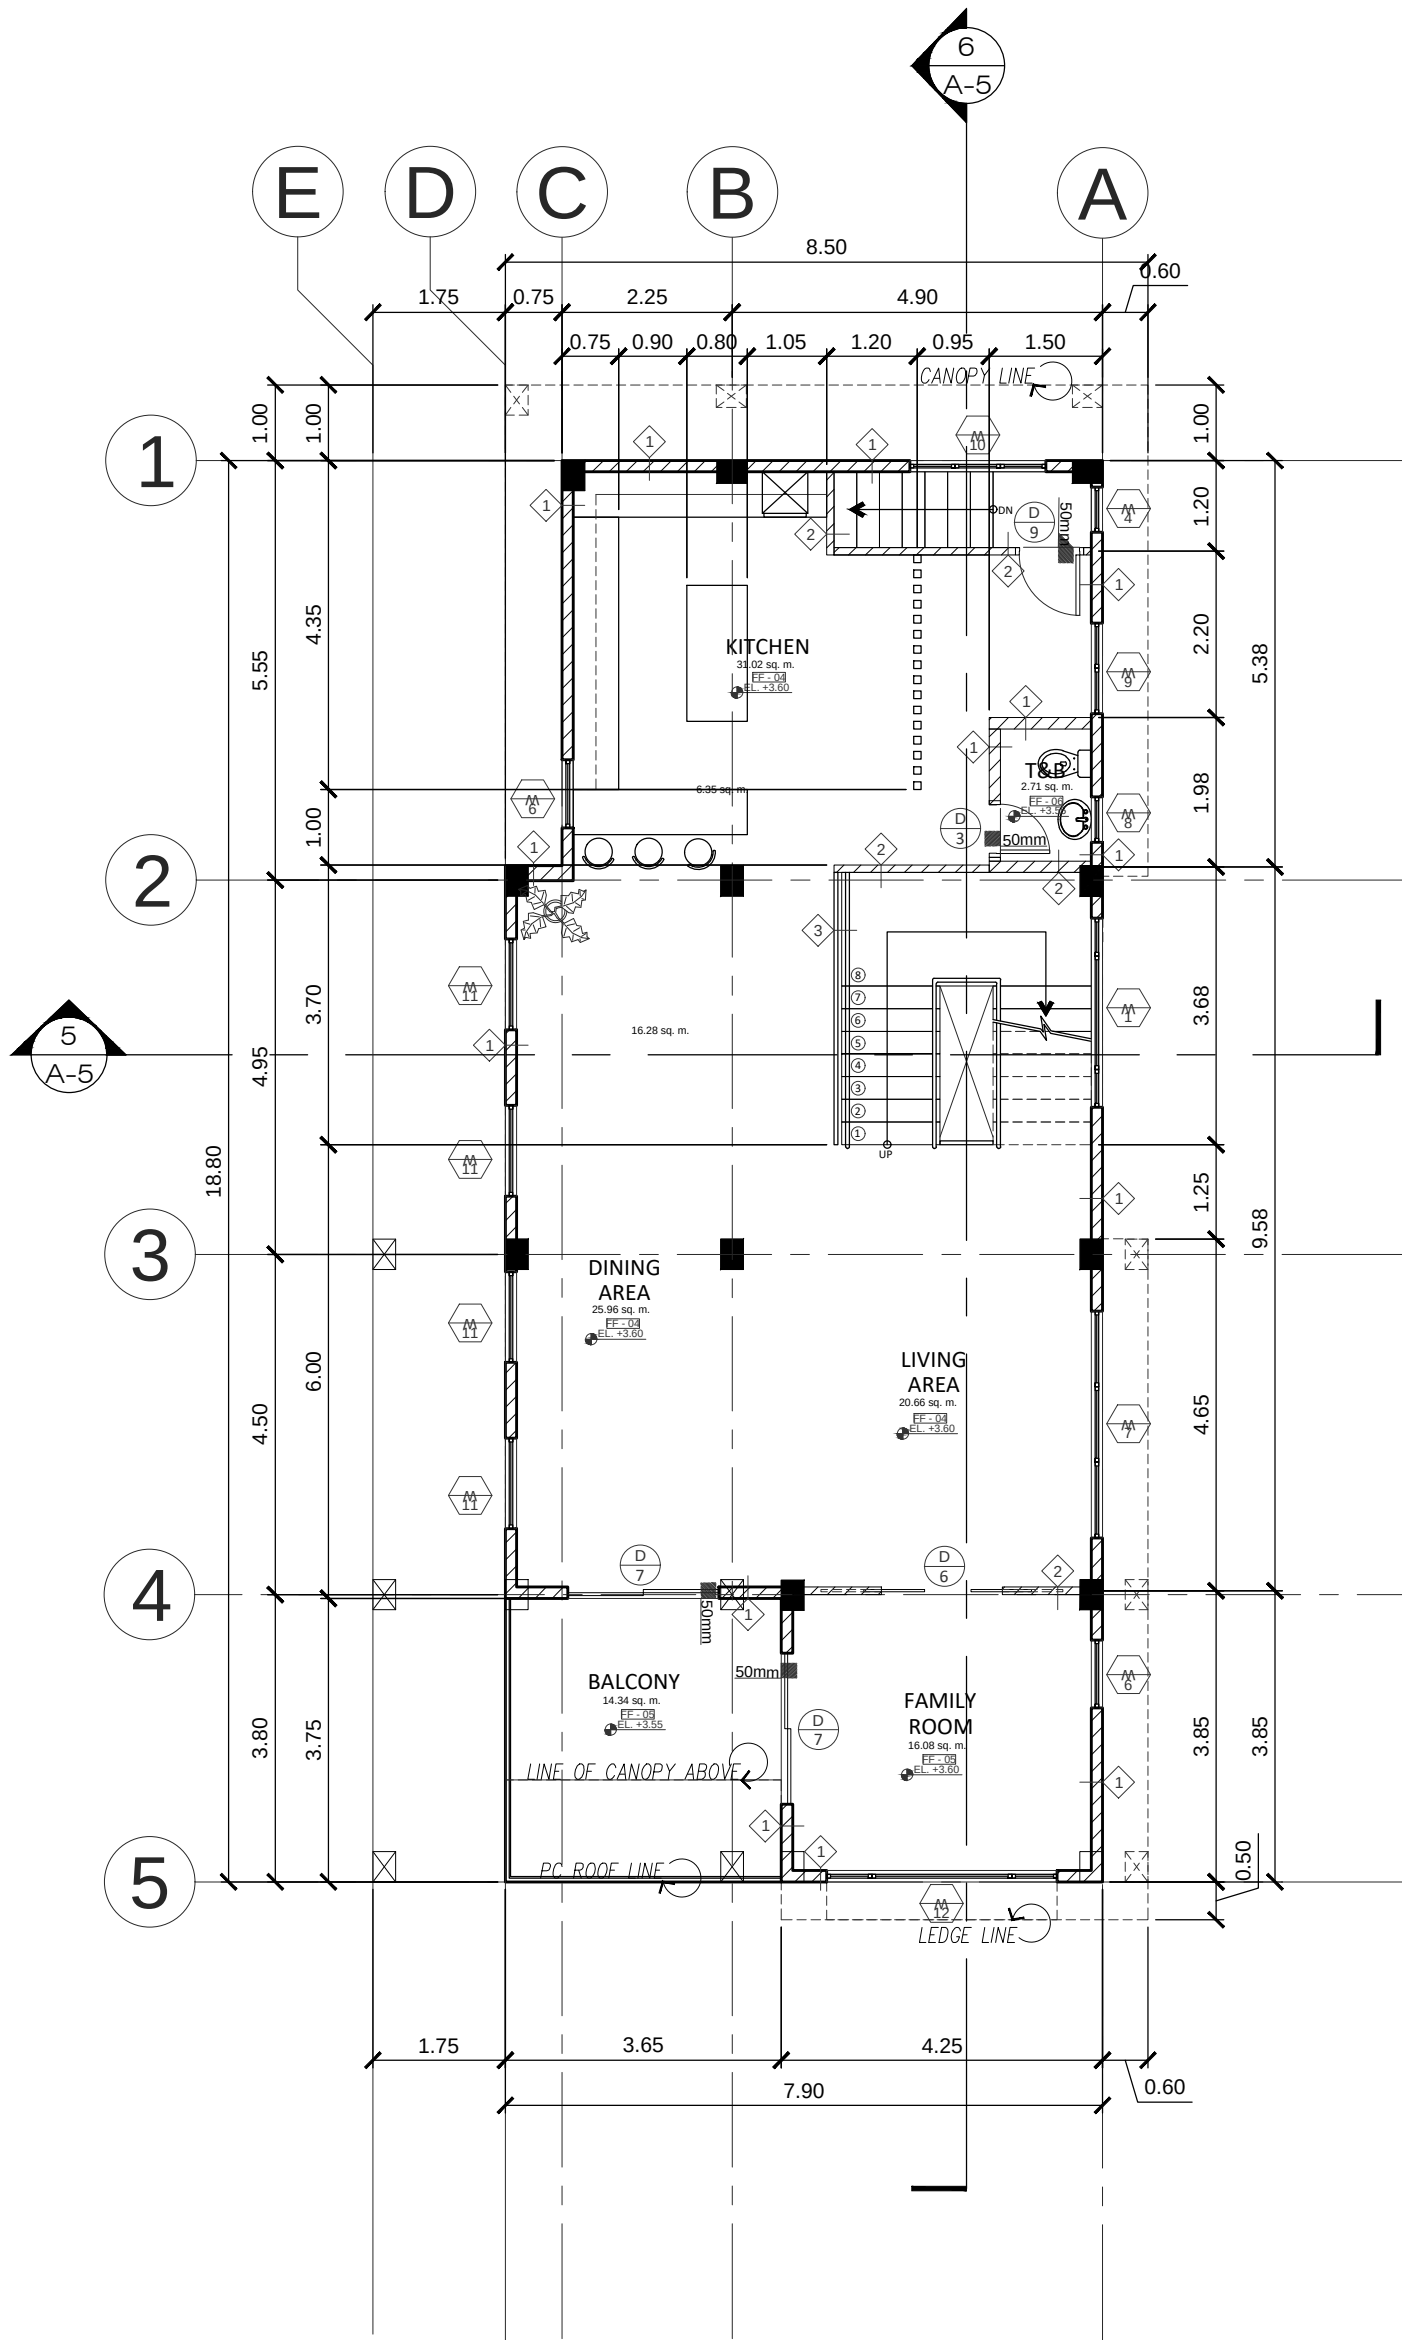

ARANETA RESIDENCE

2 SECOND FLOOR PLAN

SCALE:

1:100 MTS.

REPUBLIC OF THE PHILIPPINES
DEPARTMENT OF PUBLIC WORKS & HIGHWAYS
OFFICE OF THE BUILDING OFFICIAL

MALABON
MUNICIPALITY / CITY

NO. REVISIONS DATE

ALL WORKS SHALL BE CARRIED OUT IN ACCORDANCE WITH ALL BY LAWS AND CODES HAVING JURISDICTION OVER THIS SITE LOCATION. ALL DIMENSIONS AND INFORMATION SHALL BE CHECKED AND VERIFIED ON THE JOB AND ANY VARIANCES TO THE ARCHITECT.

THESE DRAWINGS MUST NOT BE SCALED. THE DESIGN AND CONTRACT DOCUMENTS ARE THE COPYRIGHT PROPERTY OF THE ARCHITECT AND MAY NOT BE REPRODUCED, ALTERED OR REUSED WITHOUT THE ARCHITECTS WRITTEN AUTHORITY.

SANITARY

PRC. NO. T.J.N. DATE:

PTR. NO. PLACE: DATE:

MECHANICAL

PRC. NO. T.J.N. DATE:

PTR. NO. PLACE: DATE:

ELECTRICAL

PRC. NO. T.J.N. DATE:

PTR. NO. PLACE: DATE:

STRUCTURAL

PRC. NO. T.J.N. DATE:

PTR. NO. PLACE: DATE:

ARCHITECT

REANNE DENISE G. PE

PRC. NO. T.J.N. DATE:

PTR. NO. PLACE: DATE:

OWNER

MS. CINDY DE LUCIA

PROJECT:

PROPOSED
ARANETA RESIDENCE
LOT 16 AND 17, ARANETA VILLAGE,
POTRIERO, MALABON CITY, METRO MANILA.

SHEET CONTENT:

FLOOR PLAN

DESIGN: RDP SCALE: 1:100 SHEET NO. A-02

DRAWN: RDP DATE: 01/02/22