

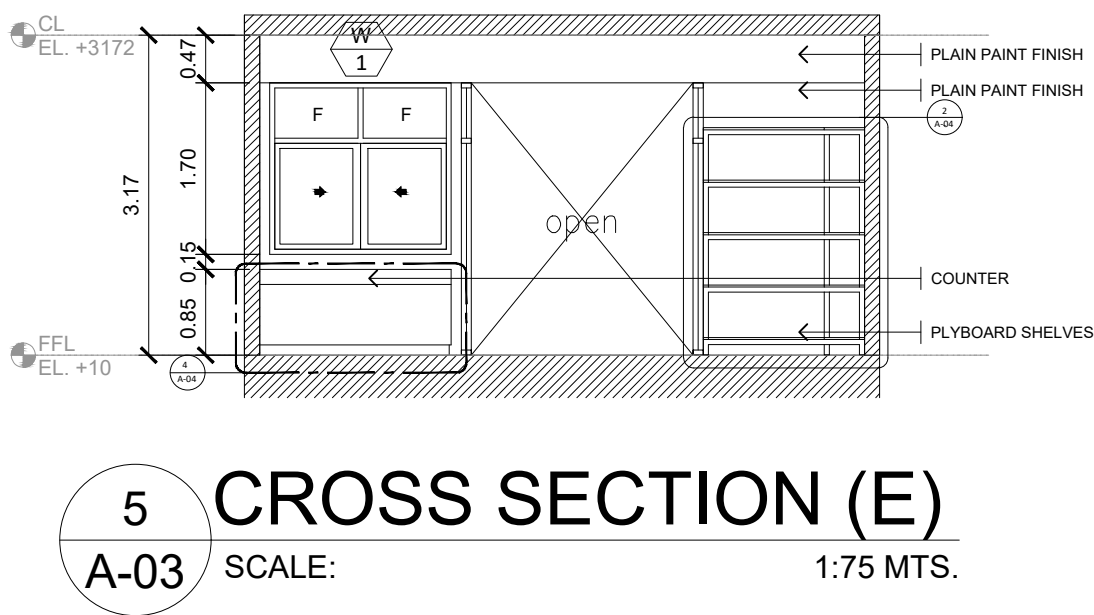
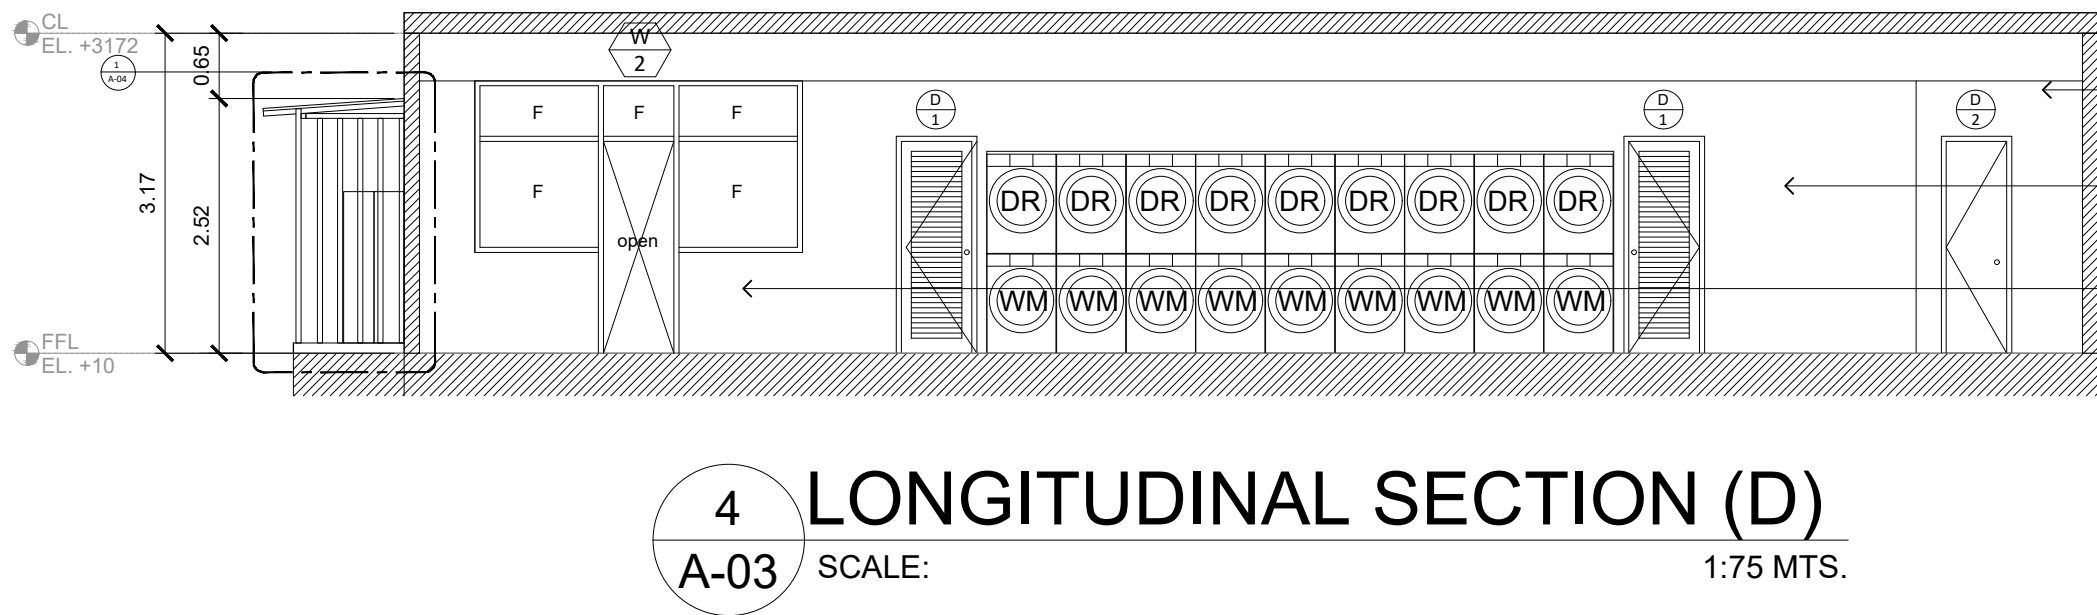
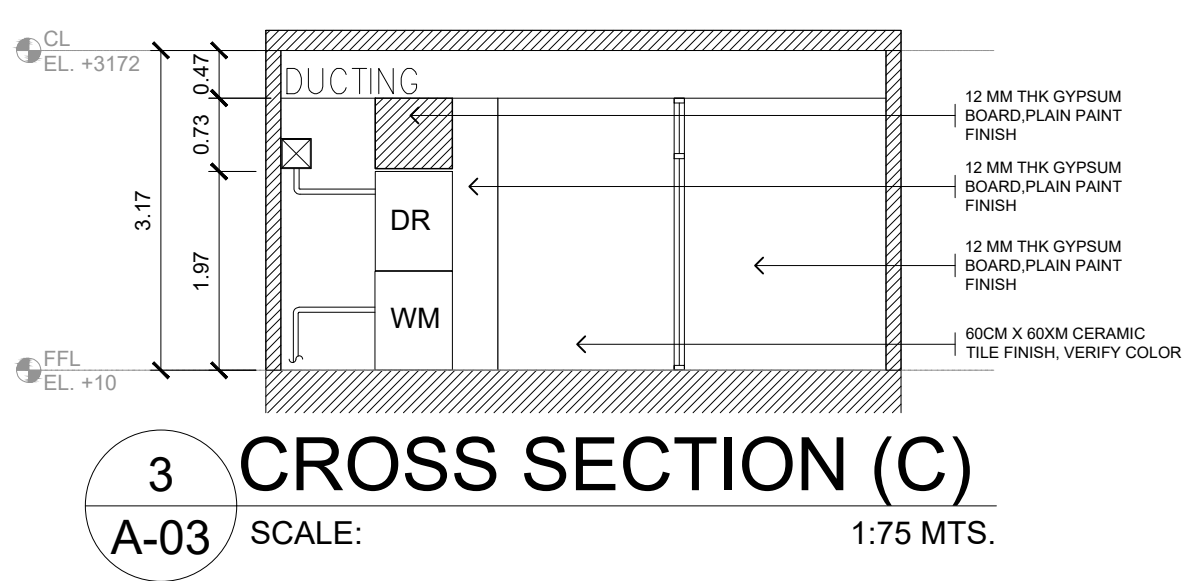
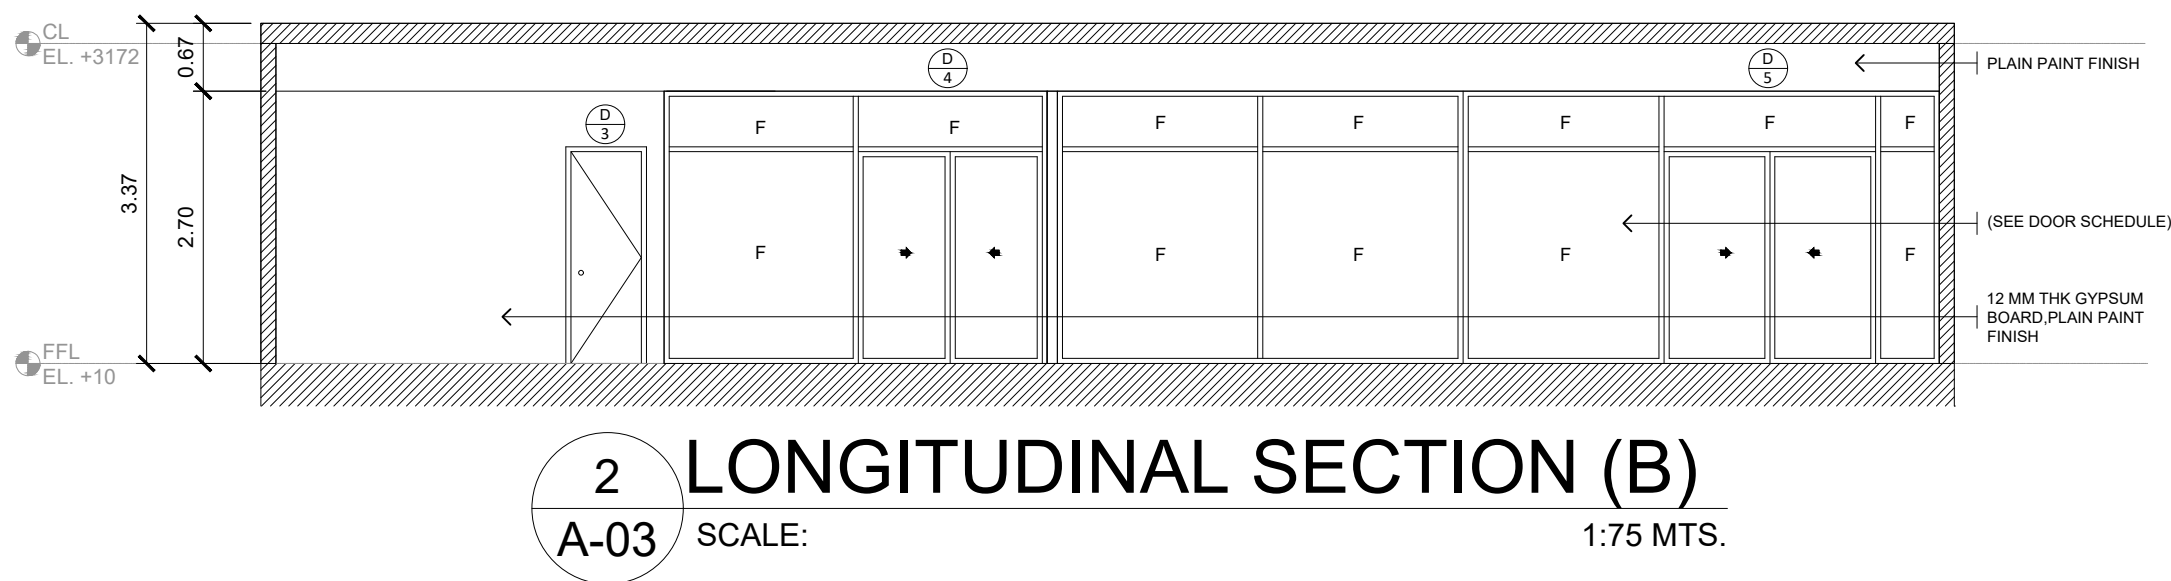


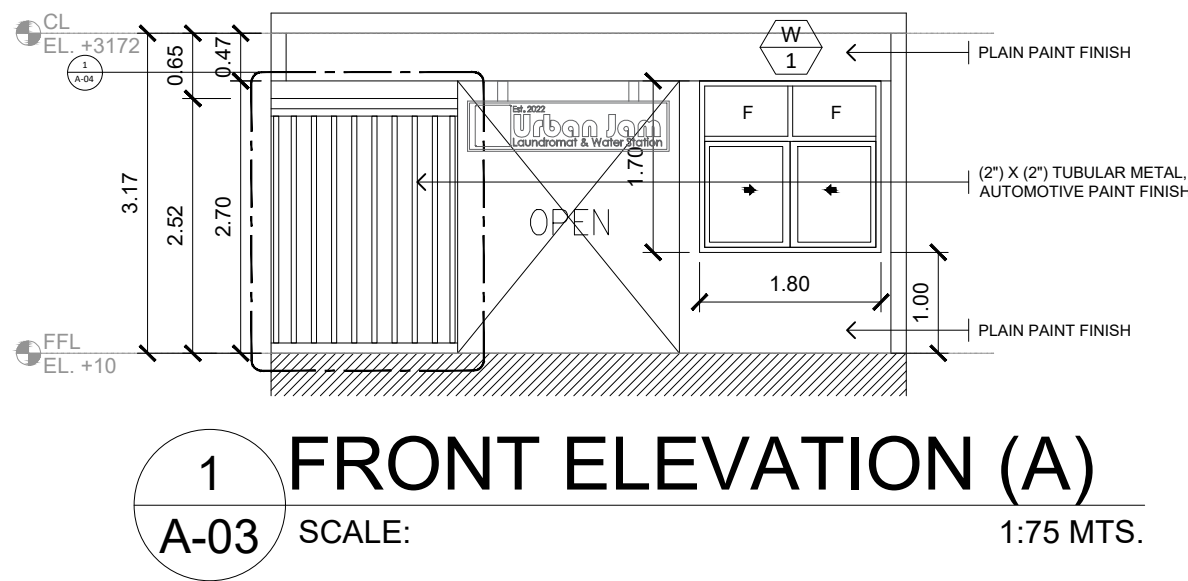

SCHEDULE OF WINDOWS		
LOCATION	WATER STATION	STORAGE AREA
SPECIFICATIONS	6mm THK TEMPERED GLASS SLIDING WINDOW W/ FIXED PANELS	6mm THK TEMPERED GLASS FIXED WINDOW
FRAME	PLAIN FINISH POWDER COATED ALUMINUM FRAME (VERIFY COLOR)	PLAIN FINISH POWDER COATED ALUMINUM FRAME (VERIFY COLOR)
QUANTITY	1 SET	1 SET

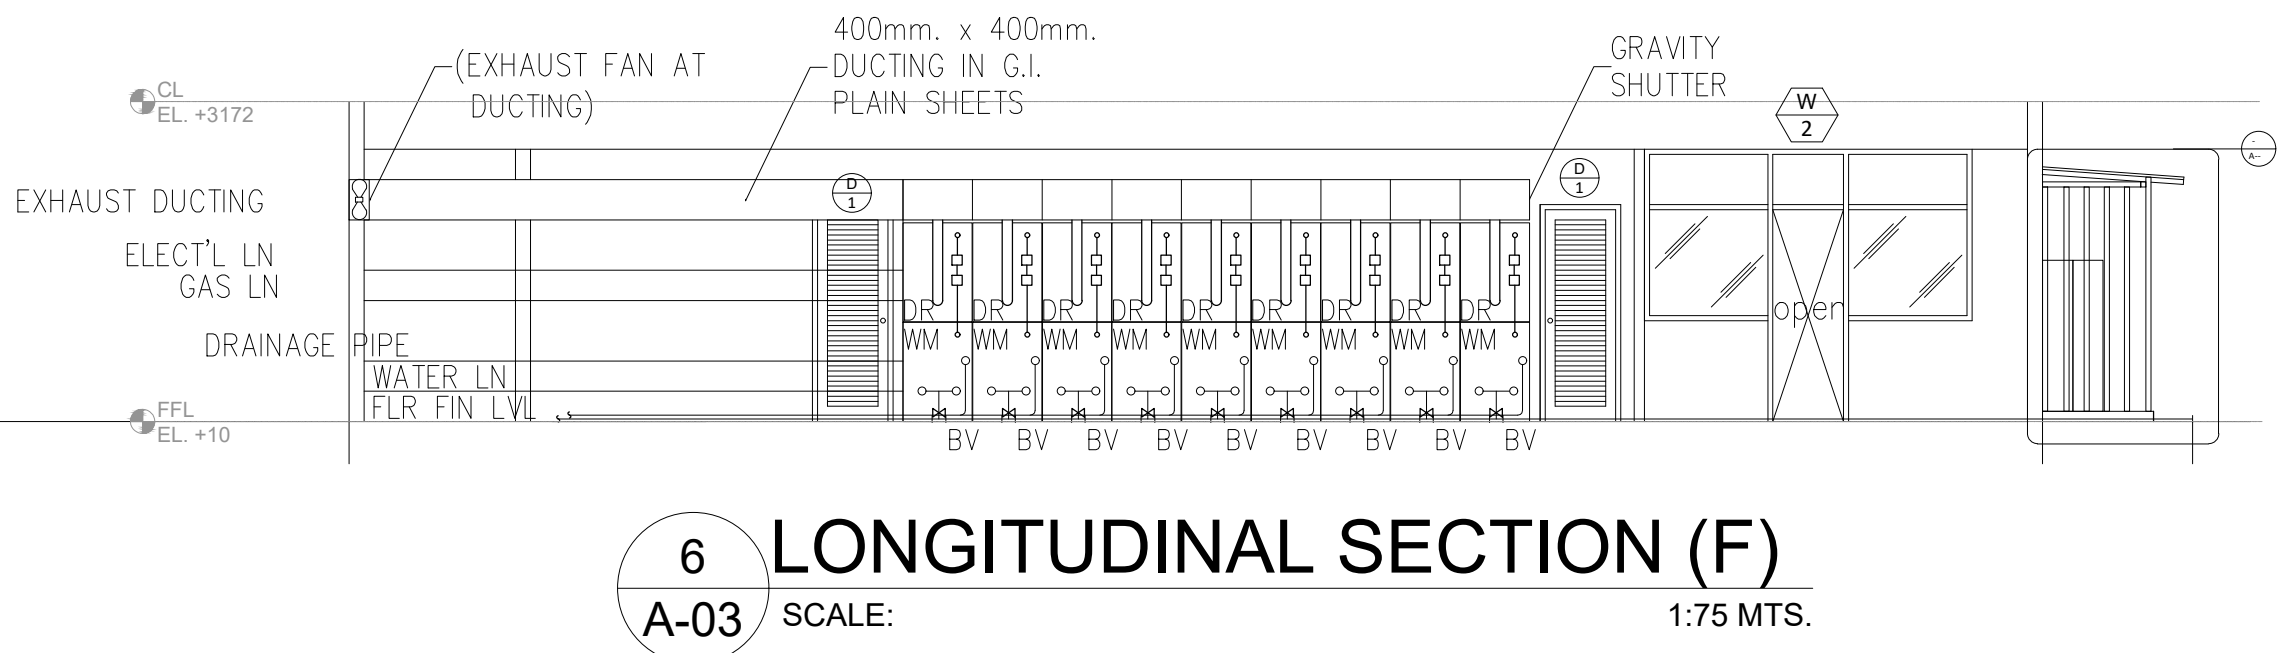

SCHEDULE OF DOORS					
LOCATION	WET AREA	T&B	ROOM 1	OFFICE	WATER STATION
SPECIFICATIONS	PVC DOOR	PVC DOOR	SOLID WOODEN FLUSH DOOR IN VARNISH FINISH	12mm THK CLEAR TEMPERED GLASS SLIDING DOOR	12mm THK CLEAR TEMPERED GLASS SLIDING DOOR
FRAME	2" x 4" PVC DOOR JAMB	2" x 4" PVC DOOR JAMB	2" x 4" KD WOODEN DOOR JAMB IN VARNISH FINISH	POWDER COATED ALUMINUM FRAME (VERIFY COLOR)	POWDER COATED ALUMINUM FRAME (VERIFY COLOR)
QUANTITY	2 SETS	1 SET	1 SET	1 SET	1 SET

8 SCHEDULE OF DOORS
A-03 SCALE: NTS.

