
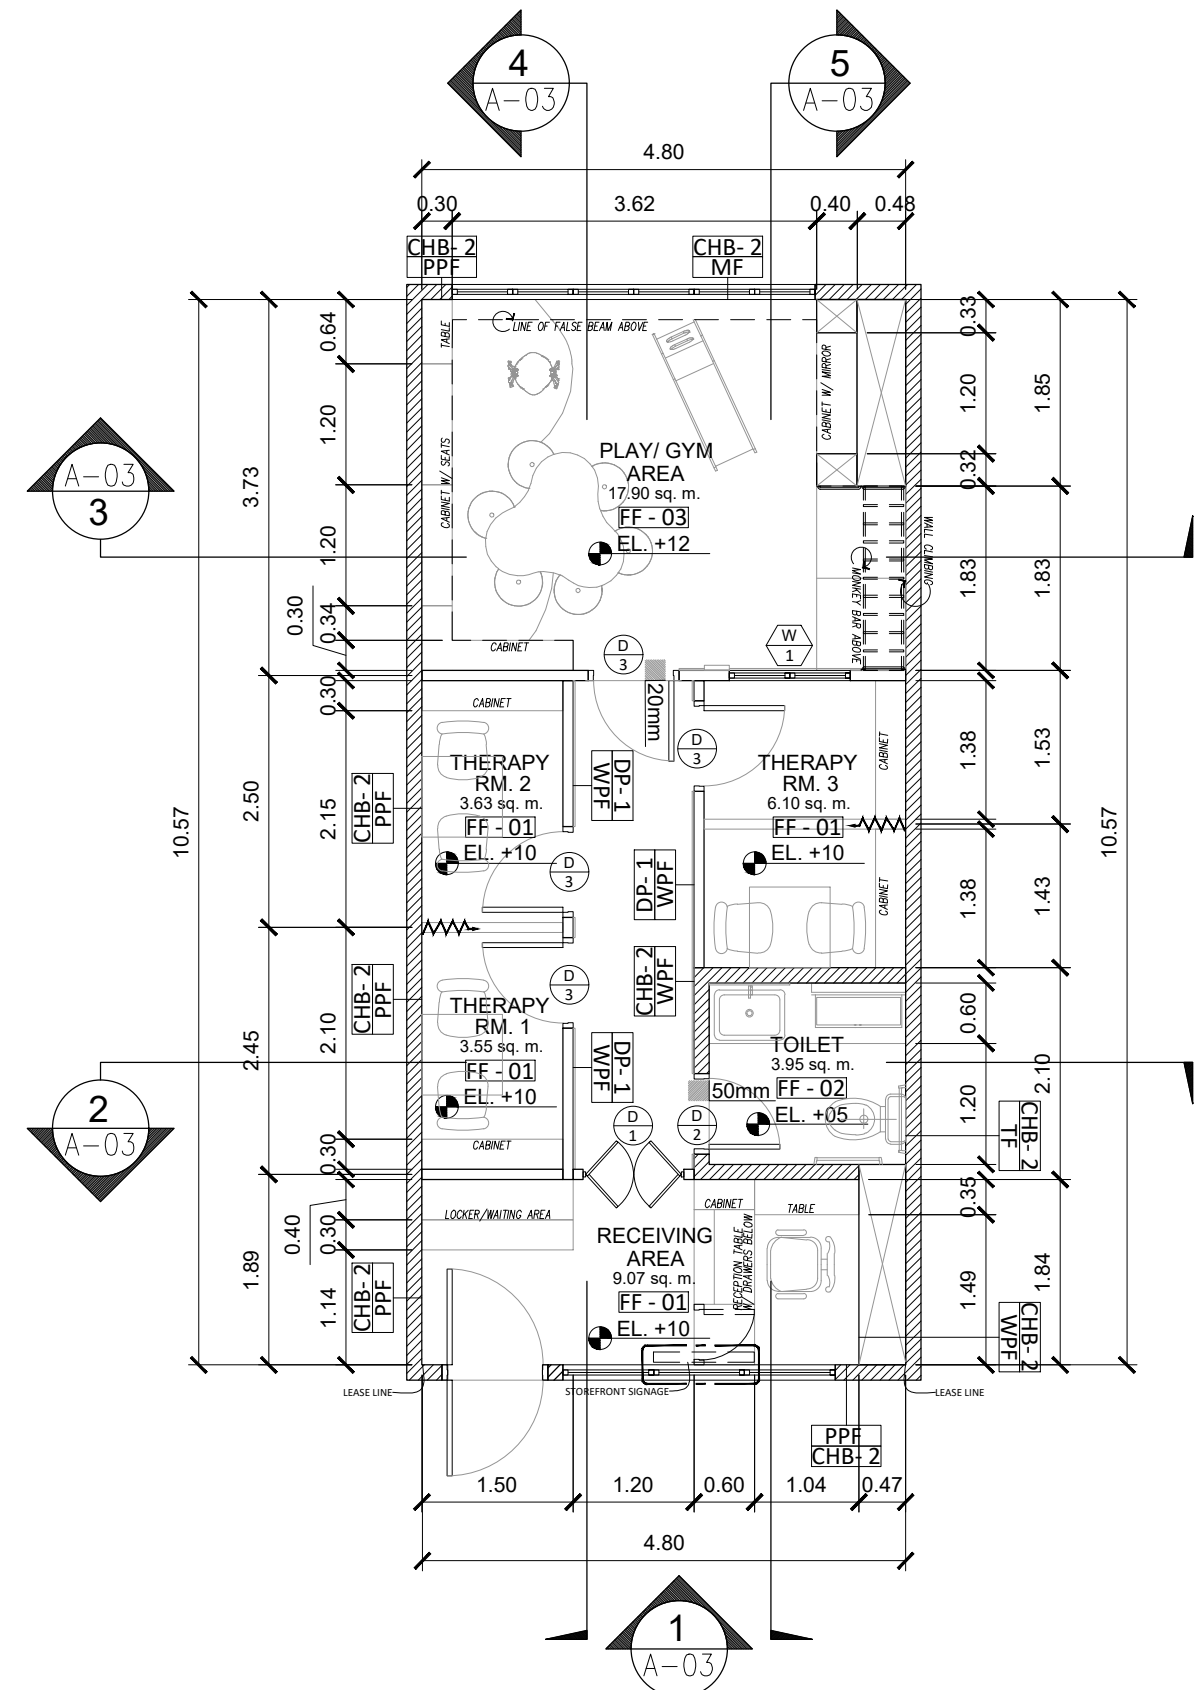
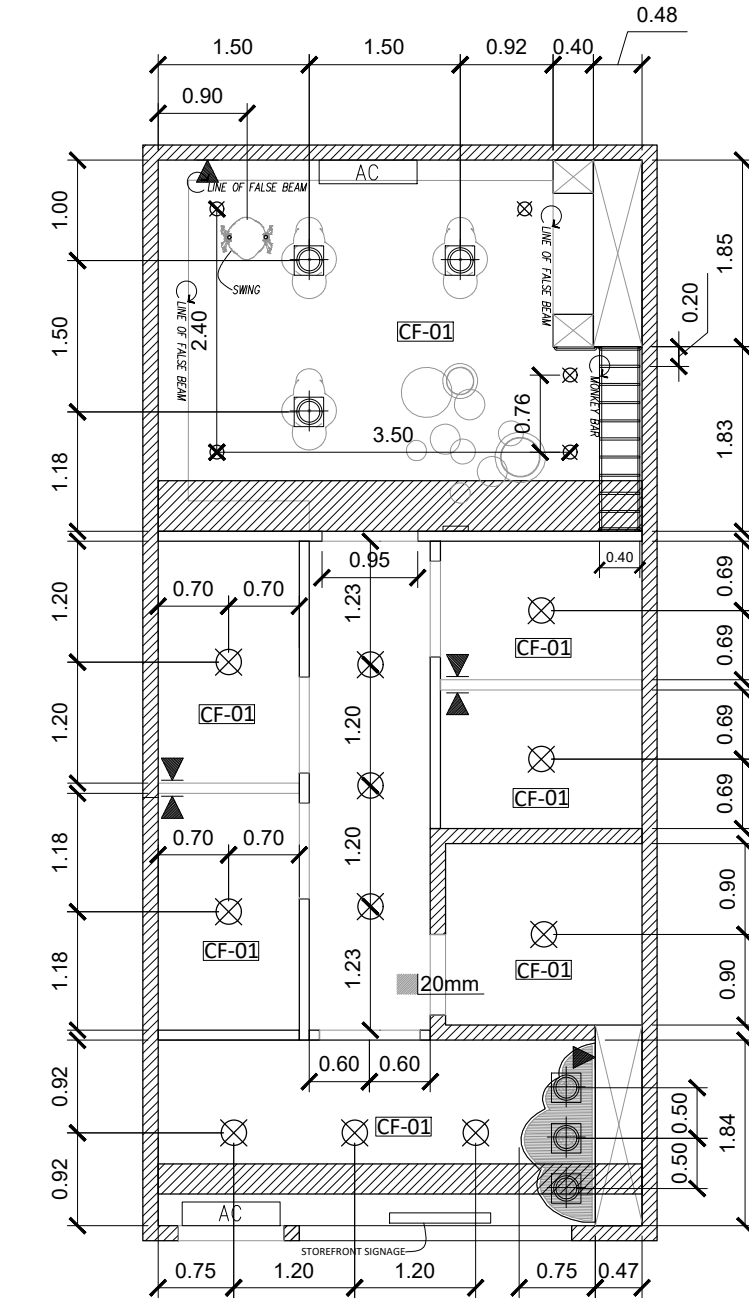
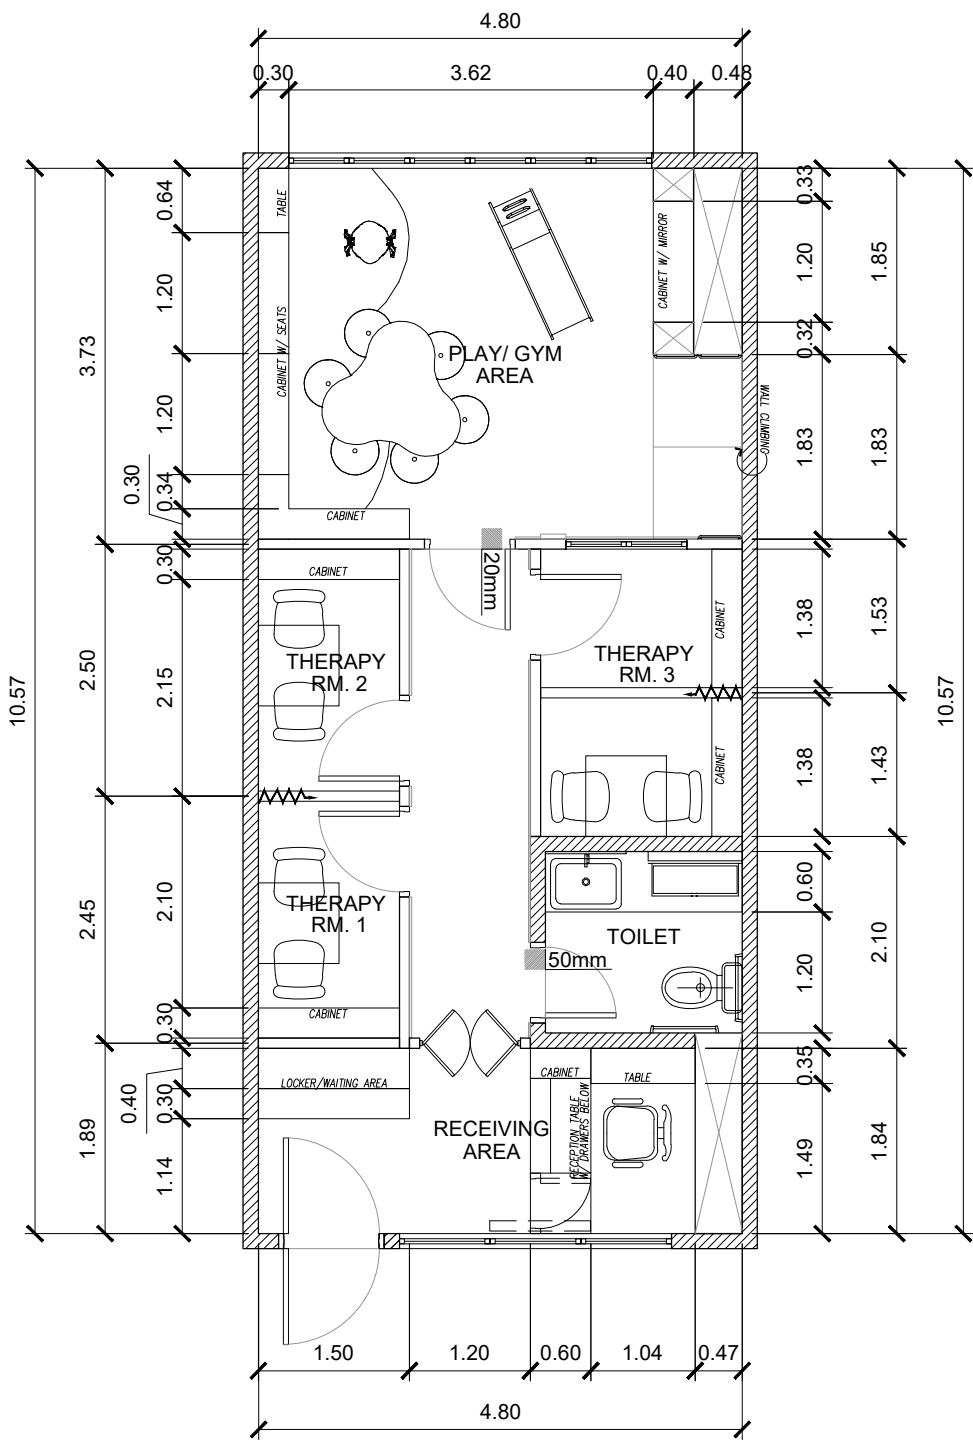


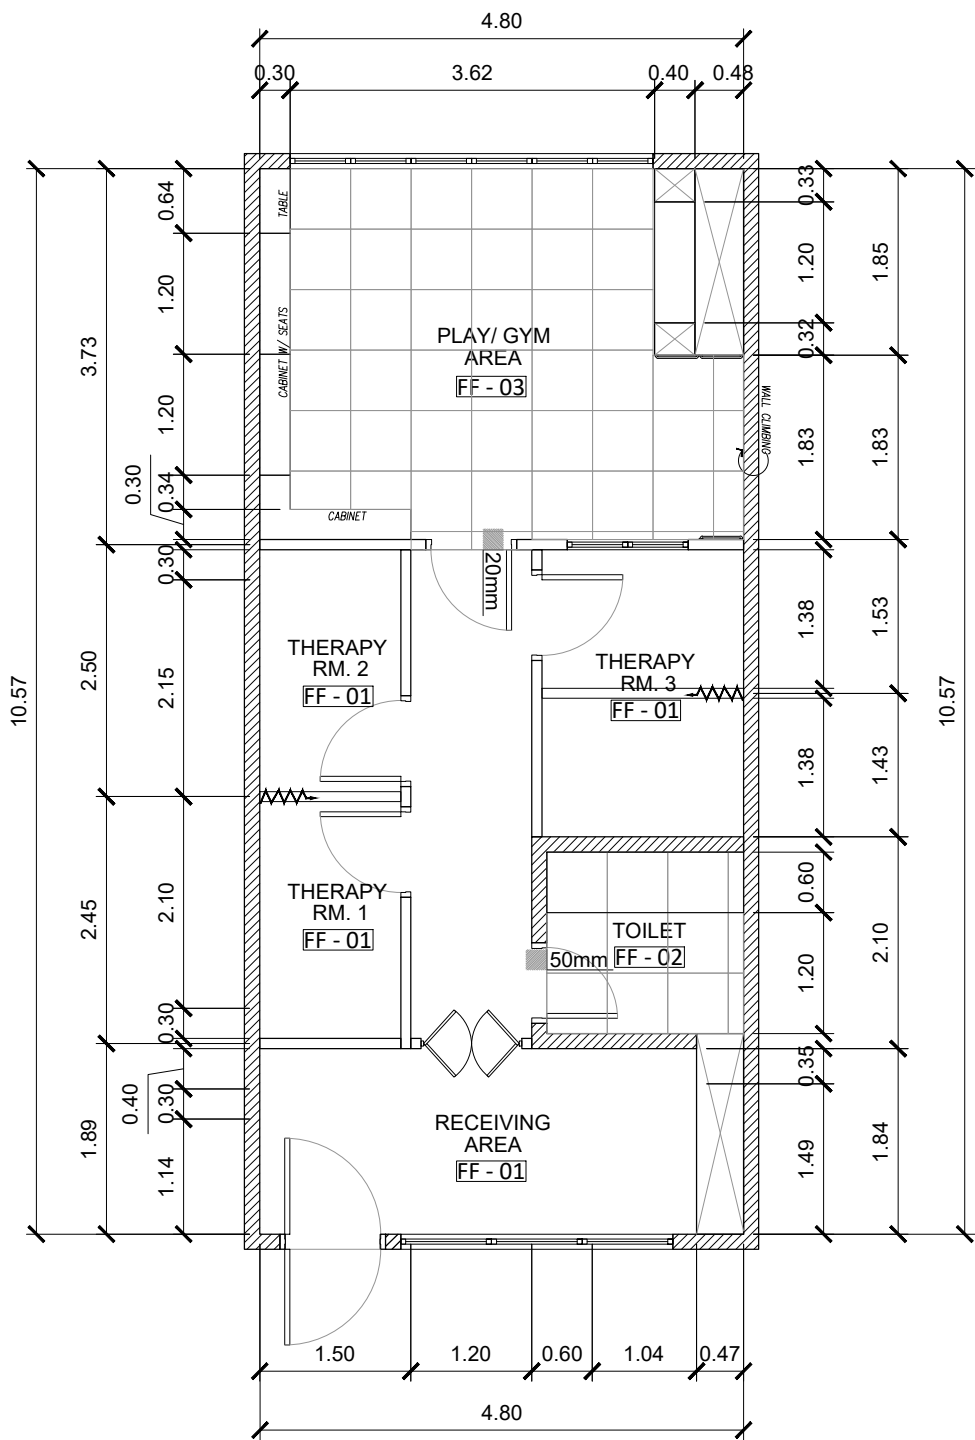

1 FLOOR FINISH LAYOUT
A-02 SCALE: 1:75 MTS.

2 FURNITURE LAYOUT
A-02 SCALE: 1:75 MTS.

3 REFLECTED CEILING PLAN
A-02 SCALE: 1:75 MTS.

4 GROUND FLOOR PLAN
A-02 SCALE: 1:75 MTS.

SCHEDULE OF DOORS AND WINDOW				
	D 1	D 2	D 3	W 1
LOCATION	RECEIVING AREA, HALLWAY	TOILET	THERAPY ROOMS 1, 2 & 3, PLAY/ GYM AREA	THERAPY RM. 3, PLAY/ GYM AREA
SPECIFICATIONS	8MM THK CLEAR TEMPERED GLASS DOUBLE SWING DOOR IN POWDER COATED ALUMINUM FRAMING	WOODEN FLUSH DOOR	SOLID WOODEN FLUSH DOOR IN VARNISH FINISH	8MM THK ONE WAY MIRROR FIXED PANELS
FRAME	POWDER COATED ALUMINUM FRAME (VERIFY COLOR)	2" x 6" KID WOODEN DOOR JAMB IN VARNISH FINISH	2" x 4" KID WOODEN DOOR JAMB IN VARNISH FINISH	FRAMELESS
QUANTITY	1 SET	1 SET	4 SETS	1 SET

5 SCHEDULE OF DOORS AND WINDOW
A-02 SCALE: NTS.

LEGEND:

FF - 01	WOOD LAMINATE COLOR TO BE VERIFIED
FF - 02	60 CM X 60 CM NON SKID CERAMIC TILE (W/ WATERPROOFING) COLOR TO BE VERIFIED
FF - 03	INTERLOCKING FOAM FLOOR TILES COLOR TO BE VERIFIED
CHB- 1	CONCRETE HOLLOW BLOCK 4"
CHB- 2	CONCRETE HOLLOW BLOCK 6"
DP- 1	DRYWALL 4"
TF	TILED FINISH
MF	MIRROR FINISH (FACIAL)
WPF	WALLPAPER FINISH
PPF	PLAIN PAINT FINISH

CEILING FINISHES:

CF-01	EXPOSED SLAB AND BEAM, PAINTED FINISH.
-------	--

LIGHTING FIXTURES:

	PENDANT LIGHT
	SURFACED: 200 mm. Ø DOWN LIGHT
	CCTV