




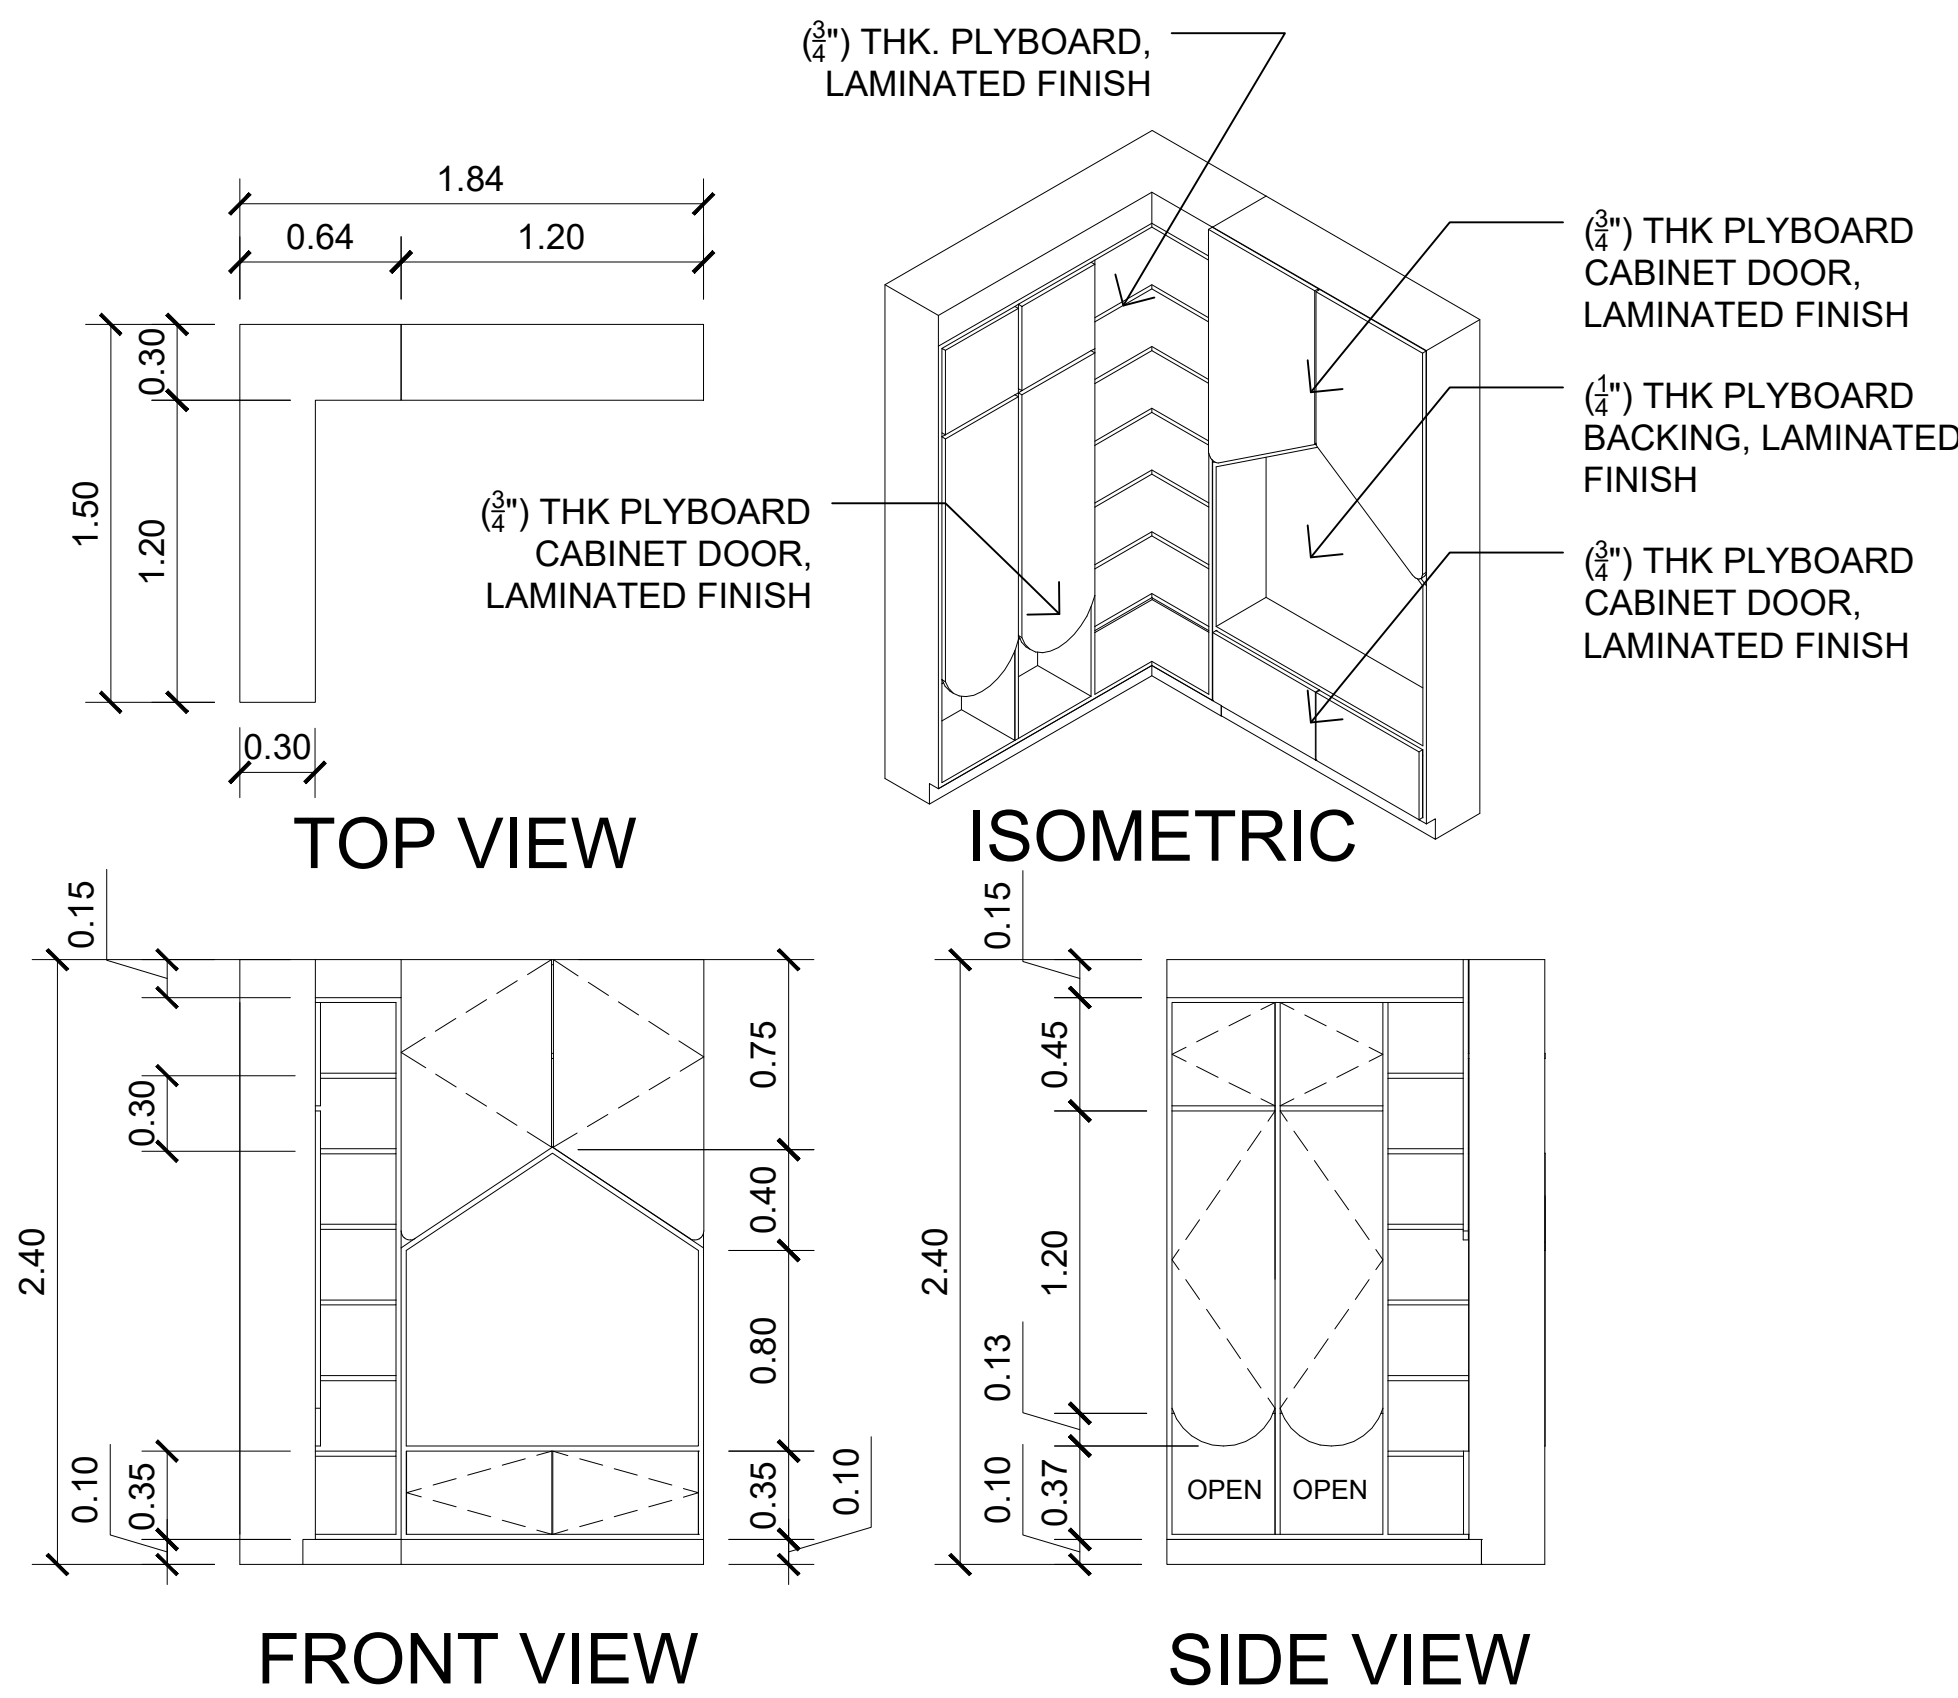


1 BLOW-UP DETAIL (A)
A-04 SCALE: 1:30 MTS.

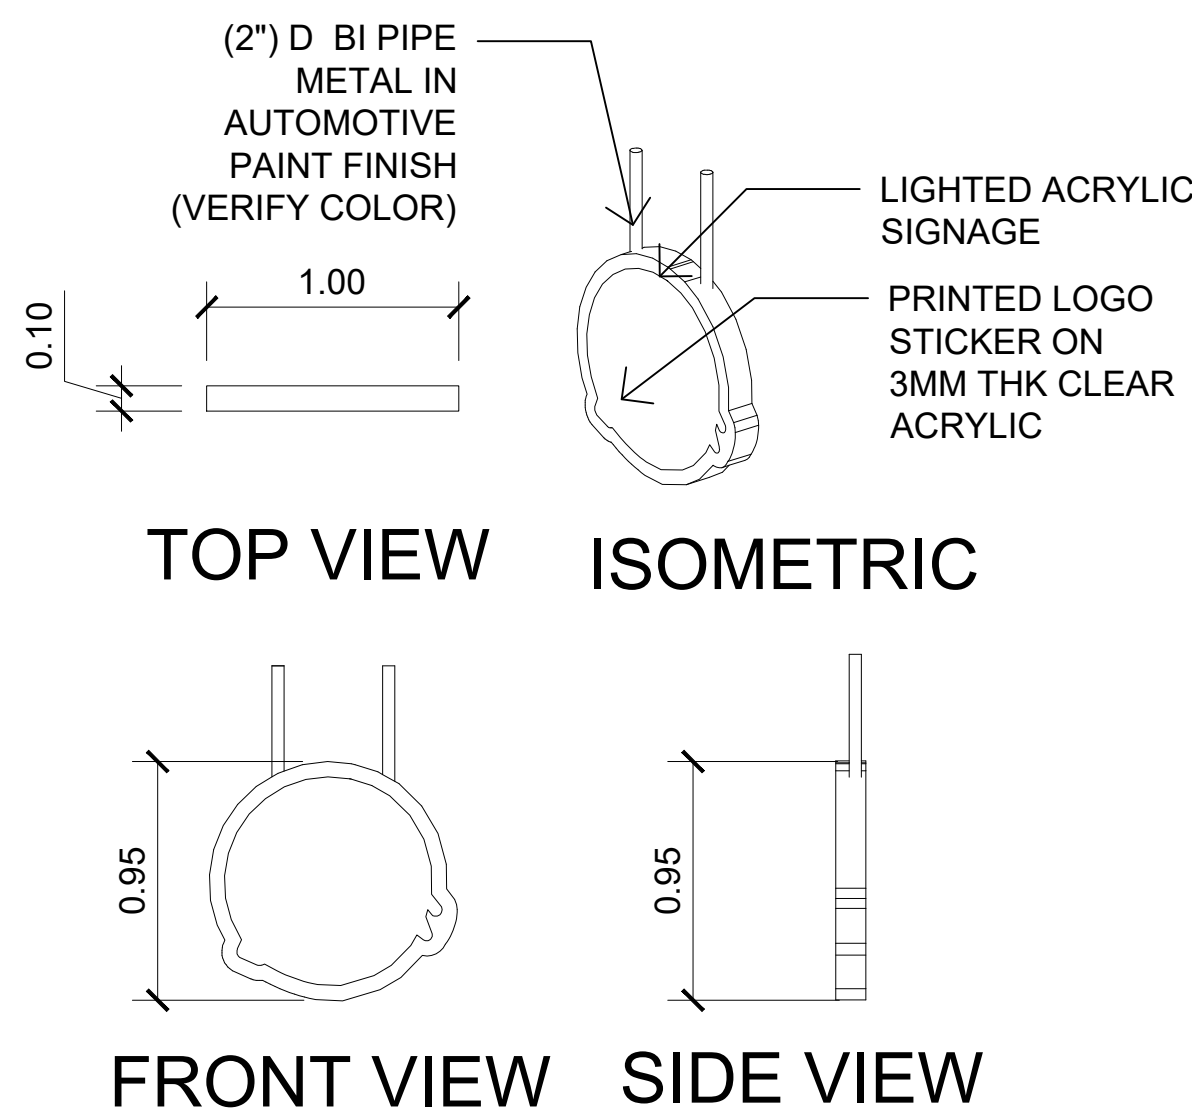

3 STOREFRONT SIGNAGE BLOW-UP DETAIL (C)
A-04 SCALE: 1:30 MTS.

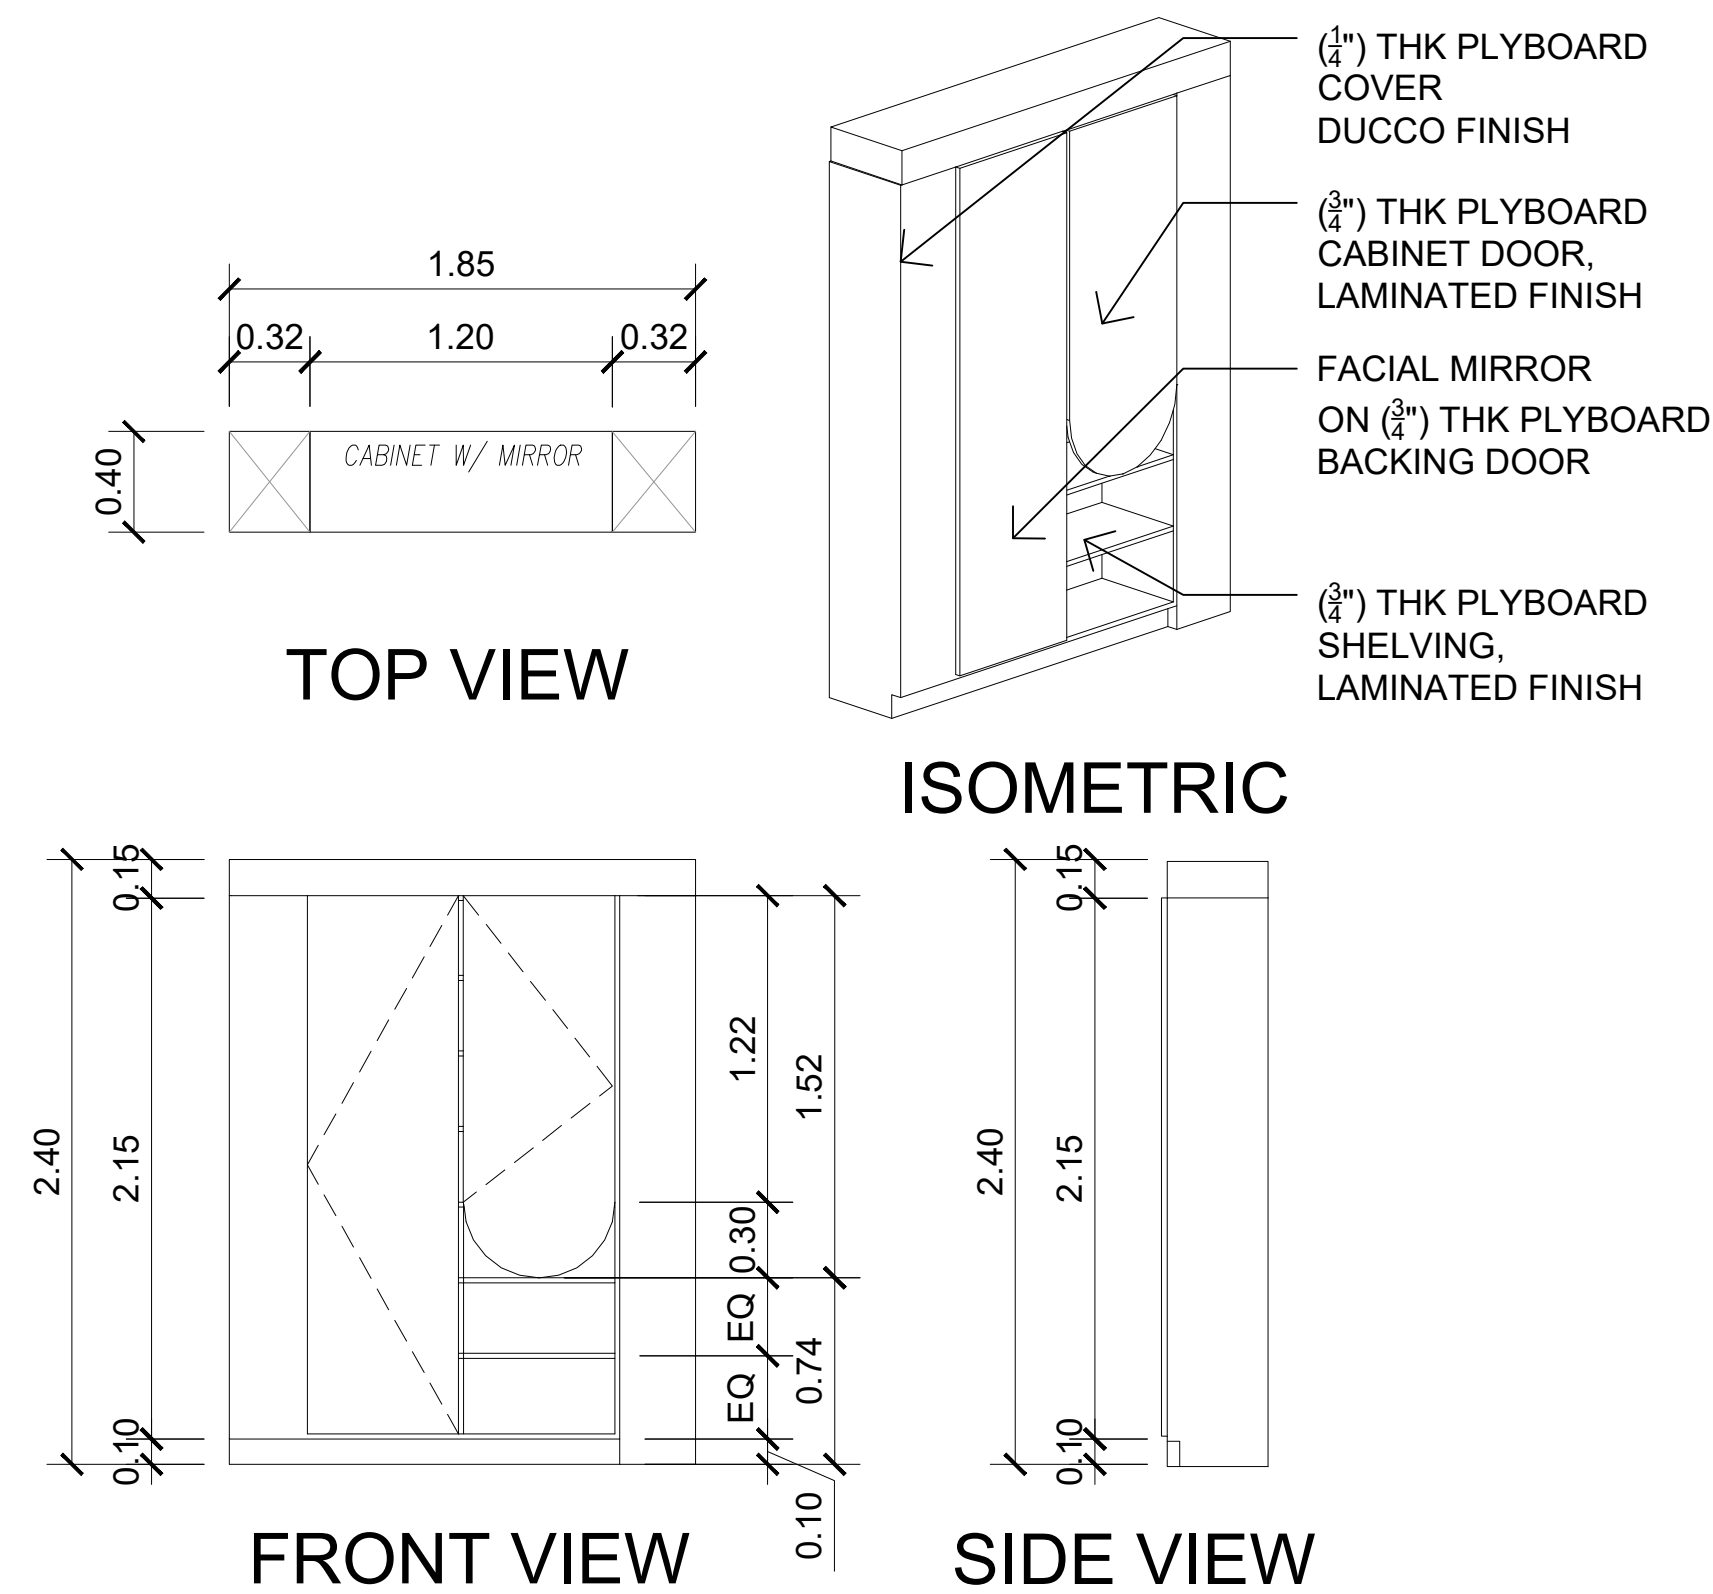

2 BLOW-UP DETAIL (B)
A-04 SCALE: 1:30 MTS.

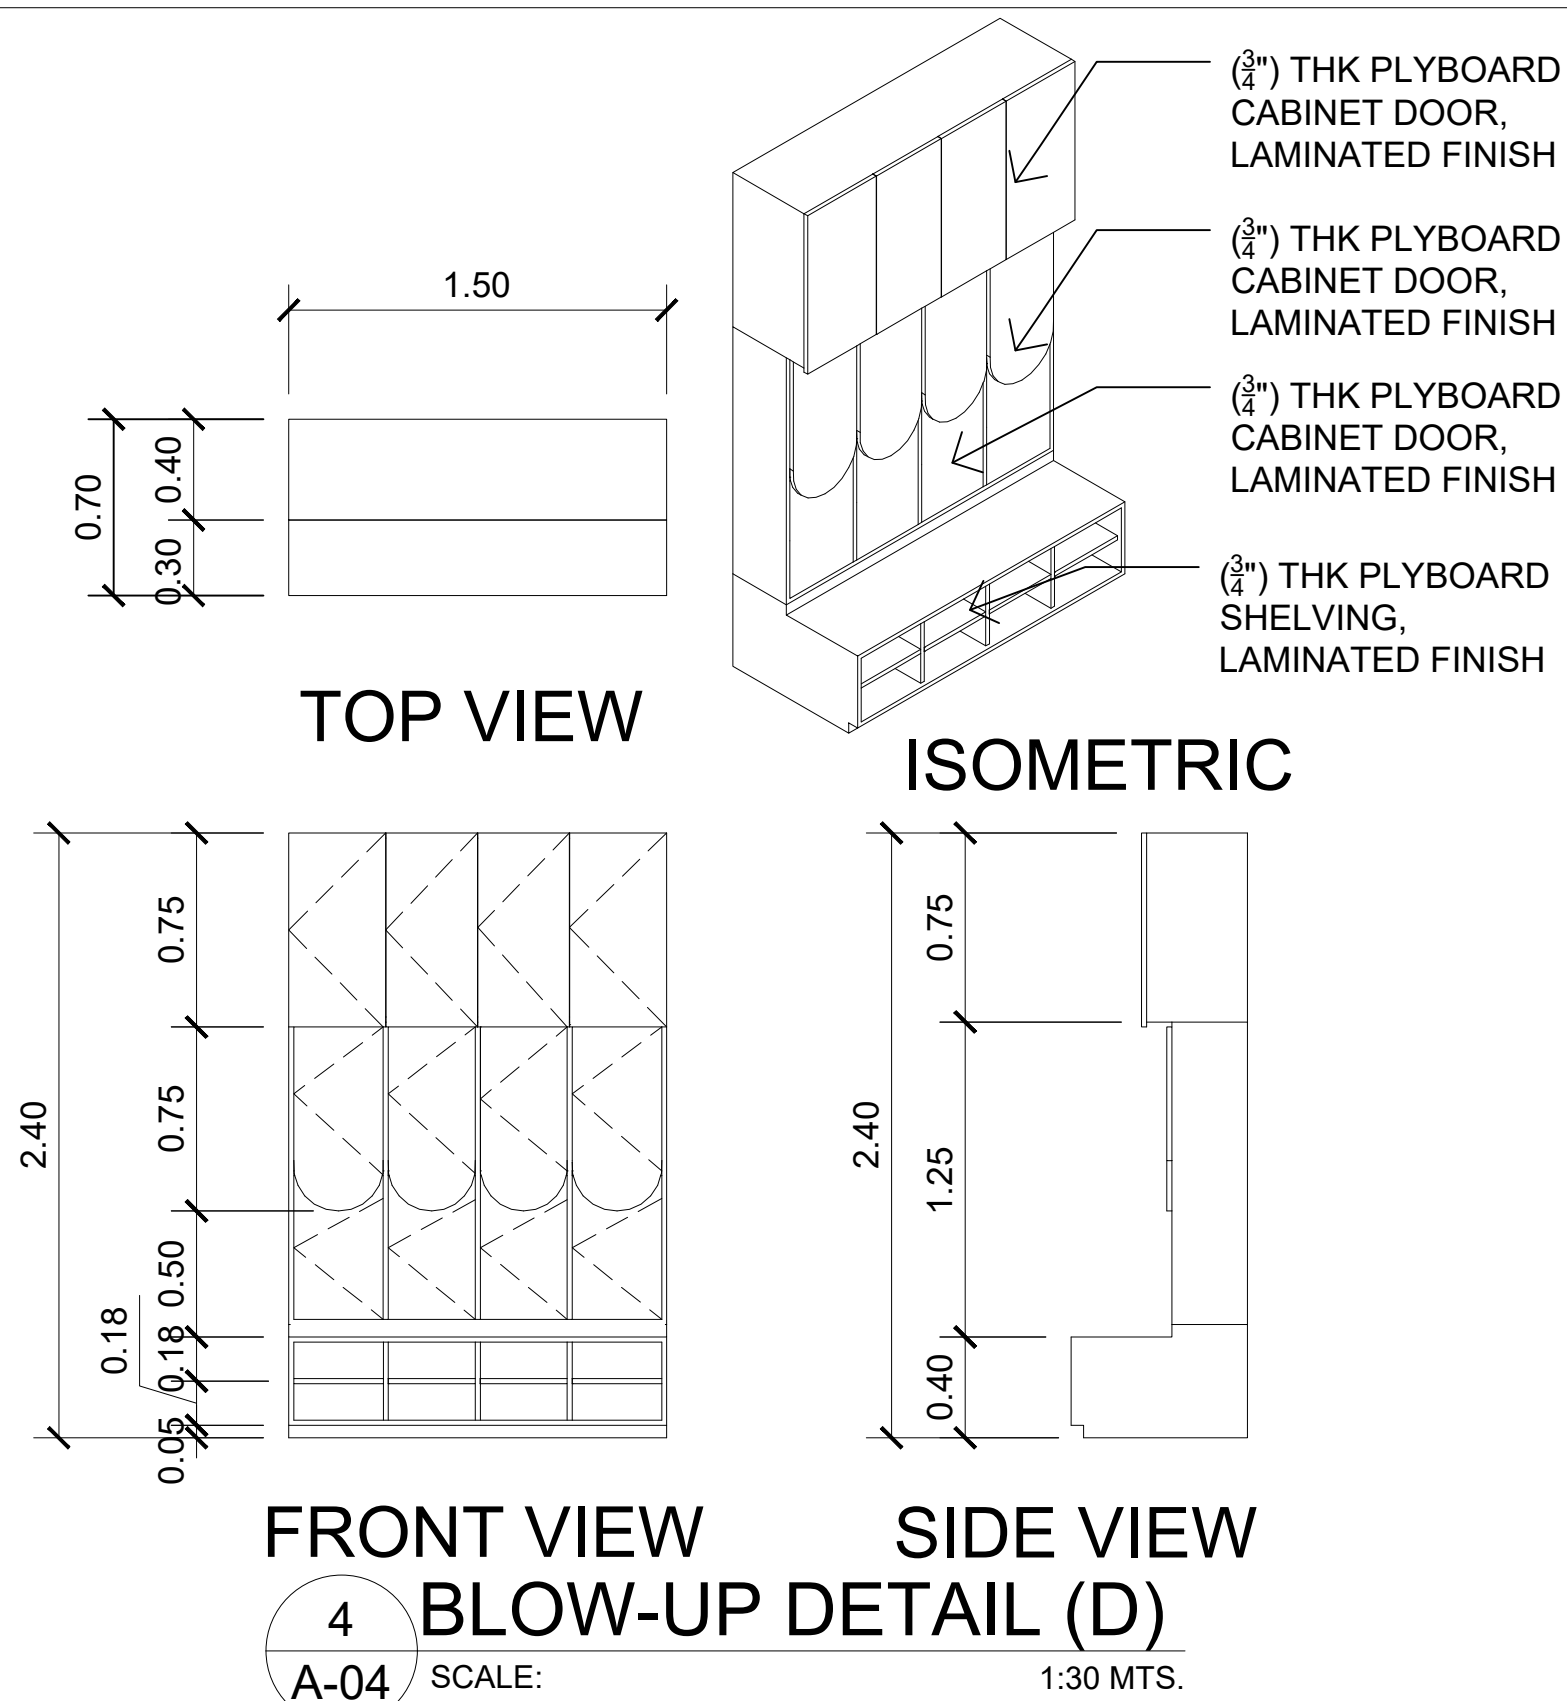

4 BLOW-UP DETAIL (D)
A-04 SCALE: 1:30 MTS.