

LEGEND:

- FF - 01

OUTDOOR STONE TILE
- FF - 02

600 mm. X 600 mm. PORCELAIN TILE
- FF - 03

300 mm. X 300 mm. NON- SKID CERAMIC TILE
- FF - 04

800 mm. X 800 mm. NON- SKID CERAMIC TILE
- FF - 05

WOOD PLANKS
- FF - 06

600 mm. X 600 mm. NON- SKID CERAMIC TILE
- FF - 07


600 mm. X 600 mm. NON- SKID CERAMIC TILE
- FF - 08

VINYL WOOD PLANKS
- FF - 09

VINYL WOOD TILES
- 1

SMOOTH PLASTER FINISH ON 150 mm. (6") THICK CHB
- 2

SMOOTH PLASTER FINISH ON 100 mm. (4") THICK DRY WALL

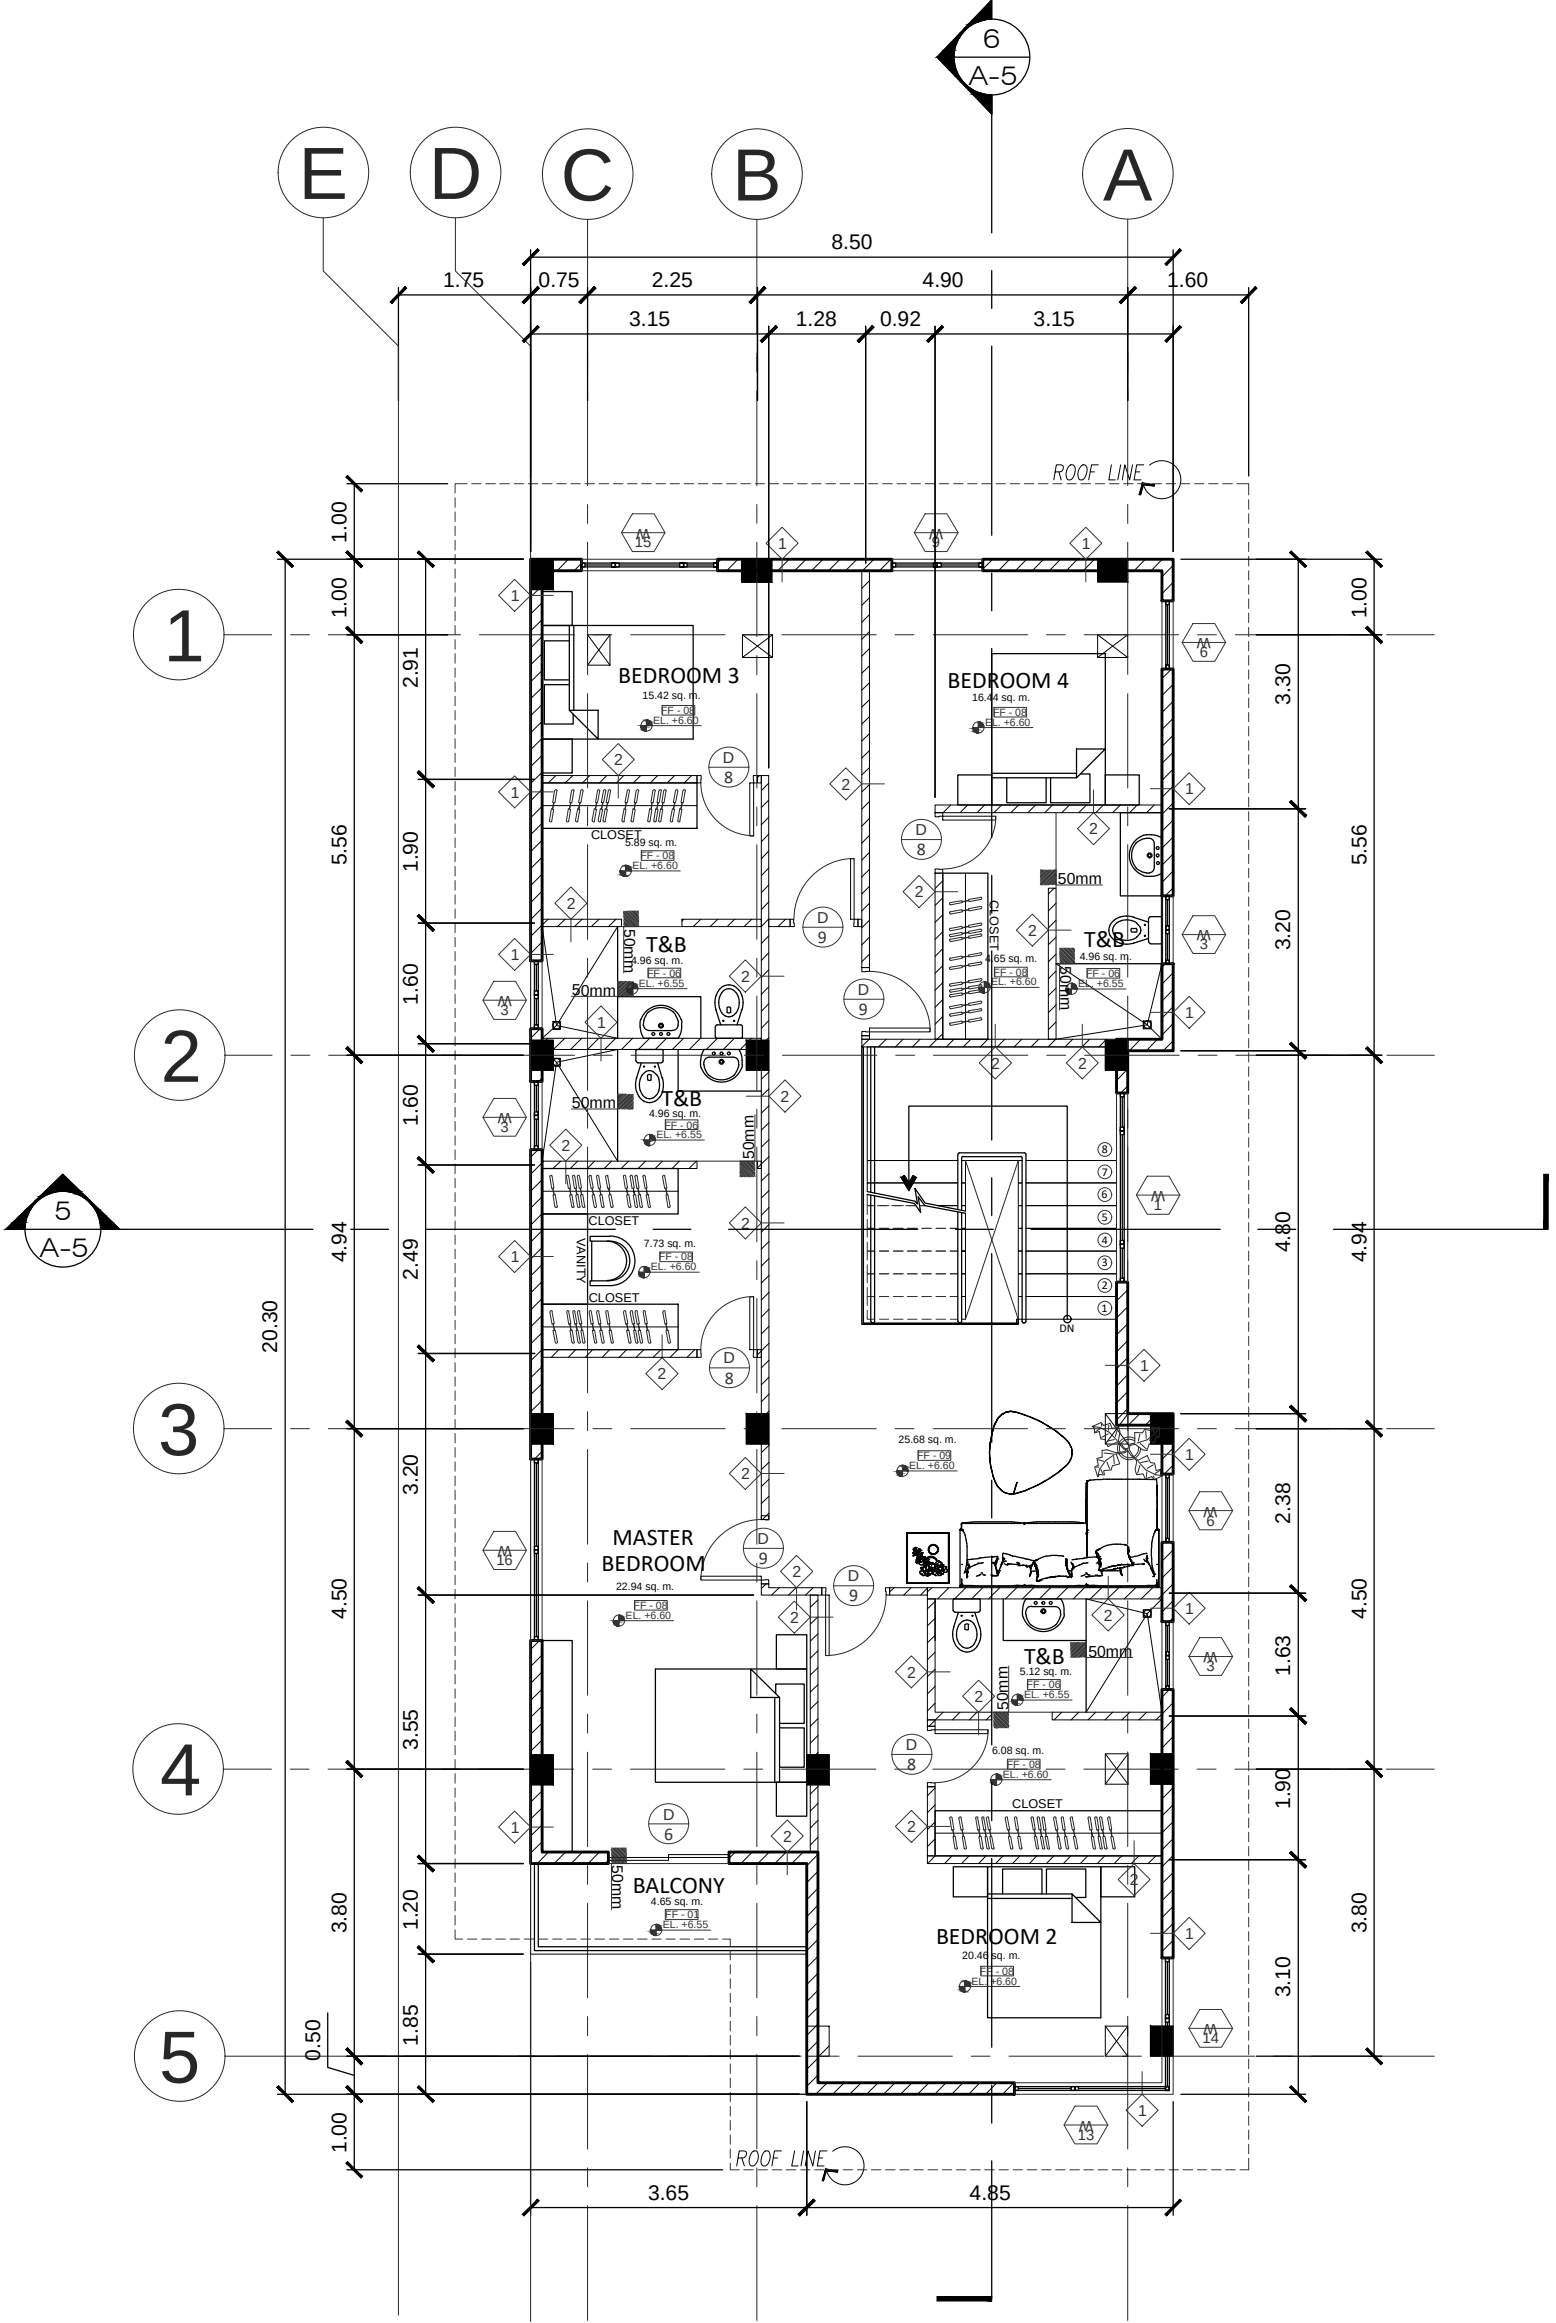

ARANETA RESIDENCE


1

THIRD FLOOR PLAN

A-03

SCALE:

1:100 MTS.

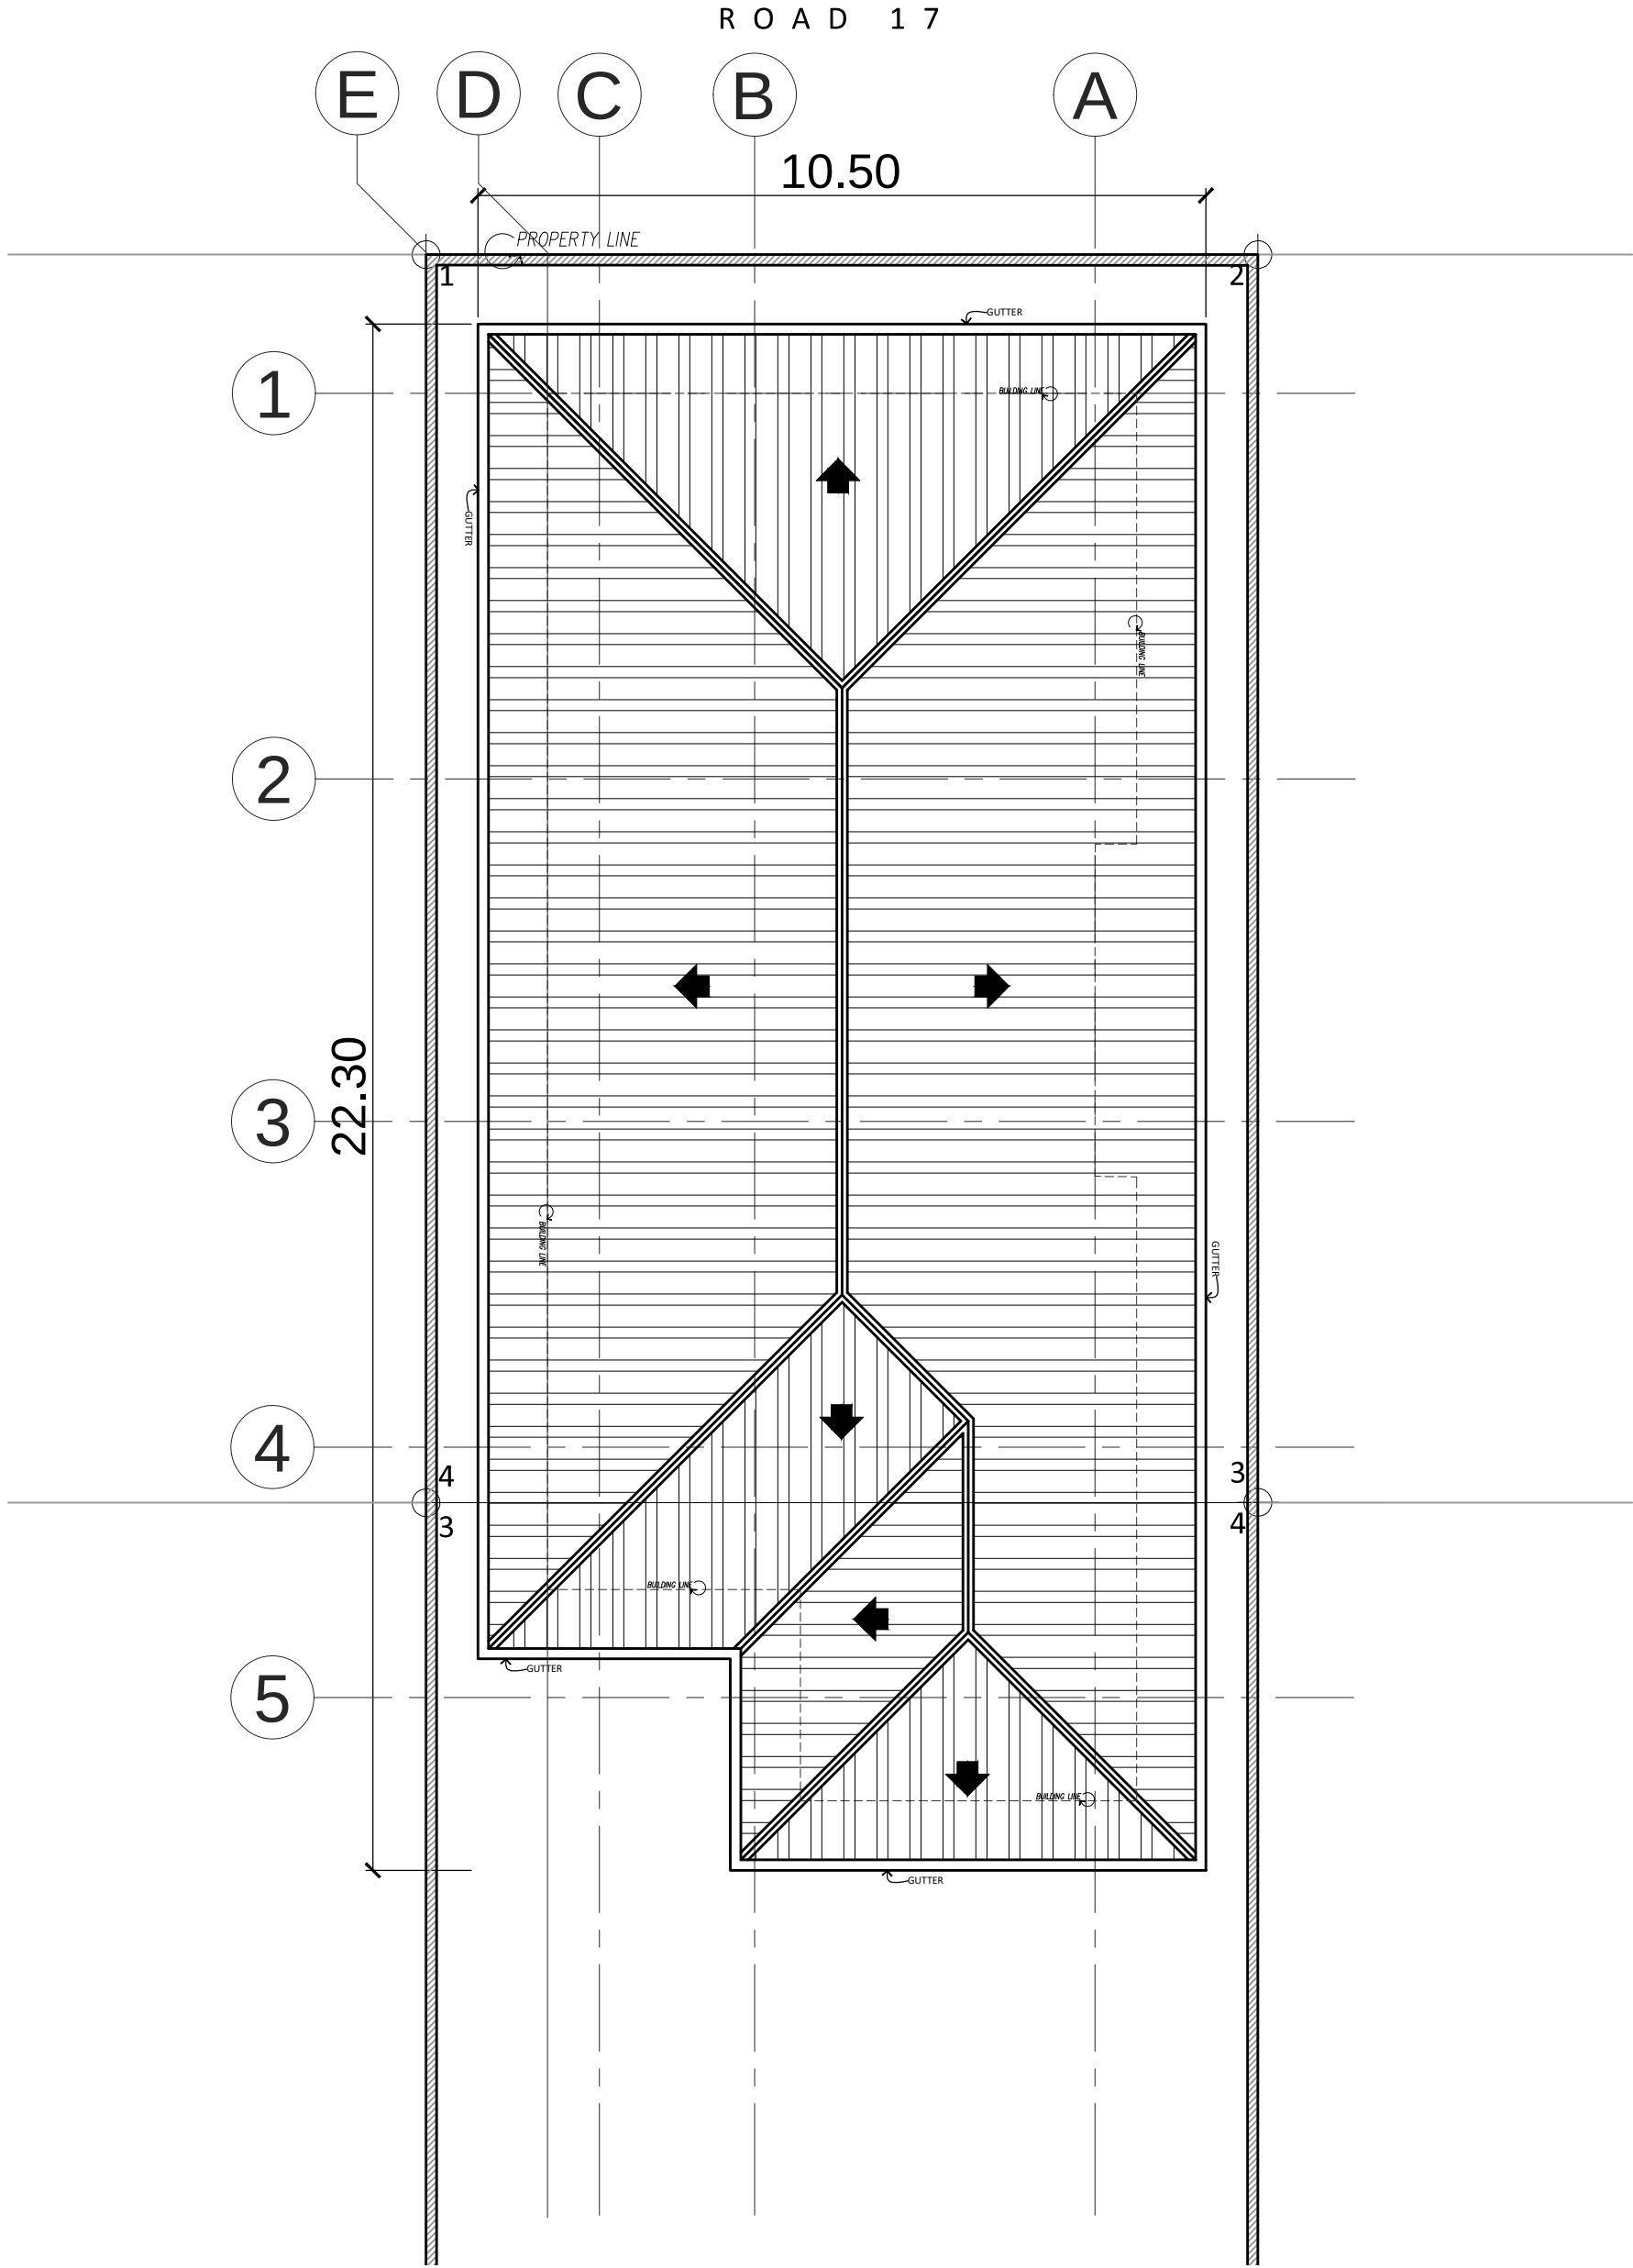

ARANETA RESIDENCE

2

ROOF PLAN

A-03

SCALE:

1:100 MTS.

REPUBLIC OF THE PHILIPPINES DEPARTMENT OF PUBLIC WORKS & HIGHWAYS OFFICE OF THE BUILDING OFFICIAL		
MALABON MUNICIPALITY / CITY		
NO.	REVISIONS	DATE
ALL WORKS SHALL BE CARRIED OUT IN ACCORDANCE WITH ALL BY LAWS AND CODES HAVING JURISDICTION OVER THIS SITE LOCATION. ALL DIMENSIONS AND INFORMATION SHALL BE CHECKED AND VERIFIED ON THE JOB AND ANY VARIANCES TO THE ARCHITECT.		
THESE DRAWINGS MUST NOT BE SCALED. THE DESIGN AND CONTRACT DOCUMENTS ARE THE COPYRIGHT PROPERTY OF THE ARCHITECT AND MAY NOT BE REPRODUCED, ALTERED OR REUSED WITHOUT THE ARCHITECTS WRITTEN AUTHORITY.		
SANITARY		
PRC. NO.	T.J.N.	DATE:
PTF. NO.	PLACE:	
MECHANICAL		
PRC. NO.	T.J.N.	DATE:
PTF. NO.	PLACE:	
ELECTRICAL		
PRC. NO.	T.J.N.	DATE:
PTF. NO.	PLACE:	
STRUCTURAL		
PRC. NO.	T.J.N.	DATE:
PTF. NO.	PLACE:	
ARCHITECT		
REANNE DENISE G. PE		
REANNE DENISE G. PE		
PRC. NO.	T.J.N.	DATE:
PTF. NO.	PLACE:	
OWNER		
MS. CINDY DE LUCIA		
PROJECT:		
PROPOSED ARANETA RESIDENCE LOT 16 AND 17, ARANETA VILLAGE, POTRIERO, MALABON CITY, METRO MANILA.		
SHEET CONTENT:		
FLOOR PLAN		
DESIGN:	SCALE:	SHEET NO.
RD	1:100	A-03
DRAWN:	DATE:	
RD	01/02/22	