

LEGEND:

- 


RECESSED CAN LIGHT
- 


RECESSED CENTER LIGHT
- 

WALL MOUNTED LIGHT
- 

EXHAUST
- 


STRIP LIGHT
- 

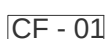PENDANT LIGHT
- 

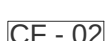
PVC LAMINATE, WOOD FINISH
- 

GYP SUM BOARD, PLAIN PAINT FINISH
- 


PVC LAMINATE, WOOD FINISH

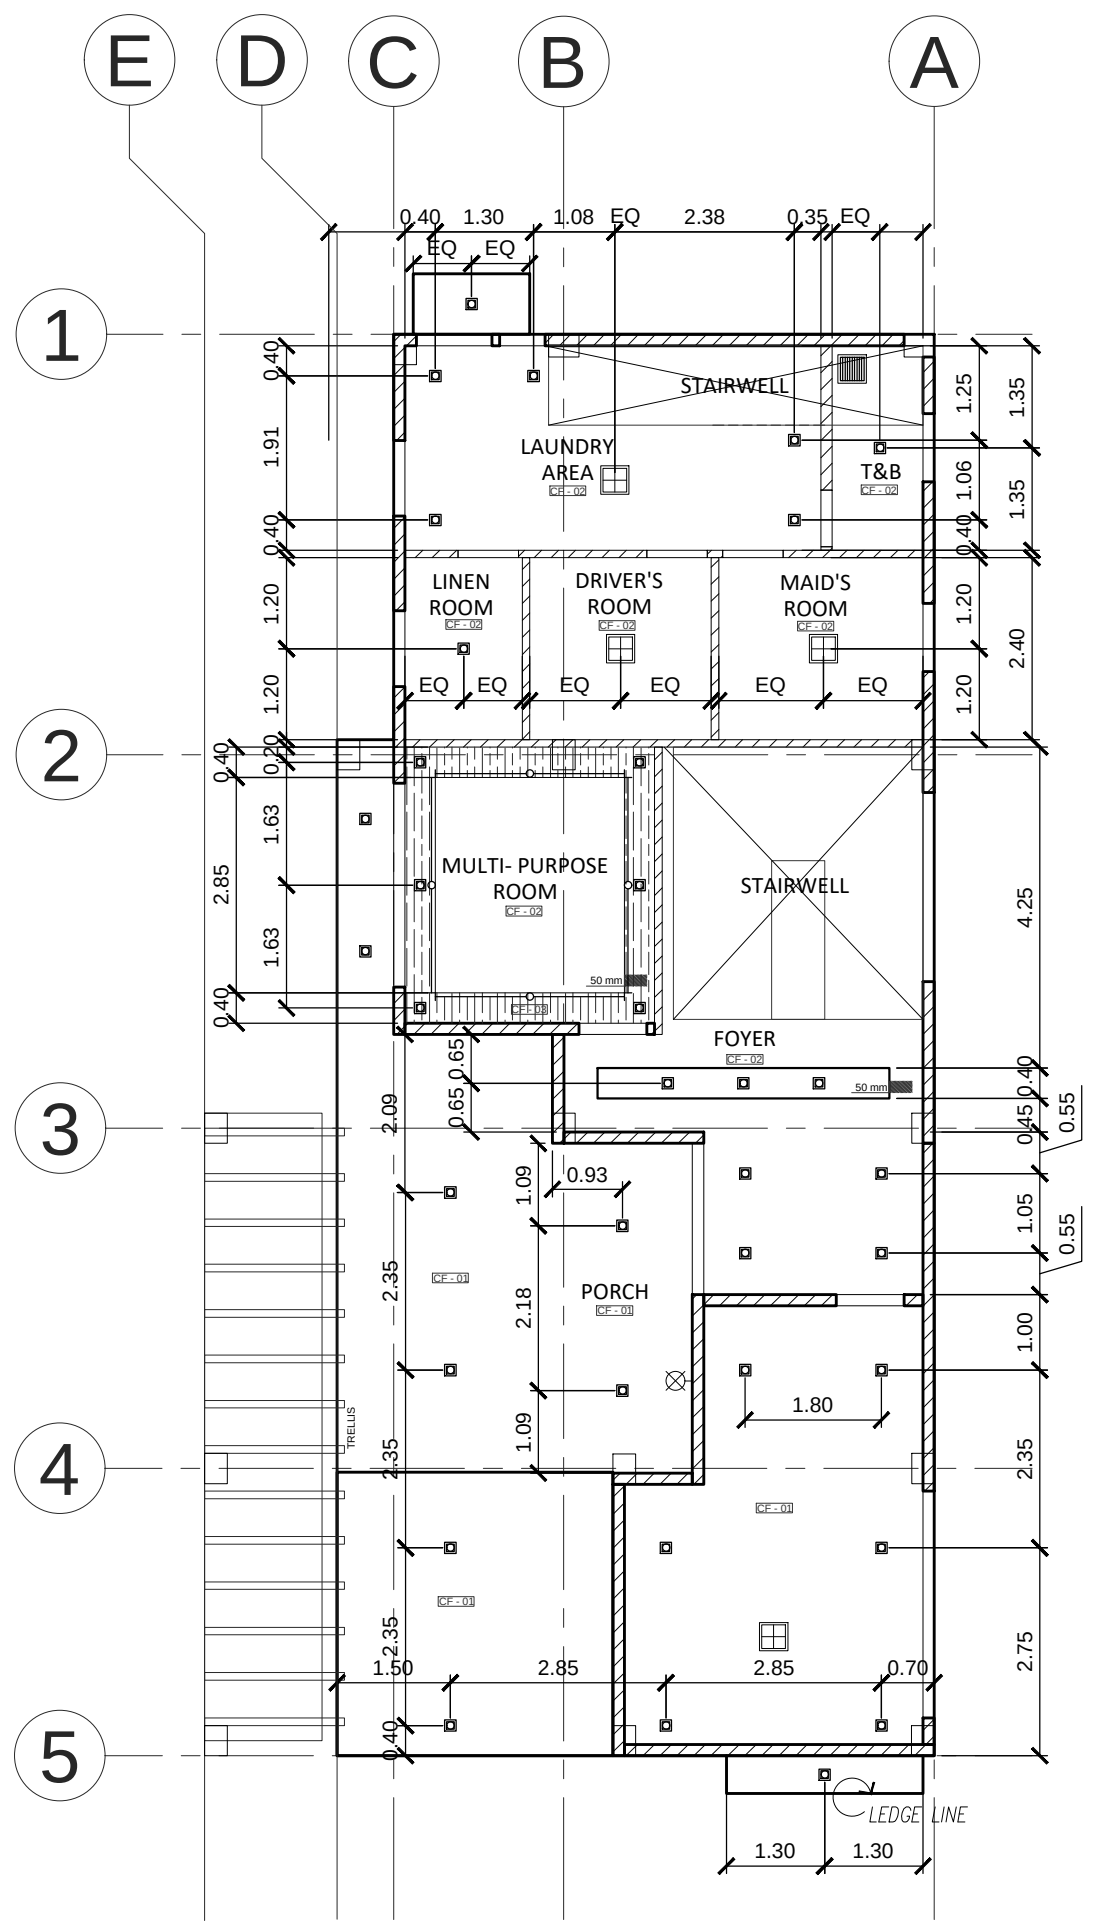

ARANETA RESIDENCE
1 GROUND CEILING PLAN
A-04 SCALE: 1:100 MTS.

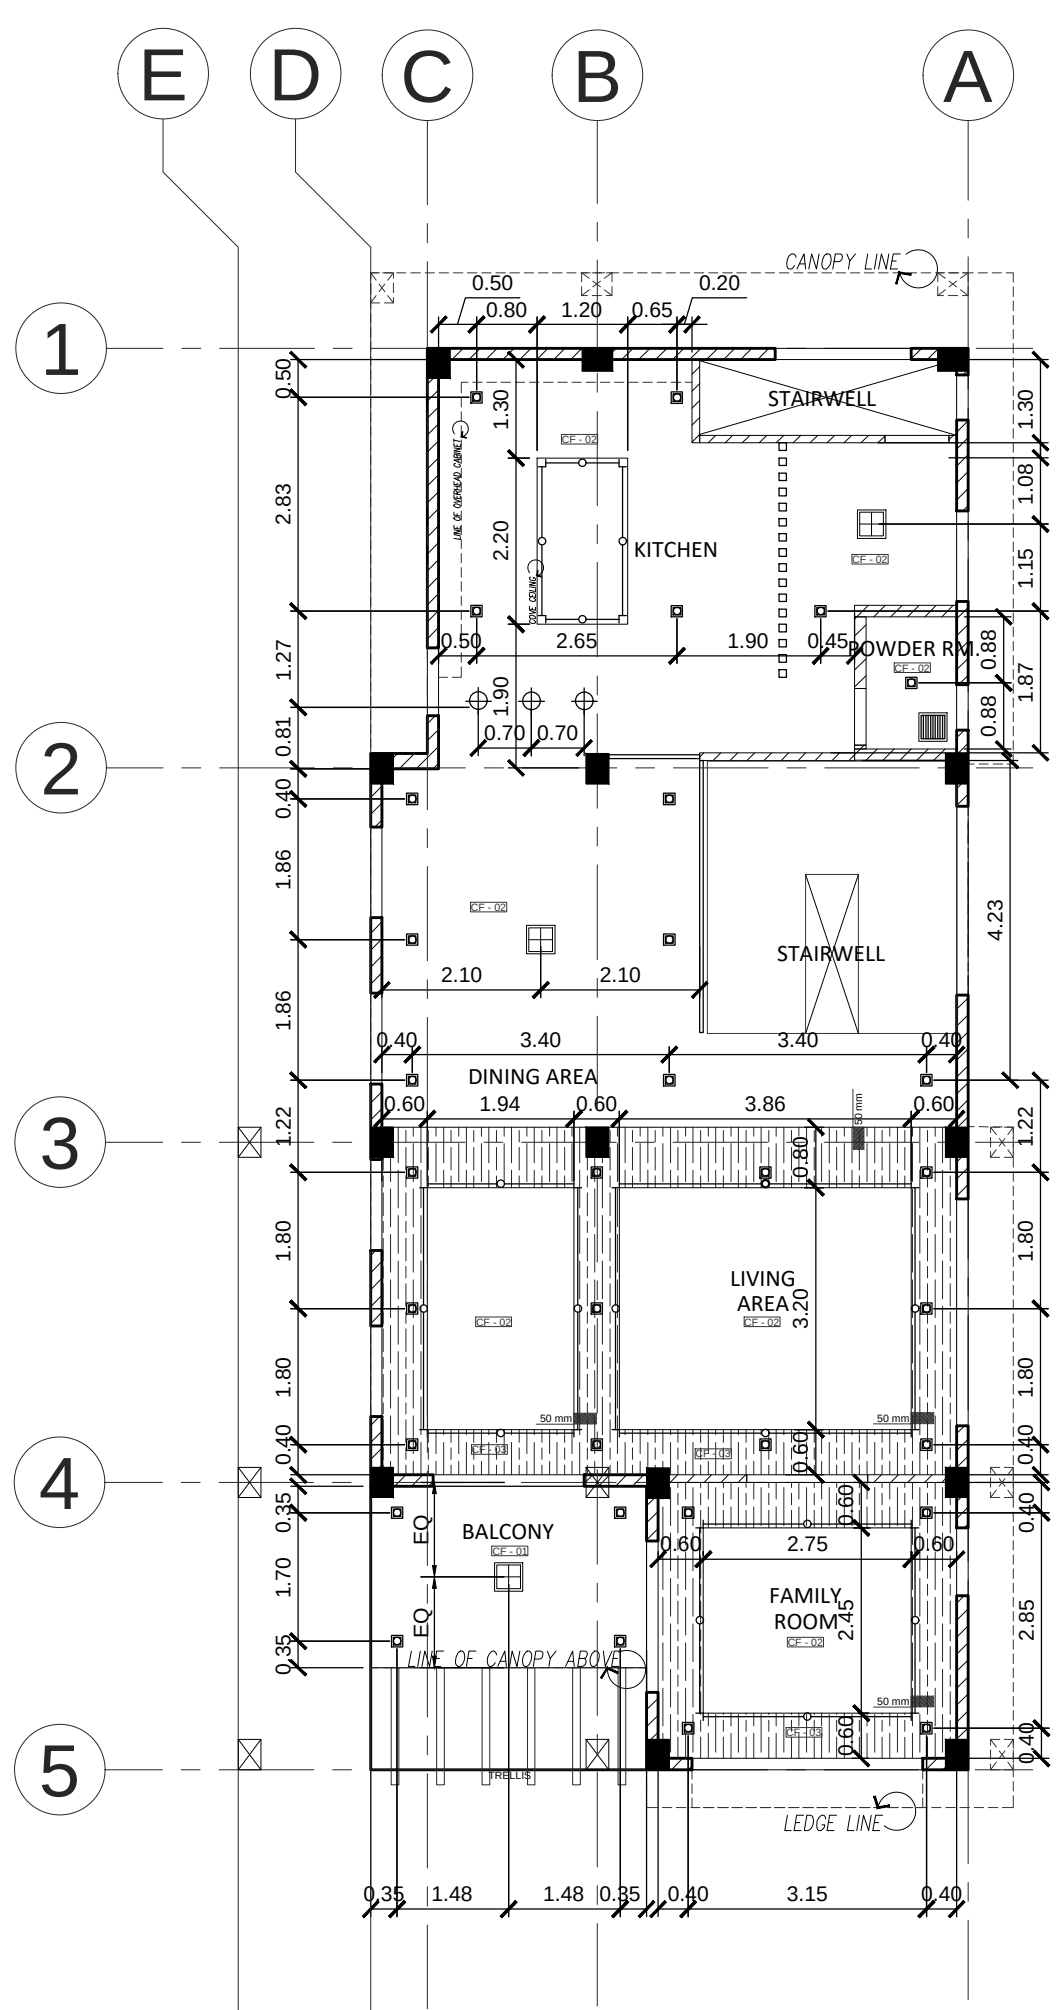

ARANETA RESIDENCE
2 SECOND CEILING PLAN
A-04 SCALE: 1:100 MTS.

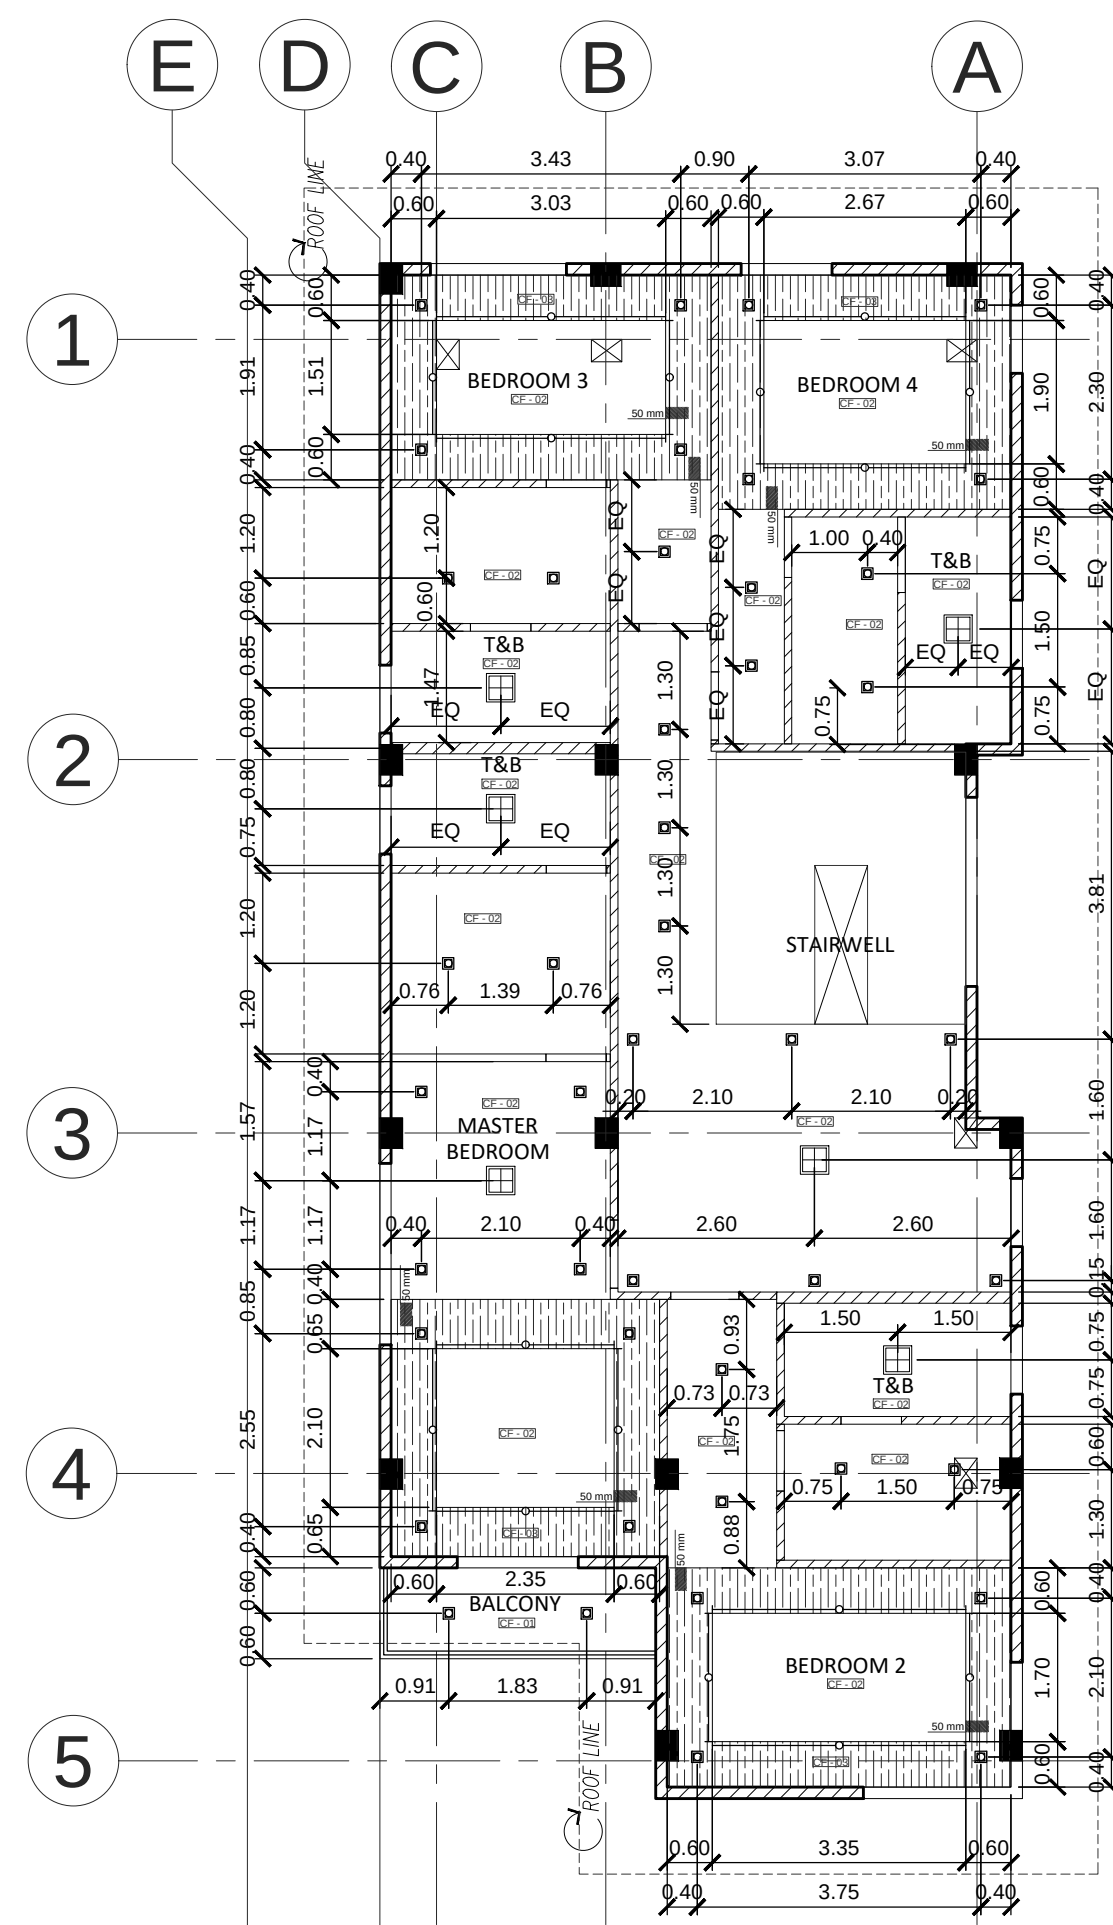

ARANETA RESIDENCE
3 THIRD CEILING PLAN
A-04 SCALE: 1:100 MTS.

REPUBLIC OF THE PHILIPPINES DEPARTMENT OF PUBLIC WORKS & HIGHWAYS OFFICE OF THE BUILDING OFFICIAL		
MALABON MUNICIPALITY / CITY		
NO.	REVISIONS	DATE
ALL WORKS SHALL BE CARRIED OUT IN ACCORDANCE WITH ALL BY LAWS AND CODES HAVING JURISDICTION OVER THIS SITE LOCATION. ALL DIMENSIONS AND INFORMATION SHALL BE CHECKED AND VERIFIED ON THE JOB AND ANY VARIANCES TO THE ARCHITECT.		
THESE DRAWINGS MUST NOT BE SCALED. THE DESIGN AND CONTRACT DOCUMENTS ARE THE COPYRIGHT PROPERTY OF THE ARCHITECT AND MAY NOT BE REPRODUCED, ALTERED OR REUSED WITHOUT THE ARCHITECT'S WRITTEN AUTHORITY.		
SANITARY		
PRC. NO.	T.I.N.	
PTR. NO.	PLACE:	DATE:
MECHANICAL		
PRC. NO.	T.I.N.	
PTR. NO.	PLACE:	DATE:
ELECTRICAL		
PRC. NO.	T.I.N.	
PTR. NO.	PLACE:	DATE:
STRUCTURAL		
PRC. NO.	T.I.N.	
PTR. NO.	PLACE:	DATE:
ARCHITECT		
REANNE DENISE G. PE		
REANNE DENISE G. PE		
PRC. NO.	T.I.N.	
PTR. NO.	PLACE:	DATE:
OWNER		
MS. CINDY DE LUCIA		
PROJECT:		
PROPOSED ARANETA RESIDENCE LOT 16 AND 17, ARANETA VILLAGE, POTRIERO, MALABON CITY, METRO MANILA.		
SHEET CONTENT:		
REFLECTED CEILING PLAN		
DESIGN:	SCALE:	SHEET NO.
RDP	1:100	A-04
DRAWN:	DATE:	
RDP	01/02/22	