


SCHEDULE OF DOORS									
LOCATION	MAIN DOOR, FOYER	MULTI- PURPOSE ROOM	T&B	LINEN RM, DRIVER'S QUARTER, MAID'S QUARTER	SERVICE AREA	FAMILY ROOM	BALCONY	WIC	BEDROOMS, SERVICE STAIR (KITCHEN)
SPECIFICATIONS	WOODEN PANEL DOOR IN VARNISH FINISH	LAMINATED FLUSH DOOR IN WOOD FINISH	LAMINATED FLUSH DOOR IN WOOD FINISH	LAMINATED FLUSH DOOR IN WOOD FINISH	LAMINATED FLUSH DOOR IN WOOD FINISH	GLASS SLIDING DOOR ON ALUMINUM FRAME, POWDER COATED FINISH	GLASS SLIDING DOOR ON ALUMINUM FRAME, POWDER COATED FINISH	LAMINATED FLUSH DOOR IN WOOD FINISH	LAMINATED FLUSH DOOR IN WOOD FINISH
FRAME	2" x 6" K/D WOODEN DOOR JAMB IN VARNISH FINISH	2" x 4" K/D WOODEN DOOR JAMB IN VARNISH FINISH	2" x 4" K/D WOODEN DOOR JAMB IN VARNISH FINISH	2" x 4" K/D WOODEN DOOR JAMB IN VARNISH FINISH	2" x 6" K/D WOODEN DOOR JAMB IN VARNISH FINISH	2" x 6" K/D ALUMINUM DOOR JAMB IN POWDER COATED FINISH	2" x 6" K/D ALUMINUM DOOR JAMB IN POWDER COATED FINISH	2" x 4" K/D WOODEN DOOR JAMB IN VARNISH FINISH	2" x 4" K/D WOODEN DOOR JAMB IN VARNISH FINISH
QUANTITY	1 SET	1 SET	2 SETS	3 SETS	1 SET	1 SET	2 SETS	4 SETS	5 SETS

ARANETA RESIDENCE
1 SCHEDULE OF DOORS
A-05 SCALE: 1:75 MTS


SCHEDULE OF WINDOWS								
LOCATION	STAIRS	MAID'S QUARTER	T&B	LAUNDRY AREA, SERVICE STAIRS	LAUNDRY AREA, LINEN ROOM	MULTI- PURPOSE RM., FAMILY RM., CLEAN KITCHEN, 3F LIVING RM., BEDROOM 4	2F LIVING AREA	POWDER ROOM
SPECIFICATIONS	6mm THK TEMPERED GLASS FIXED WINDOW PANELS	6mm THK TEMPERED GLASS SLIDING WINDOW PANELS	6mm THK TEMPERED GLASS AWNING WINDOW PANELS	6mm THK TEMPERED GLASS CASEMENT WINDOW PANELS	6mm THK TEMPERED GLASS SLIDING WINDOW PANELS	6mm THK TEMPERED GLASS AWNING WINDOW PANELS W/ FIXED WINDOW PANELS	6mm THK TEMPERED GLASS AWNING WINDOW PANELS W/ FIXED WINDOW PANELS	6mm THK TEMPERED GLASS AWNING WINDOW PANELS
FRAME	PAINTED B.I. FRAME (VERIFY COLOR)	PAINTED B.I. FRAME (VERIFY COLOR)	PAINTED B.I. FRAME (VERIFY COLOR)	PAINTED B.I. FRAME (VERIFY COLOR)	PAINTED B.I. FRAME (VERIFY COLOR)	PAINTED B.I. FRAME (VERIFY COLOR)	PAINTED B.I. FRAME (VERIFY COLOR)	PAINTED B.I. FRAME (VERIFY COLOR)
QUANTITY	3 SETS	1 SET	5 SETS	2 SETS	2 SETS	6 SETS	1 SET	1 SET

LOCATION	DIRTY KITCHEN	2F SERVICE STAIRS	DINING AREA, BEDROOM 4	FAMILY ROOM	BEDROOM 2	BEDROOM 2	BEDROOM 3	MASTER BEDROOM	GYM
SPECIFICATIONS	6mm THK TEMPERED GLASS SLIDING WINDOW PANELS	6mm THK TEMPERED GLASS AWNING WINDOW PANELS	6mm THK TEMPERED GLASS AWNING WINDOW PANELS W/ FIXED WINDOW PANELS	6mm THK TEMPERED GLASS FIXED WINDOW PANELS W/ AWNING WINDOW PANELS	6mm THK TEMPERED GLASS FIXED WINDOW PANELS W/ AWNING WINDOW PANELS	6mm THK TEMPERED GLASS FIXED WINDOW PANELS W/ AWNING WINDOW PANELS	6mm THK TEMPERED GLASS FIXED WINDOW PANELS W/ AWNING WINDOW PANELS	6mm THK TEMPERED GLASS FIXED WINDOW PANELS W/ AWNING WINDOW PANELS	6mm THK TEMPERED GLASS SLIDING WINDOW PANELS
FRAME	PAINTED B.I. FRAME (VERIFY COLOR)	PAINTED B.I. FRAME (VERIFY COLOR)	PAINTED B.I. FRAME (VERIFY COLOR)	PAINTED B.I. FRAME (VERIFY COLOR)	PAINTED B.I. FRAME (VERIFY COLOR)	PAINTED B.I. FRAME (VERIFY COLOR)	PAINTED B.I. FRAME (VERIFY COLOR)	PAINTED B.I. FRAME (VERIFY COLOR)	PAINTED B.I. FRAME (VERIFY COLOR)
QUANTITY	1 SET	1 SET	5 SETS	1 SET	1 SET	1 SET	1 SET	1 SET	1 SET


ARANETA RESIDENCE
2 SCHEDULE OF WINDOWS
A-05 SCALE: 1:75 MTS

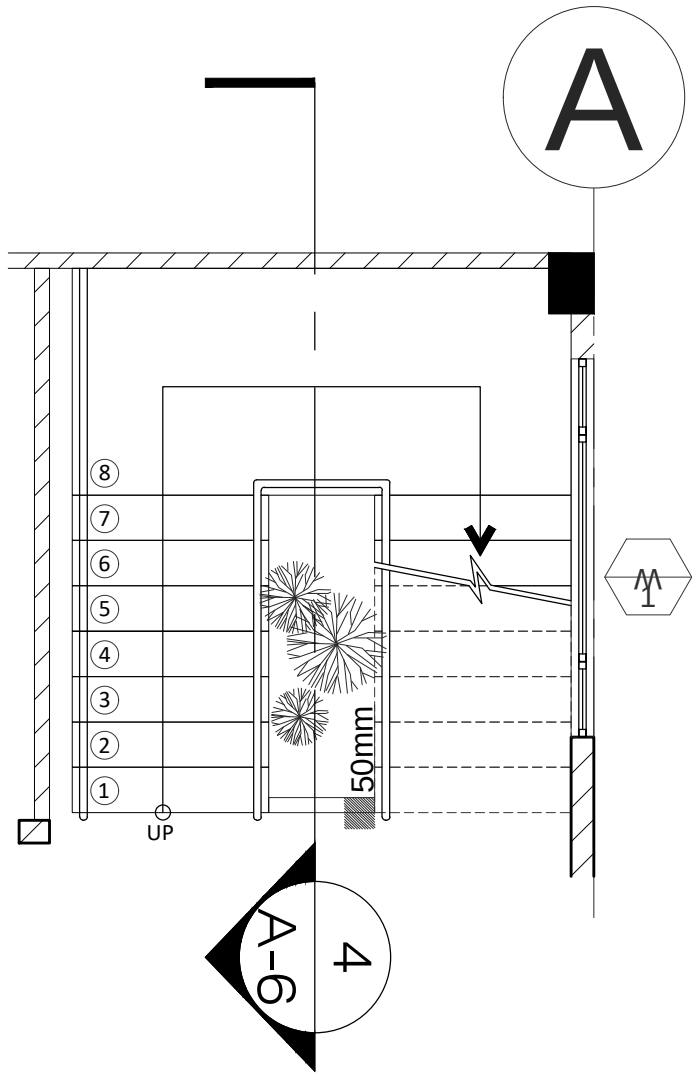

ARANETA RESIDENCE
3 STAIR DETAIL PLAN
A-05 SCALE: 1:50 MTS.

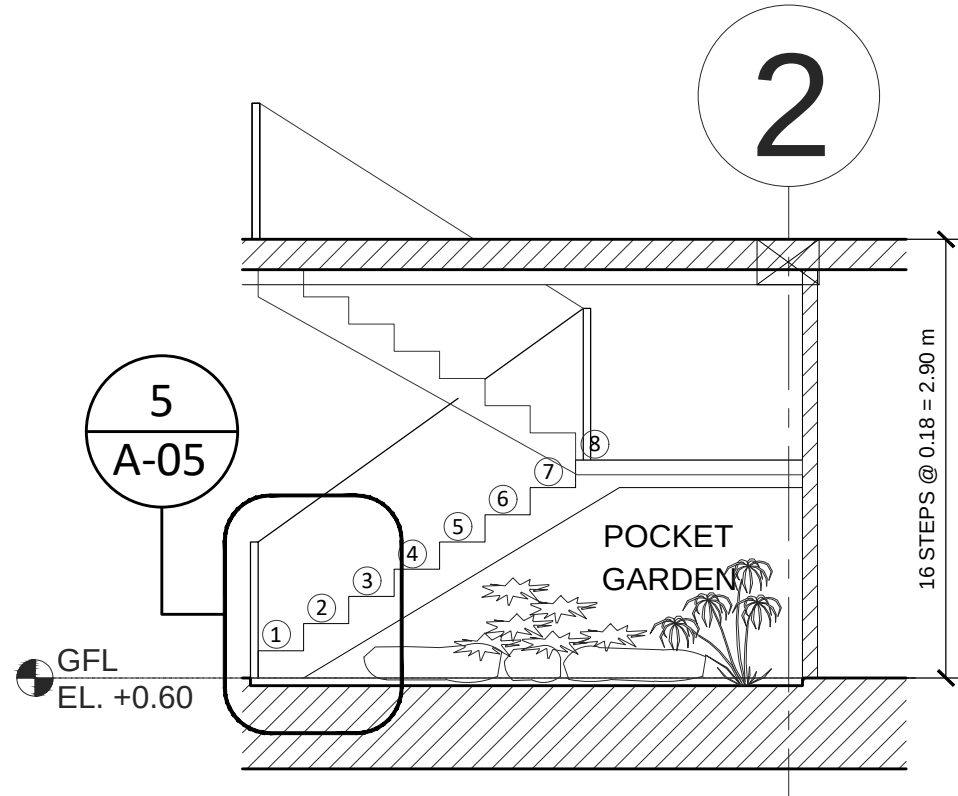

ARANETA RESIDENCE
4 STAIR DETAIL SECTION A
A-05 SCALE: 1:50 MTS.

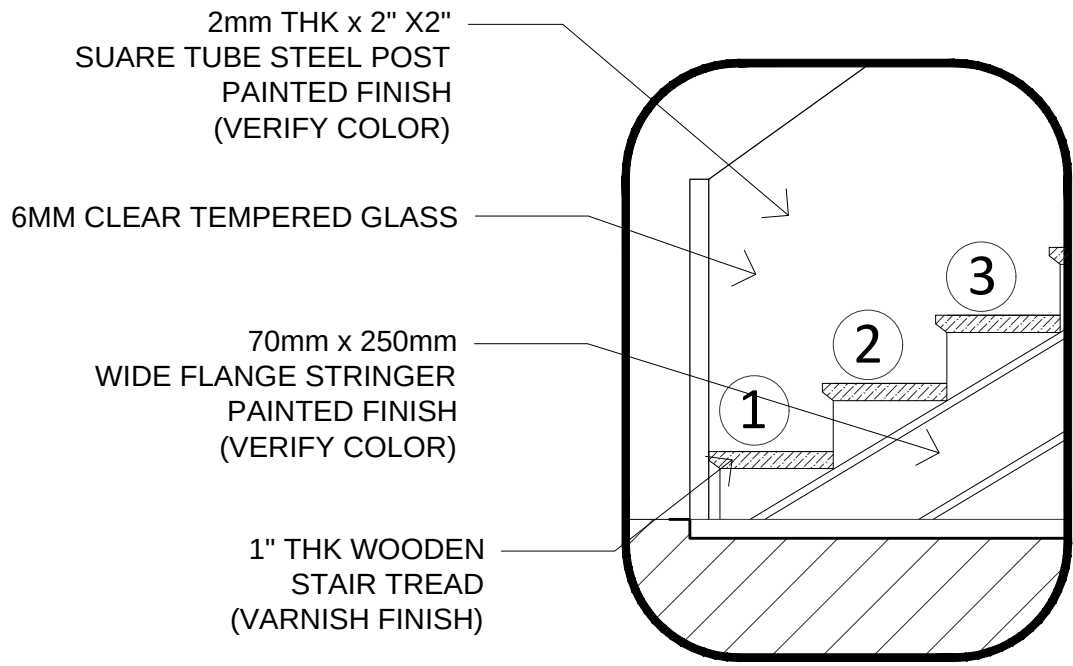

ARANETA RESIDENCE
5 STAIR DETAIL SECTION B
A-05 SCALE: 1:20 MTS.

REPUBLIC OF THE PHILIPPINES DEPARTMENT OF PUBLIC WORKS & HIGHWAYS OFFICE OF THE BUILDING OFFICIAL		
MALABON MUNICIPALITY / CITY		
NO.	REVISIONS	DATE
ALL WORKS SHALL BE CARRIED OUT IN ACCORDANCE WITH ALL BY LAWS AND CODES HAVING JURISDICTION OVER THIS SITE LOCATION. ALL DIMENSIONS AND INFORMATION SHALL BE CHECKED AND VERIFIED ON THE JOB AND ANY VARIANCES TO THE ARCHITECT.		
THESE DRAWINGS MUST NOT BE SCALED. THE DESIGN AND CONTRACT DOCUMENTS ARE THE COPYRIGHT PROPERTY OF THE ARCHITECT AND MAY NOT BE REPRODUCED, ALTERED OR REUSED WITHOUT THE ARCHITECTS WRITTEN AUTHORITY.		
SANITARY		
PRC. NO.	T.J.N.	DATE
PTF. NO.	PLACE:	DATE:
MECHANICAL		
PRC. NO.	T.J.N.	DATE
PTF. NO.	PLACE:	DATE:
ELECTRICAL		
PRC. NO.	T.J.N.	DATE
PTF. NO.	PLACE:	DATE:
STRUCTURAL		
PRC. NO.	T.J.N.	DATE
PTF. NO.	PLACE:	DATE:
ARCHITECT		
REANNE DENISE G. PE		
REANNE DENISE G. PE		
PRC. NO.	T.J.N.	DATE
PTF. NO.	PLACE:	DATE:
OWNER		
MS. CINDY DE LUCIA		
PROJECT:		
PROPOSED ARANETA RESIDENCE LOT 16 AND 17, ARANETA VILLAGE, POTRIERO, MALABON CITY, METRO MANILA.		
SHEET CONTENT:		
ROOF PLAN DOORS AND WINDOW SCHEDULE DETAILS		
DESIGN:	SCALE:	SHEET NO.
ROP	1:100	A-05
DRAWN:	DATE:	
ROP	01/02/22	