

ALL WORKS SHALL BE CARRIED OUT IN ACCORDANCE WITH ALL BY LAWS AND CODES HAVING JURISDICTION OVER THIS SITE LOCATION. ALL DIMENSIONS AND INFORMATION SHALL BE CHECKED AND VERIFIED ON THE JOB AND ANY VARIANCES TO THE ARCHITECT.

THESE DRAWINGS MUST NOT BE SCALED. THE DESIGN AND CONTRACT DOCUMENTS ARE THE COPYRIGHT PROPERTY OF THE ARCHITECT AND MAY NOT BE REPRODUCED, ALTERED OR REUSED WITHOUT THE ARCHITECTS WRITTEN AUTHORITY.

SANITARY

PRC. NO. T.J.N. DATE:
PTR. NO. PLACE:

MECHANICAL

PRC. NO. T.J.N. DATE:
PTR. NO. PLACE:

ELECTRICAL

PRC. NO. T.J.N. DATE:
PTR. NO. PLACE:

STRUCTURAL

PRC. NO. T.J.N. DATE:
PTR. NO. PLACE:

ARCHITECT

REANNE DENISE G. PE

REANNE DENISE G. PE

PRC. NO. 45779 T.J.N. 339-409-845
PTR. NO. 0762864 PLACE: QUEZON CITY DATE: 02/05/21

OWNER

MS. CINDY DE LUCIA


PROJECT:

PROPOSED
ARANETA RESIDENCE
LOT 16 AND 17, ARANETA VILLAGE,
POTRIERO, MALABON CITY, METRO MANILA.


SHEET CONTENT:

SECTION
ELEVATION


DESIGN: RDP SCALE: 1:100 SHEET NO:
DRAWN: RDP DATE: 01/02/22 A-06

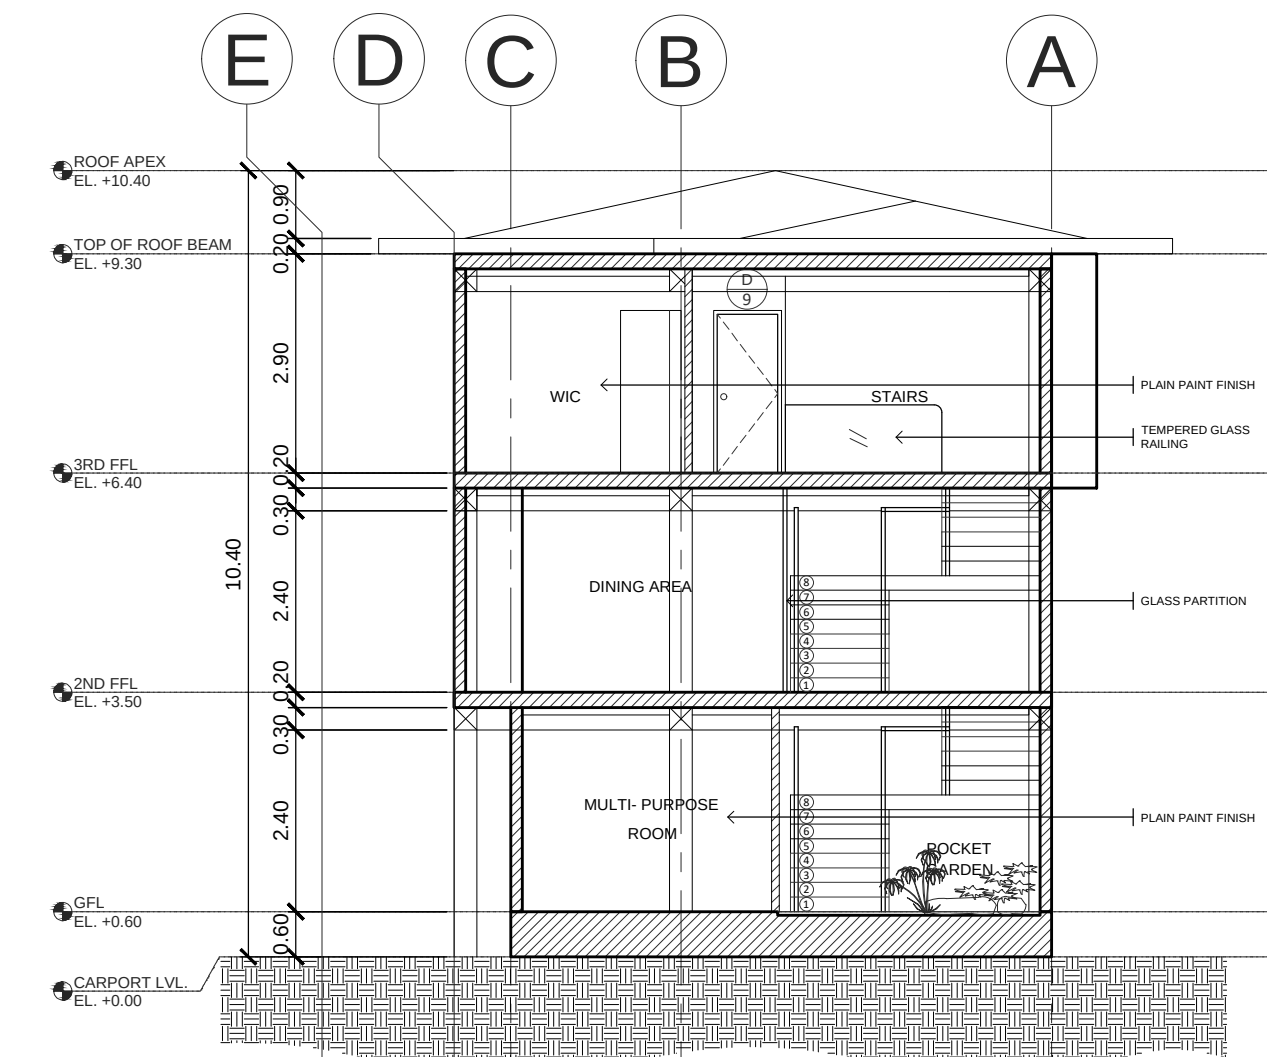


ARANETA RESIDENCE
1 CROSS SECTION
A-06 SCALE: 1:100 MTS

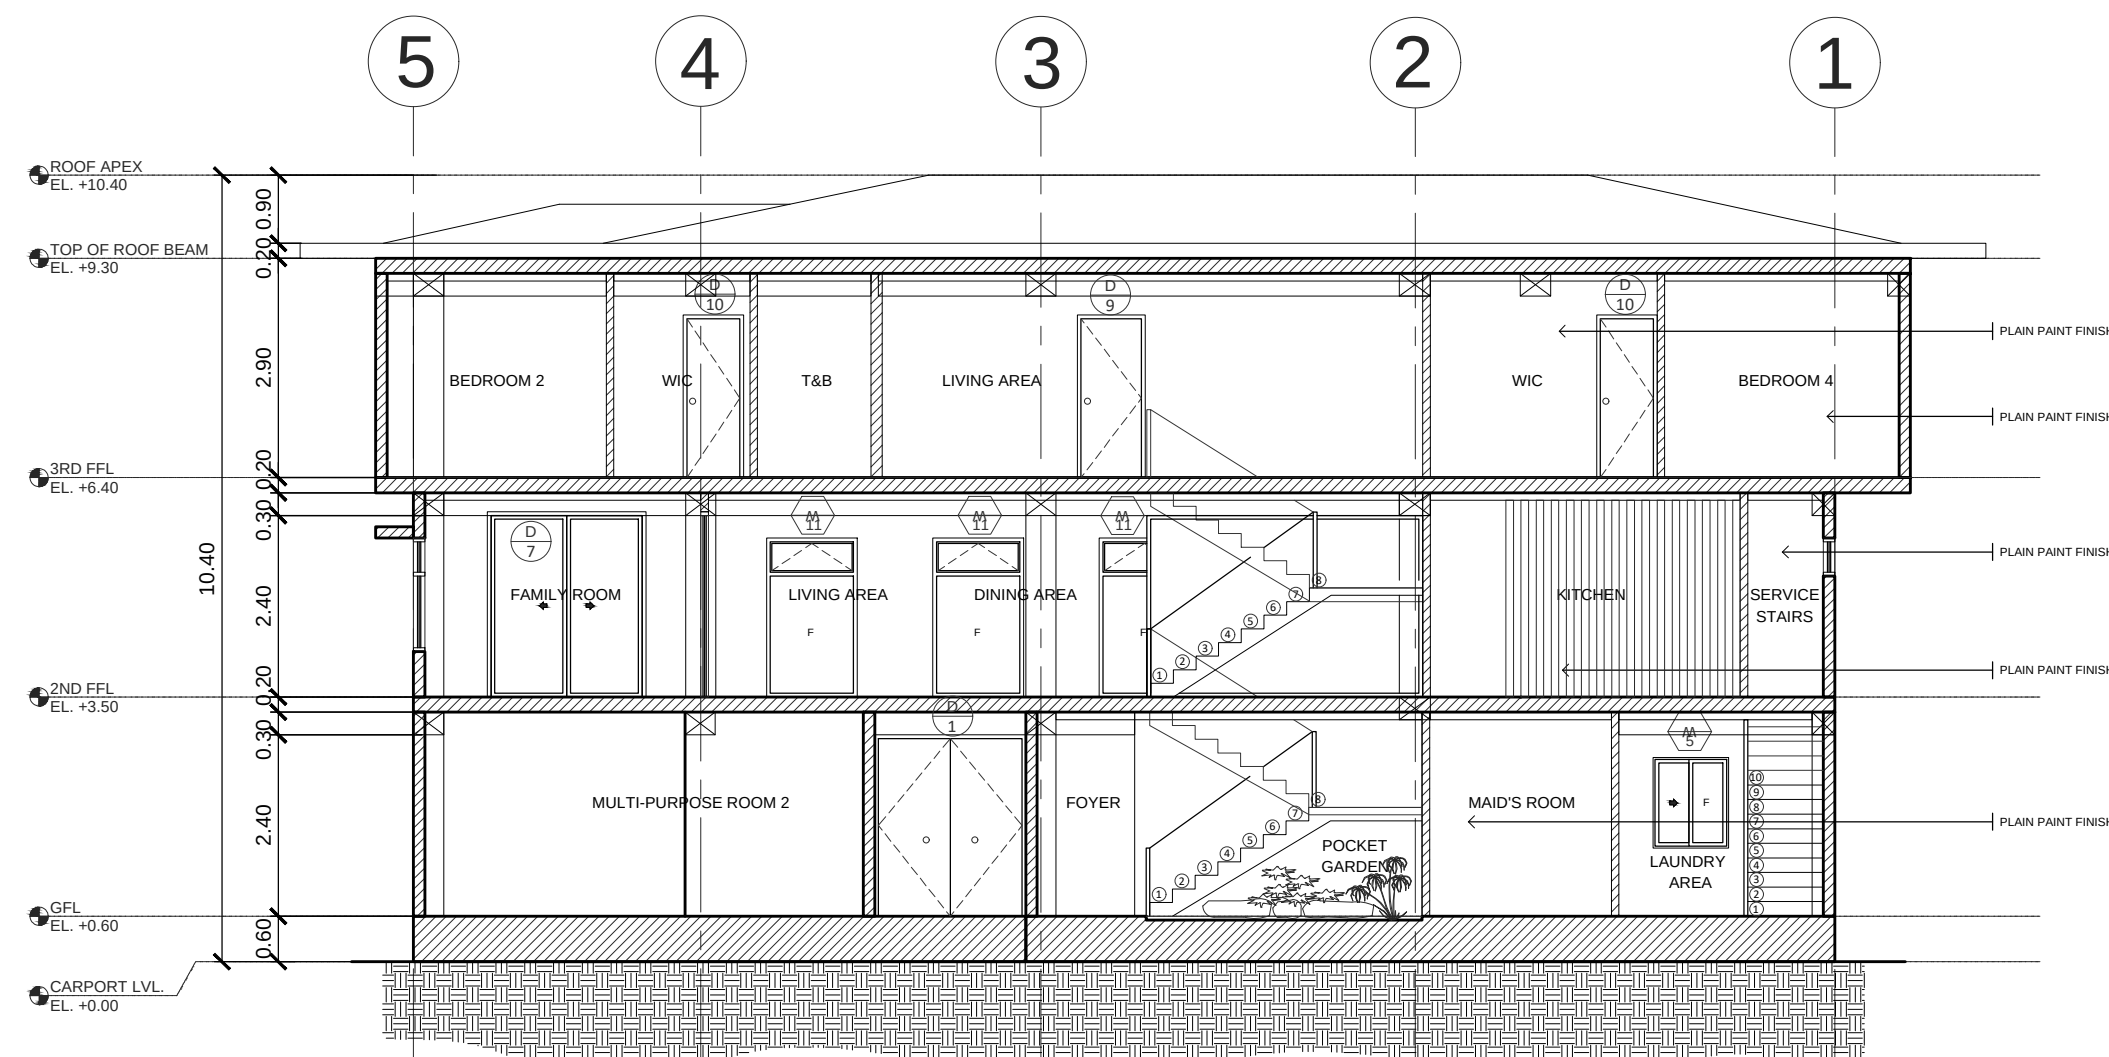


ARANETA RESIDENCE
2 LONGITUDINAL SECTION
A-06 SCALE: 1:100 MTS

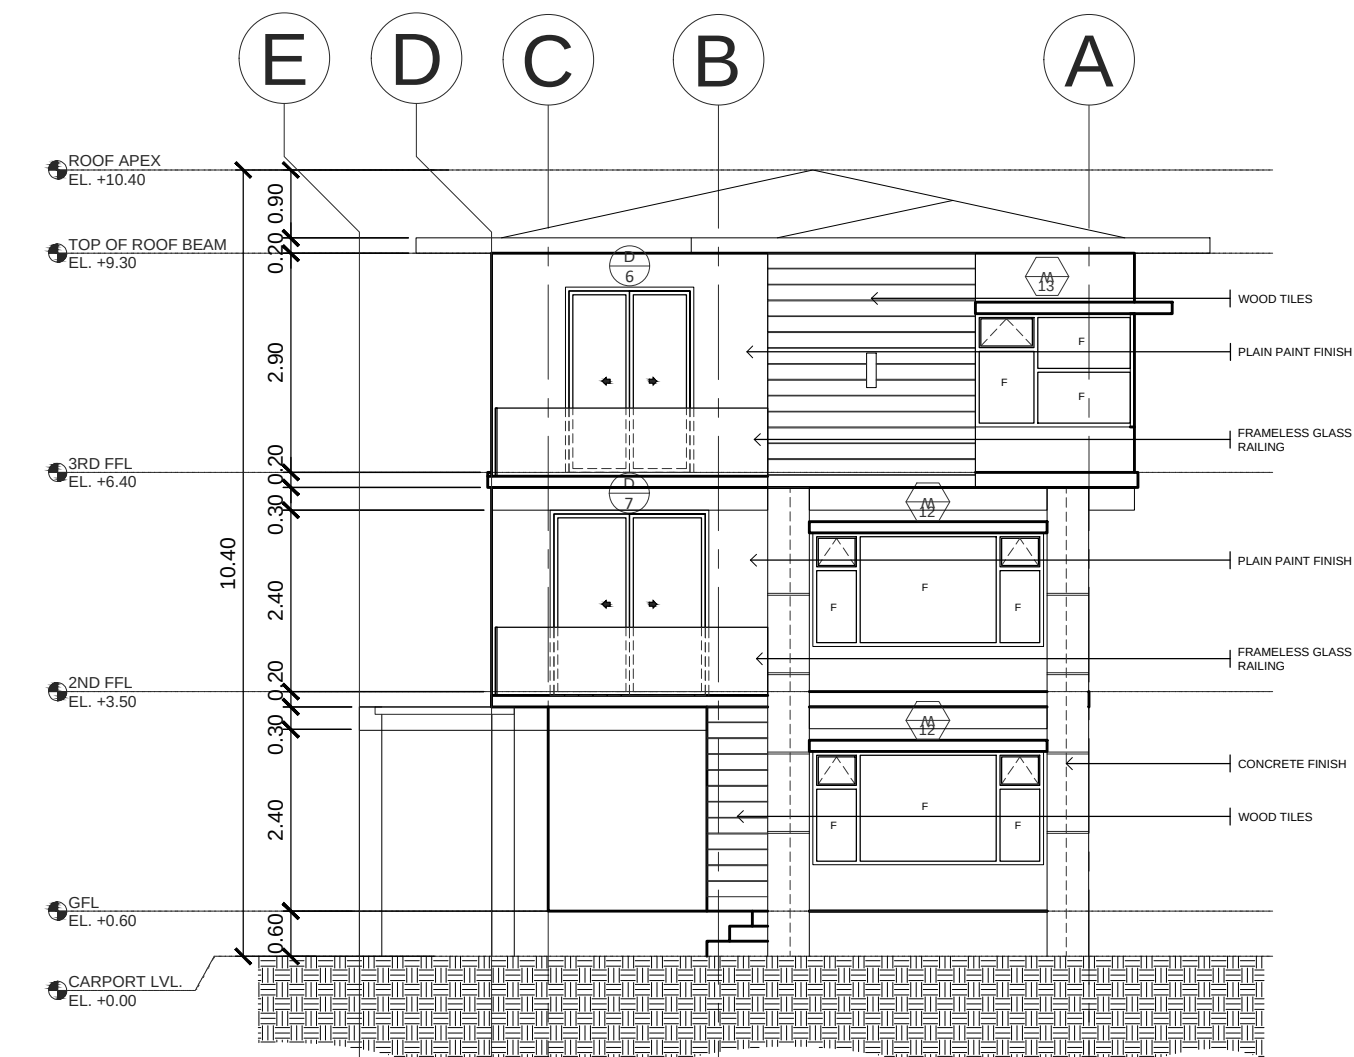


ARANETA RESIDENCE
3 FRONT ELEVATION
A-06 SCALE: 1:100 MTS

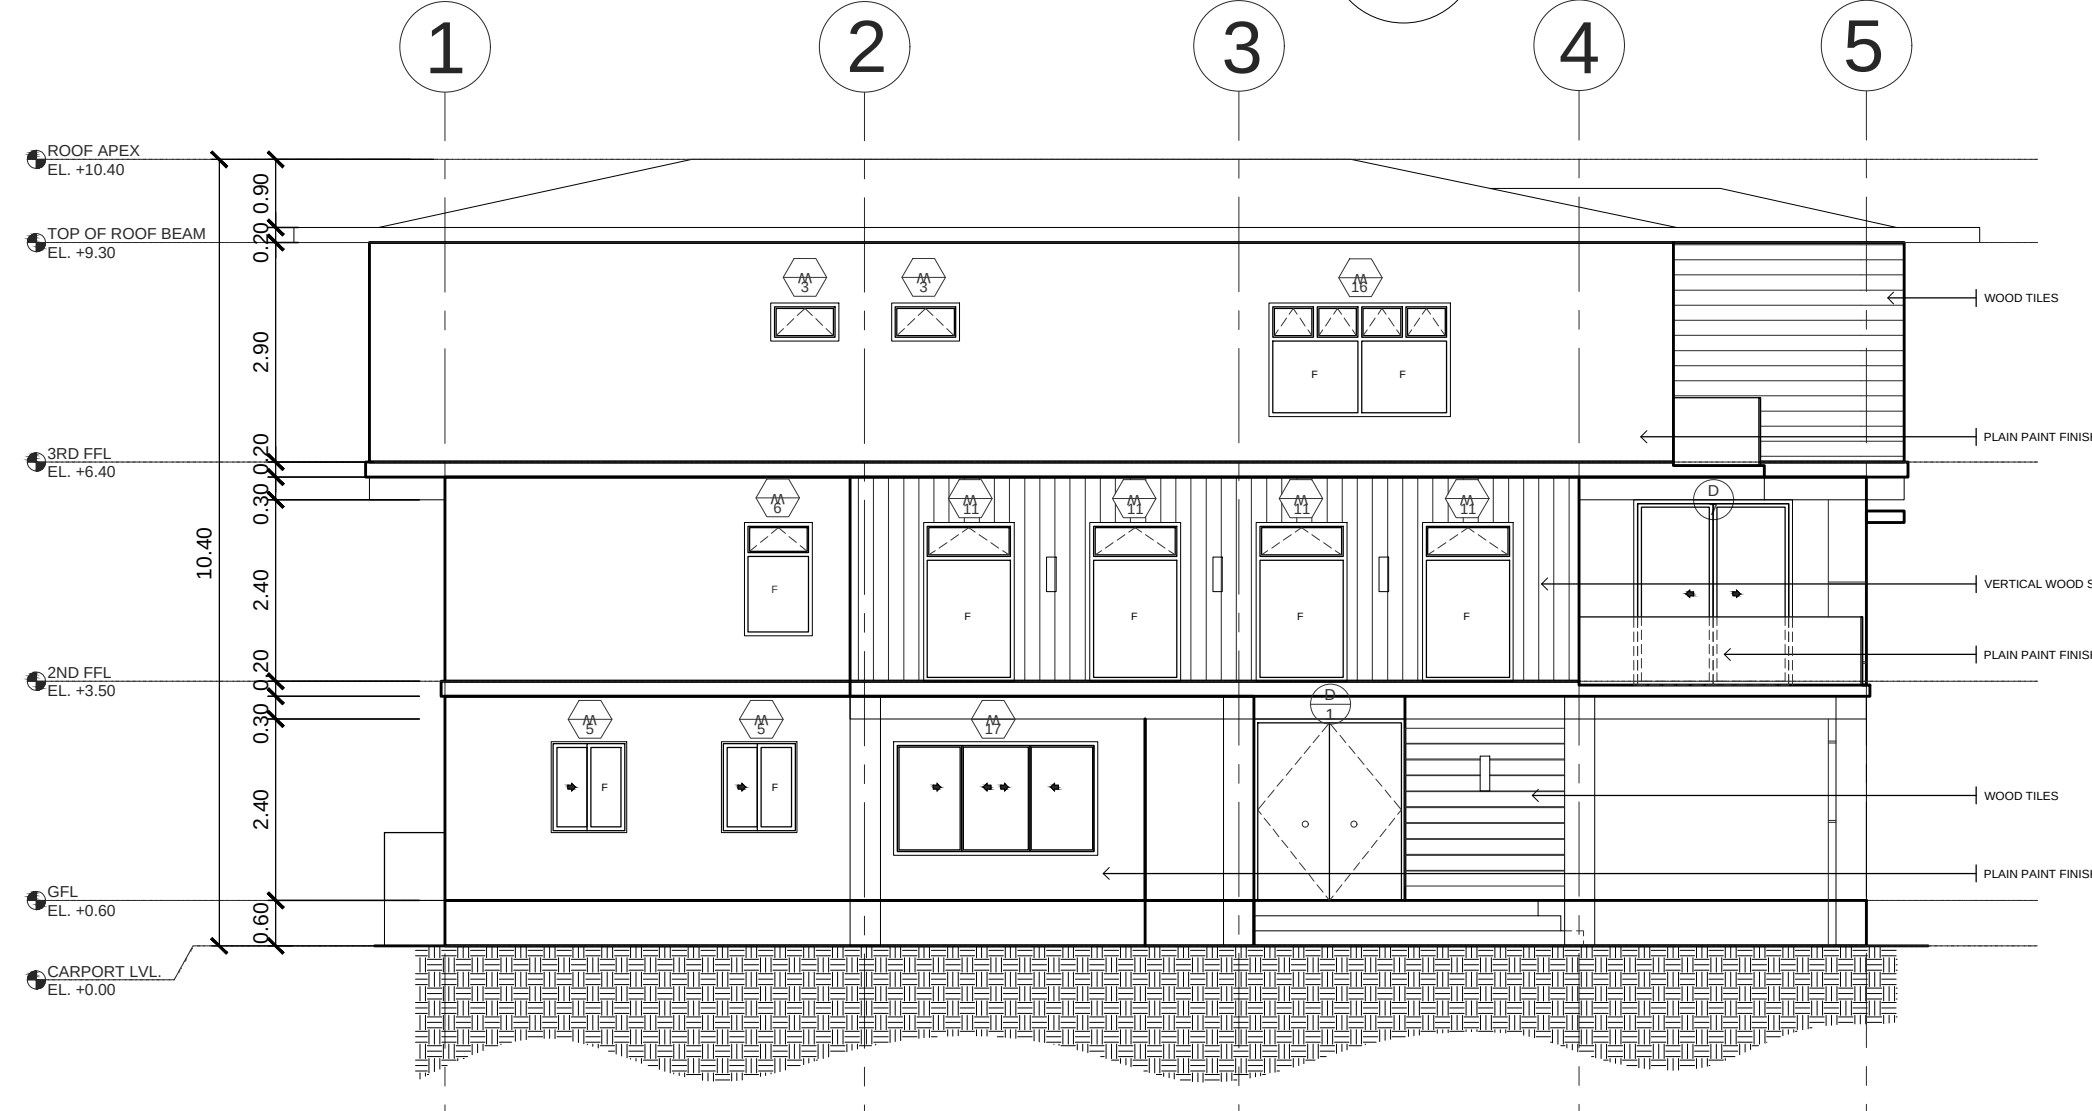

ARANETA RESIDENCE
4 RIGHT SIDE ELEVATION
A-06 SCALE: 1:100 MTS

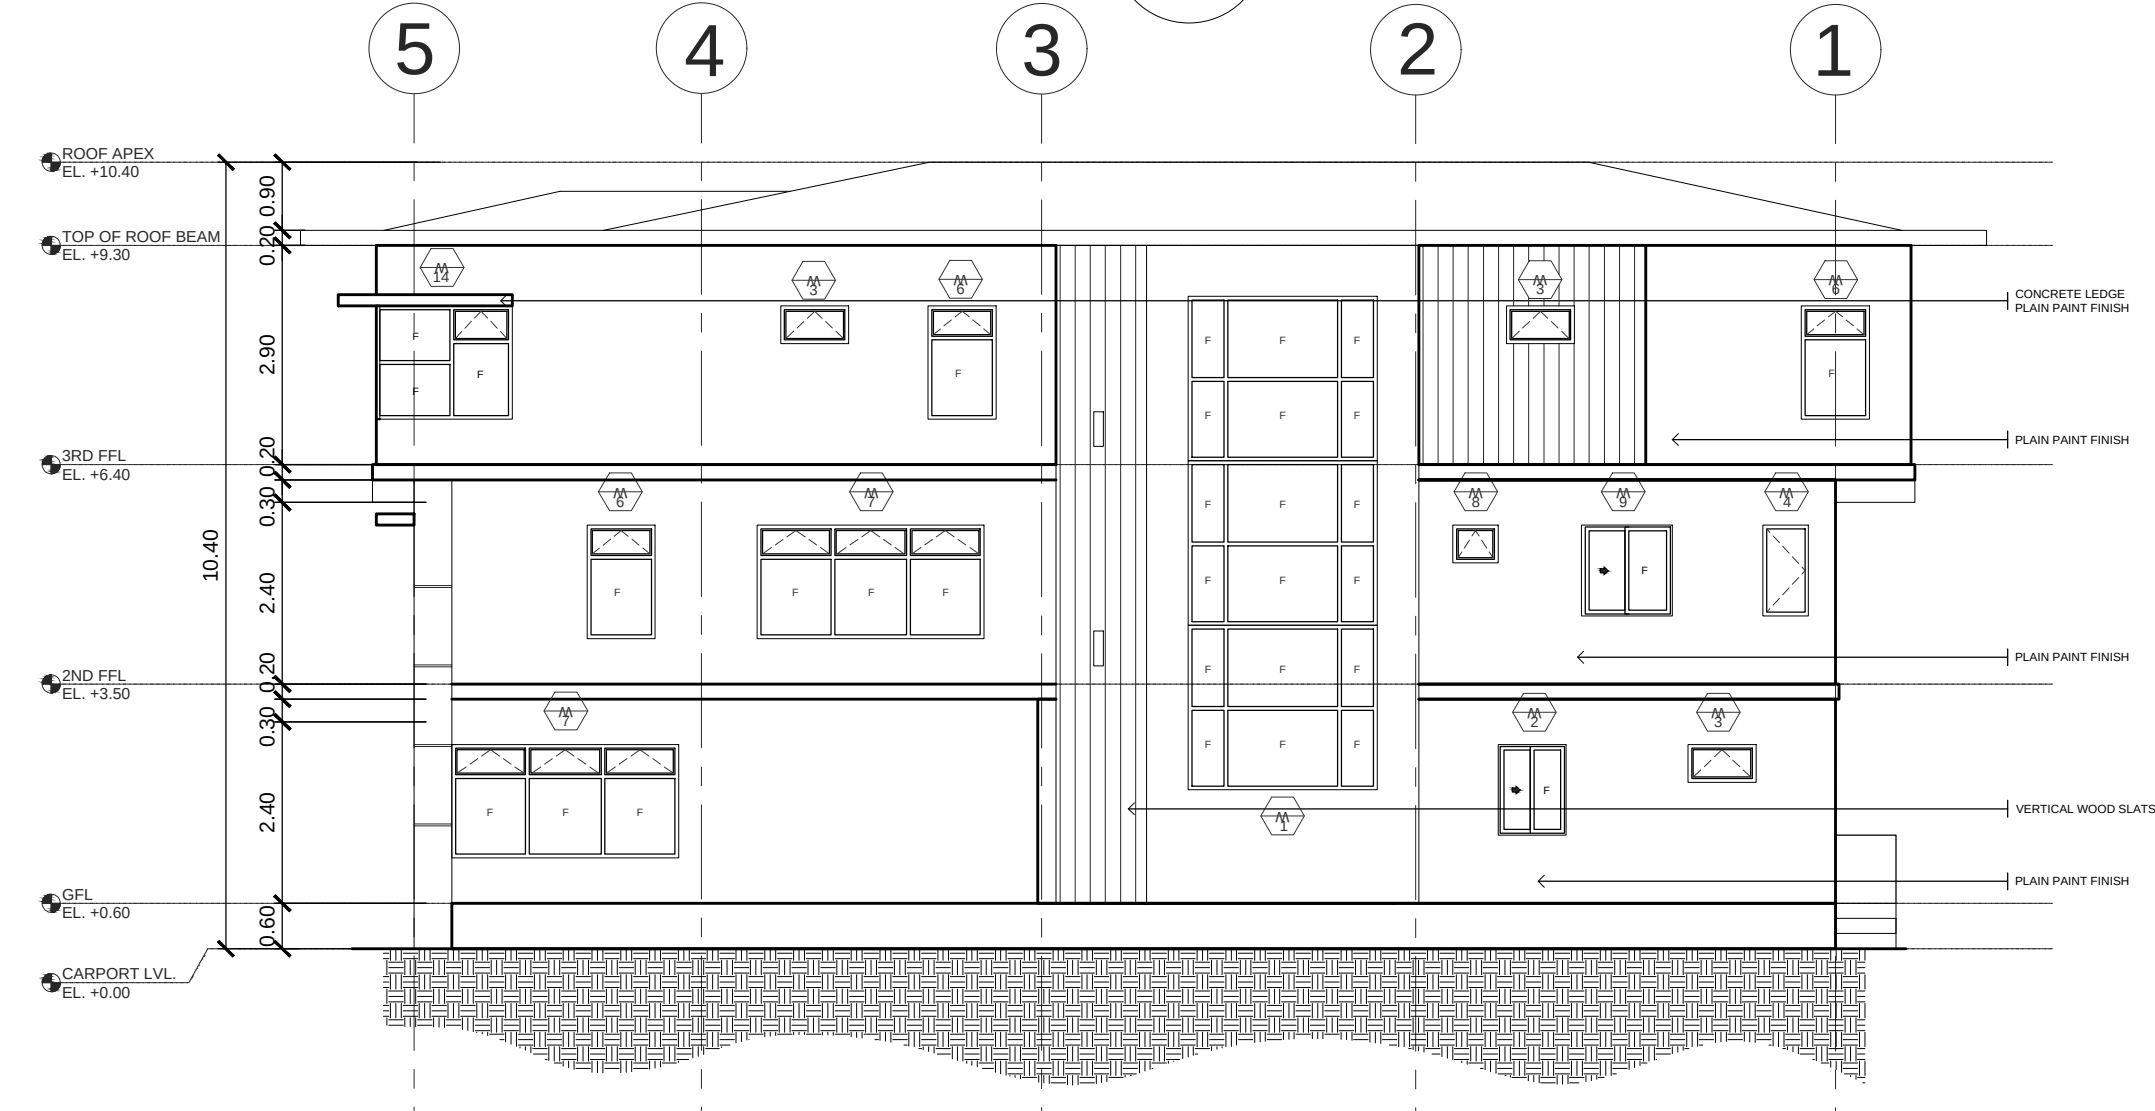

ARANETA RESIDENCE
5 LEFT SIDE ELEVATION
A-06 SCALE: 1:100 MTS

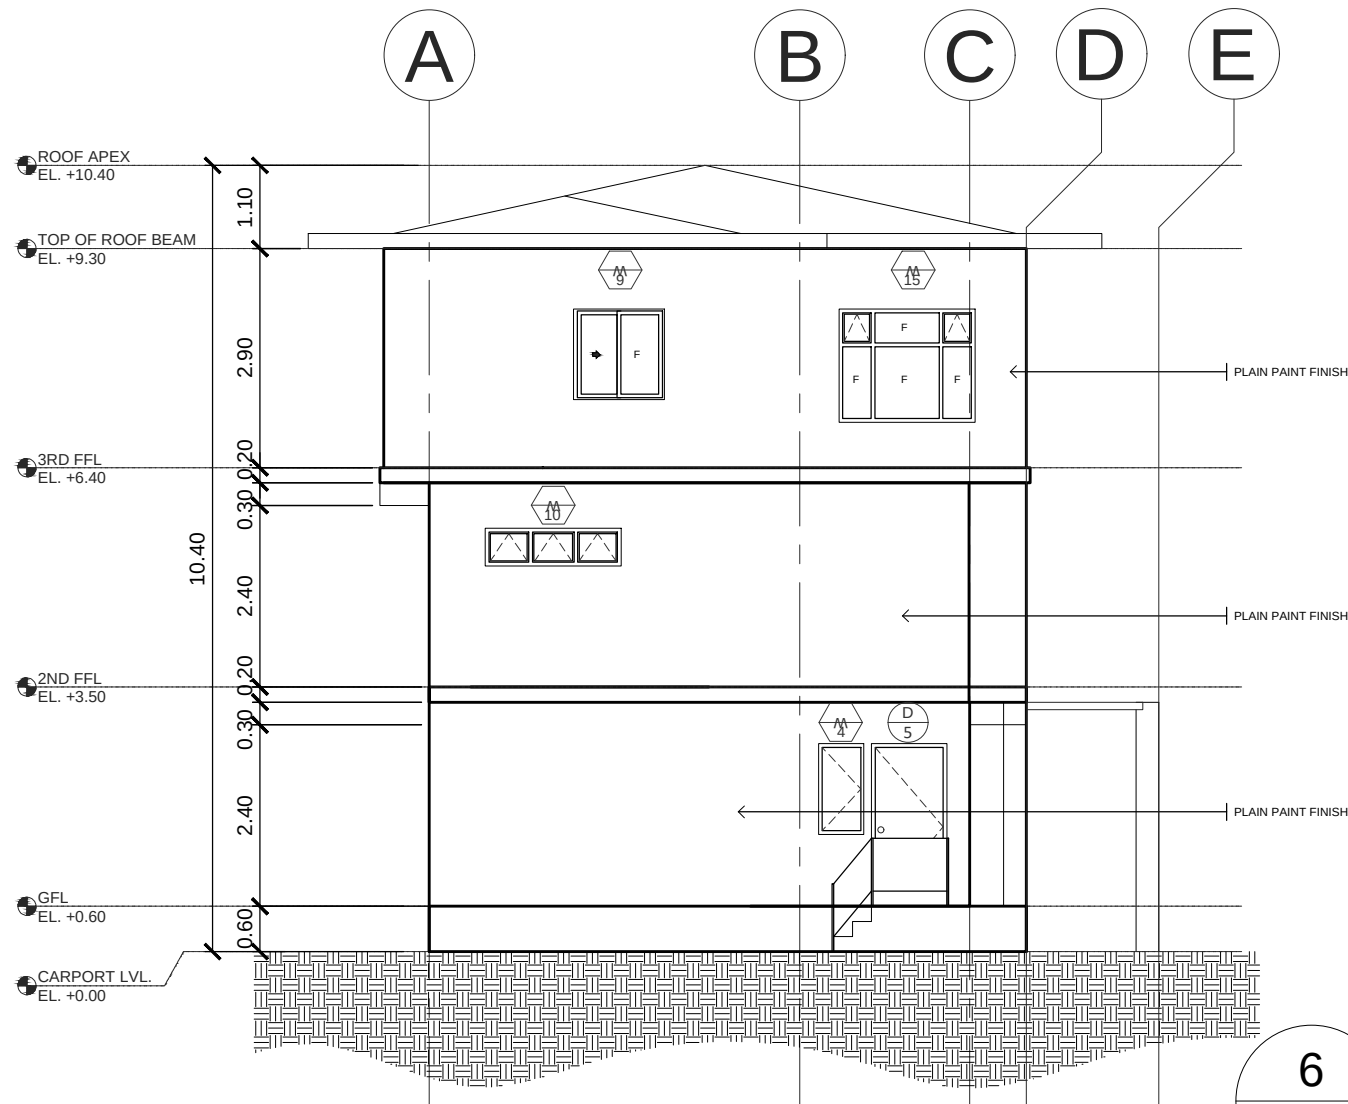

ARANETA RESIDENCE
6 REAR ELEVATION
A-06 SCALE: 1:100 MTS