
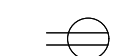
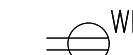
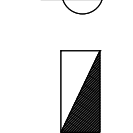


LEGEND:

-  CONVENIENCE OUTLET
-  WATER HEATER
-  REFRIGERATOR OUTLET
-  WEATHER PROOF OUTLET
-  AIRCON UNIT
-  COUNTERTOP OUTLET
-  RANGE OUTLET
-  PANELBOARD

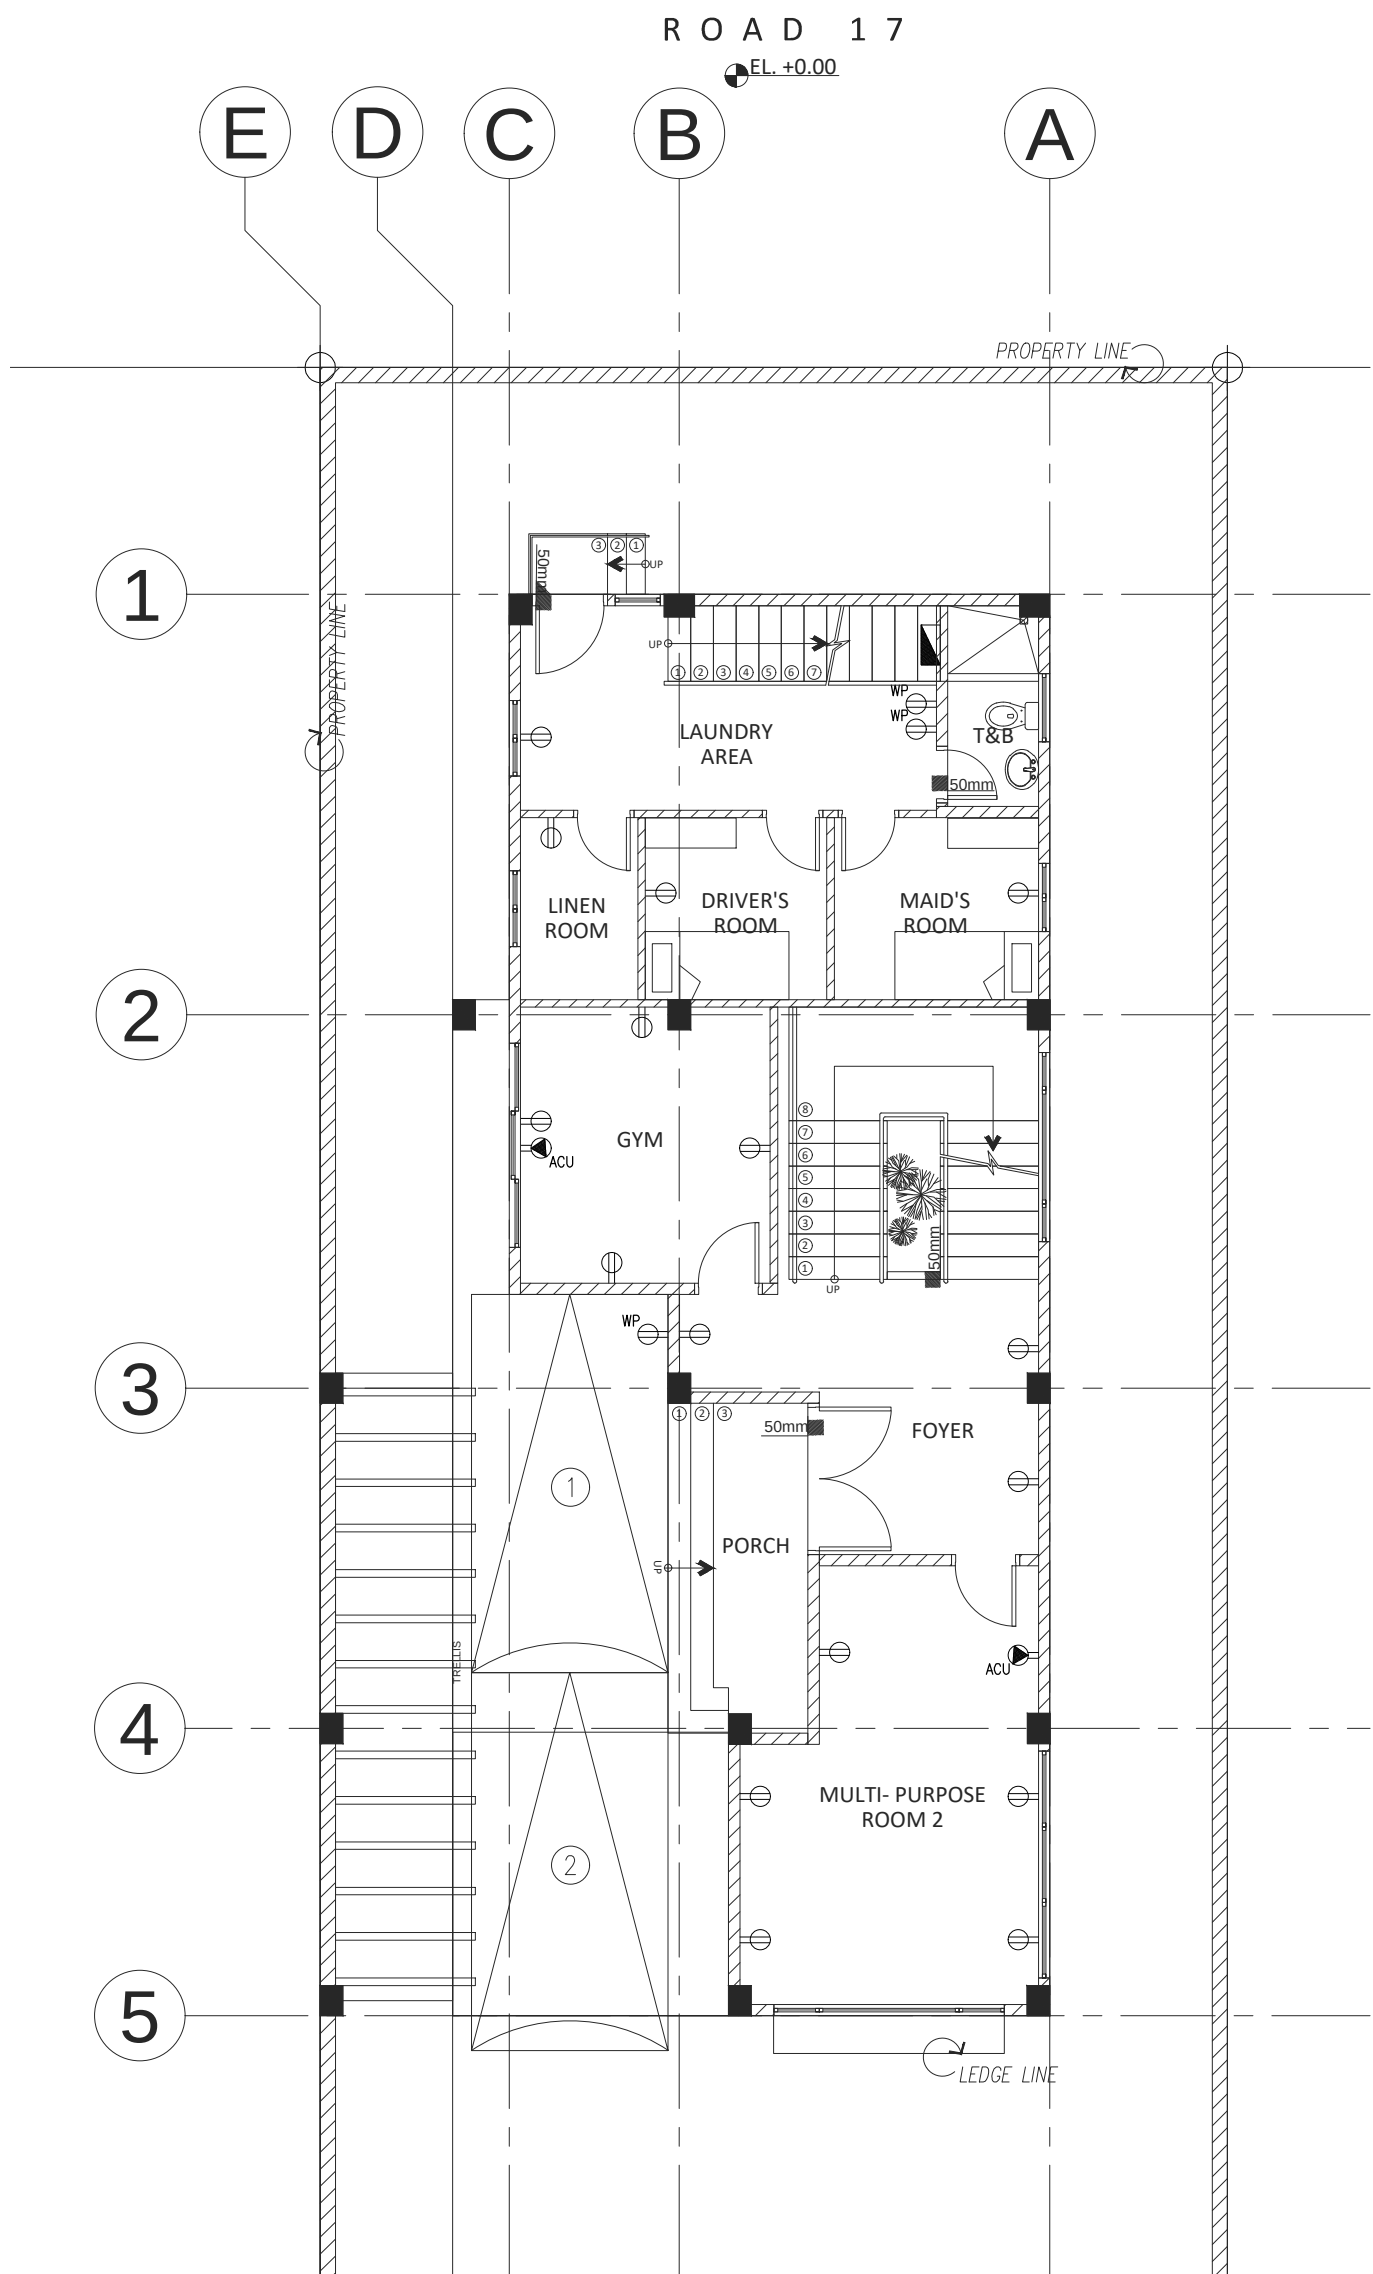


ARANETA RESIDENCE

1
A-00

GROUND POWER LAYOUT

SCALE: 1:100 MTS.

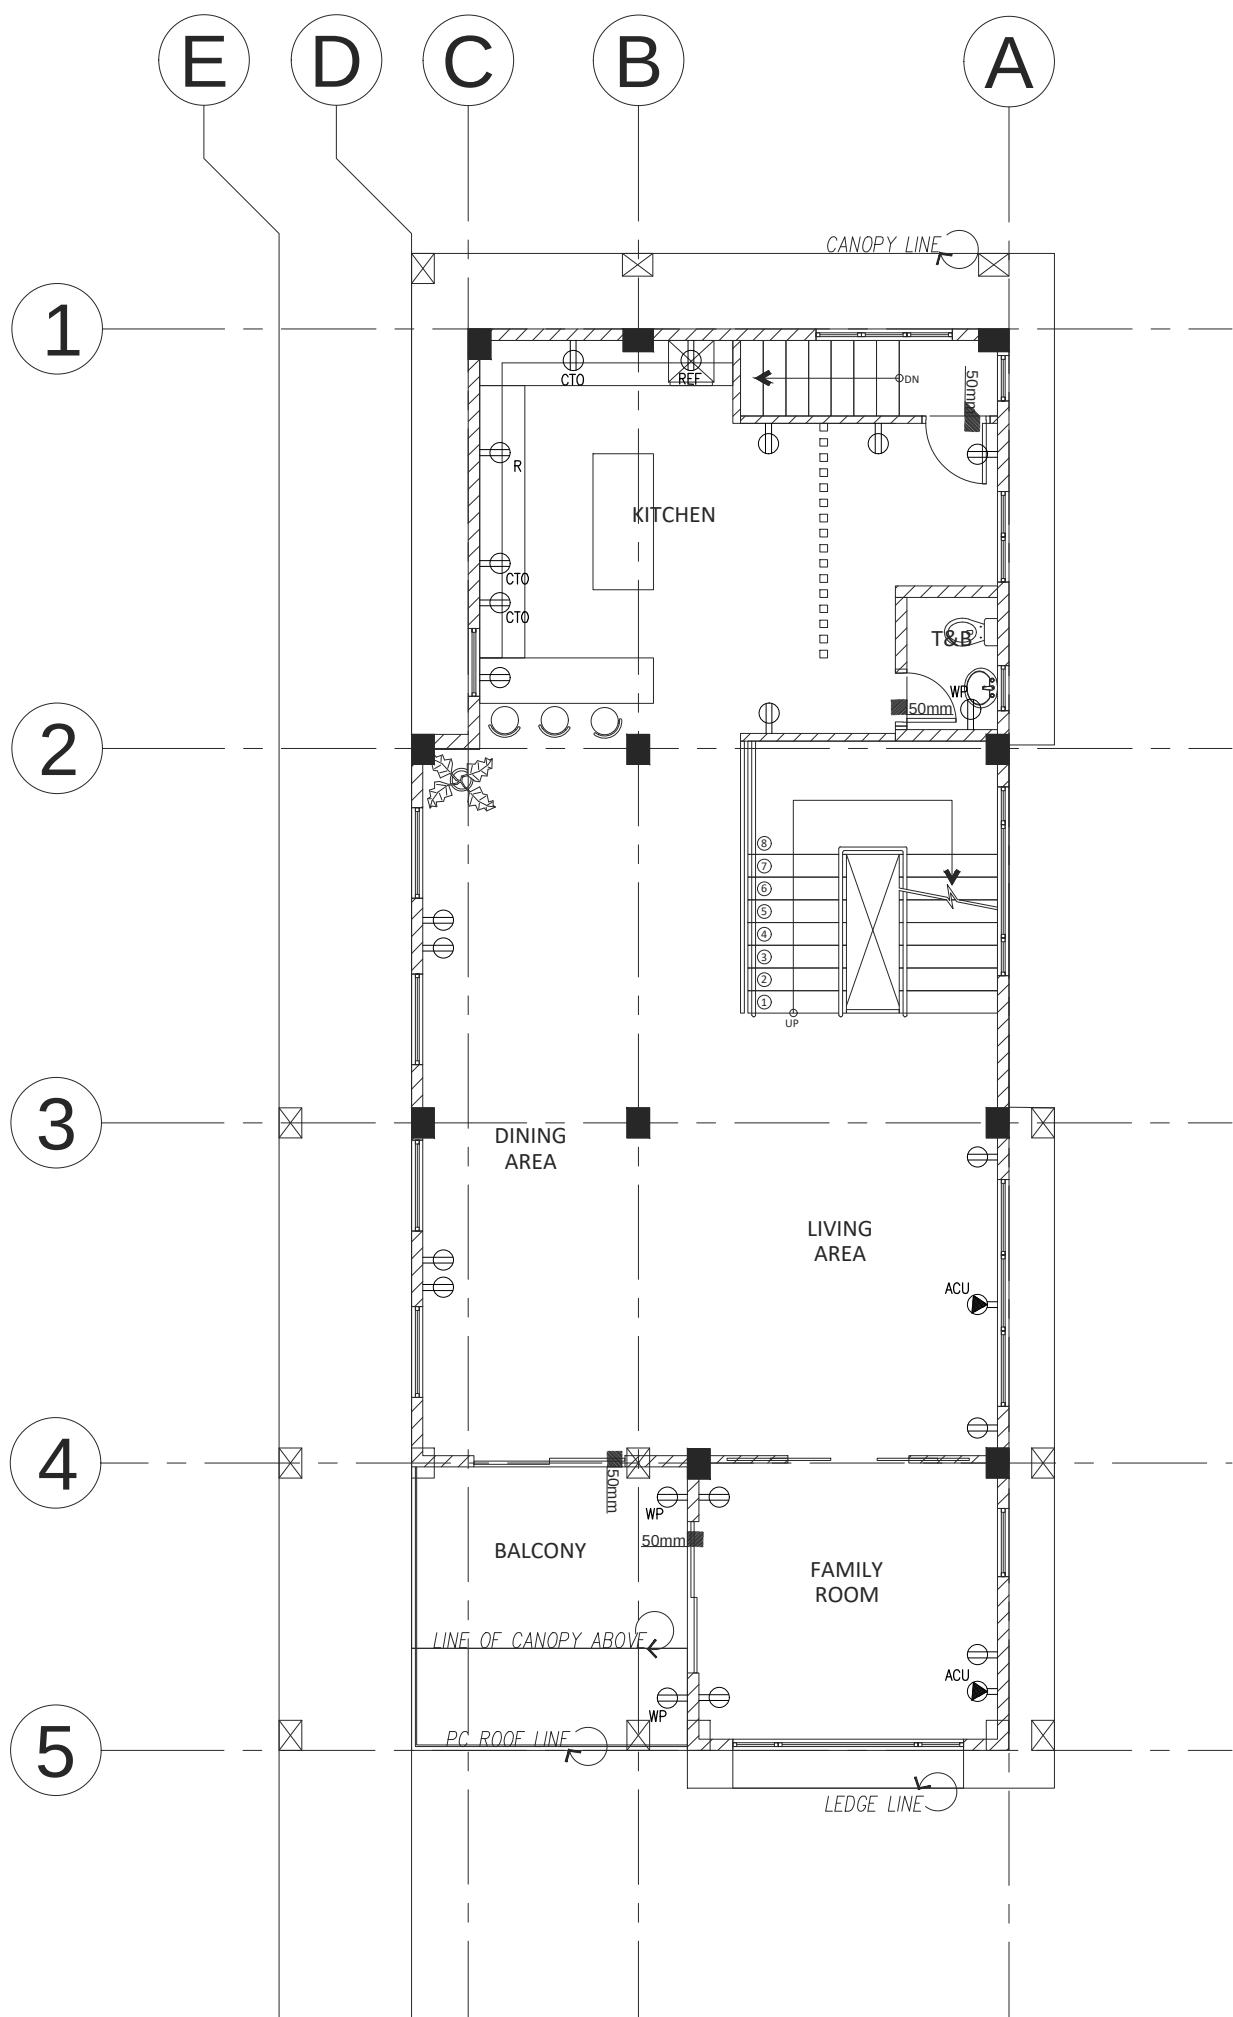


ARANETA RESIDENCE

2
A-00

SECOND POWER LAYOUT

SCALE: 1:100 MTS.

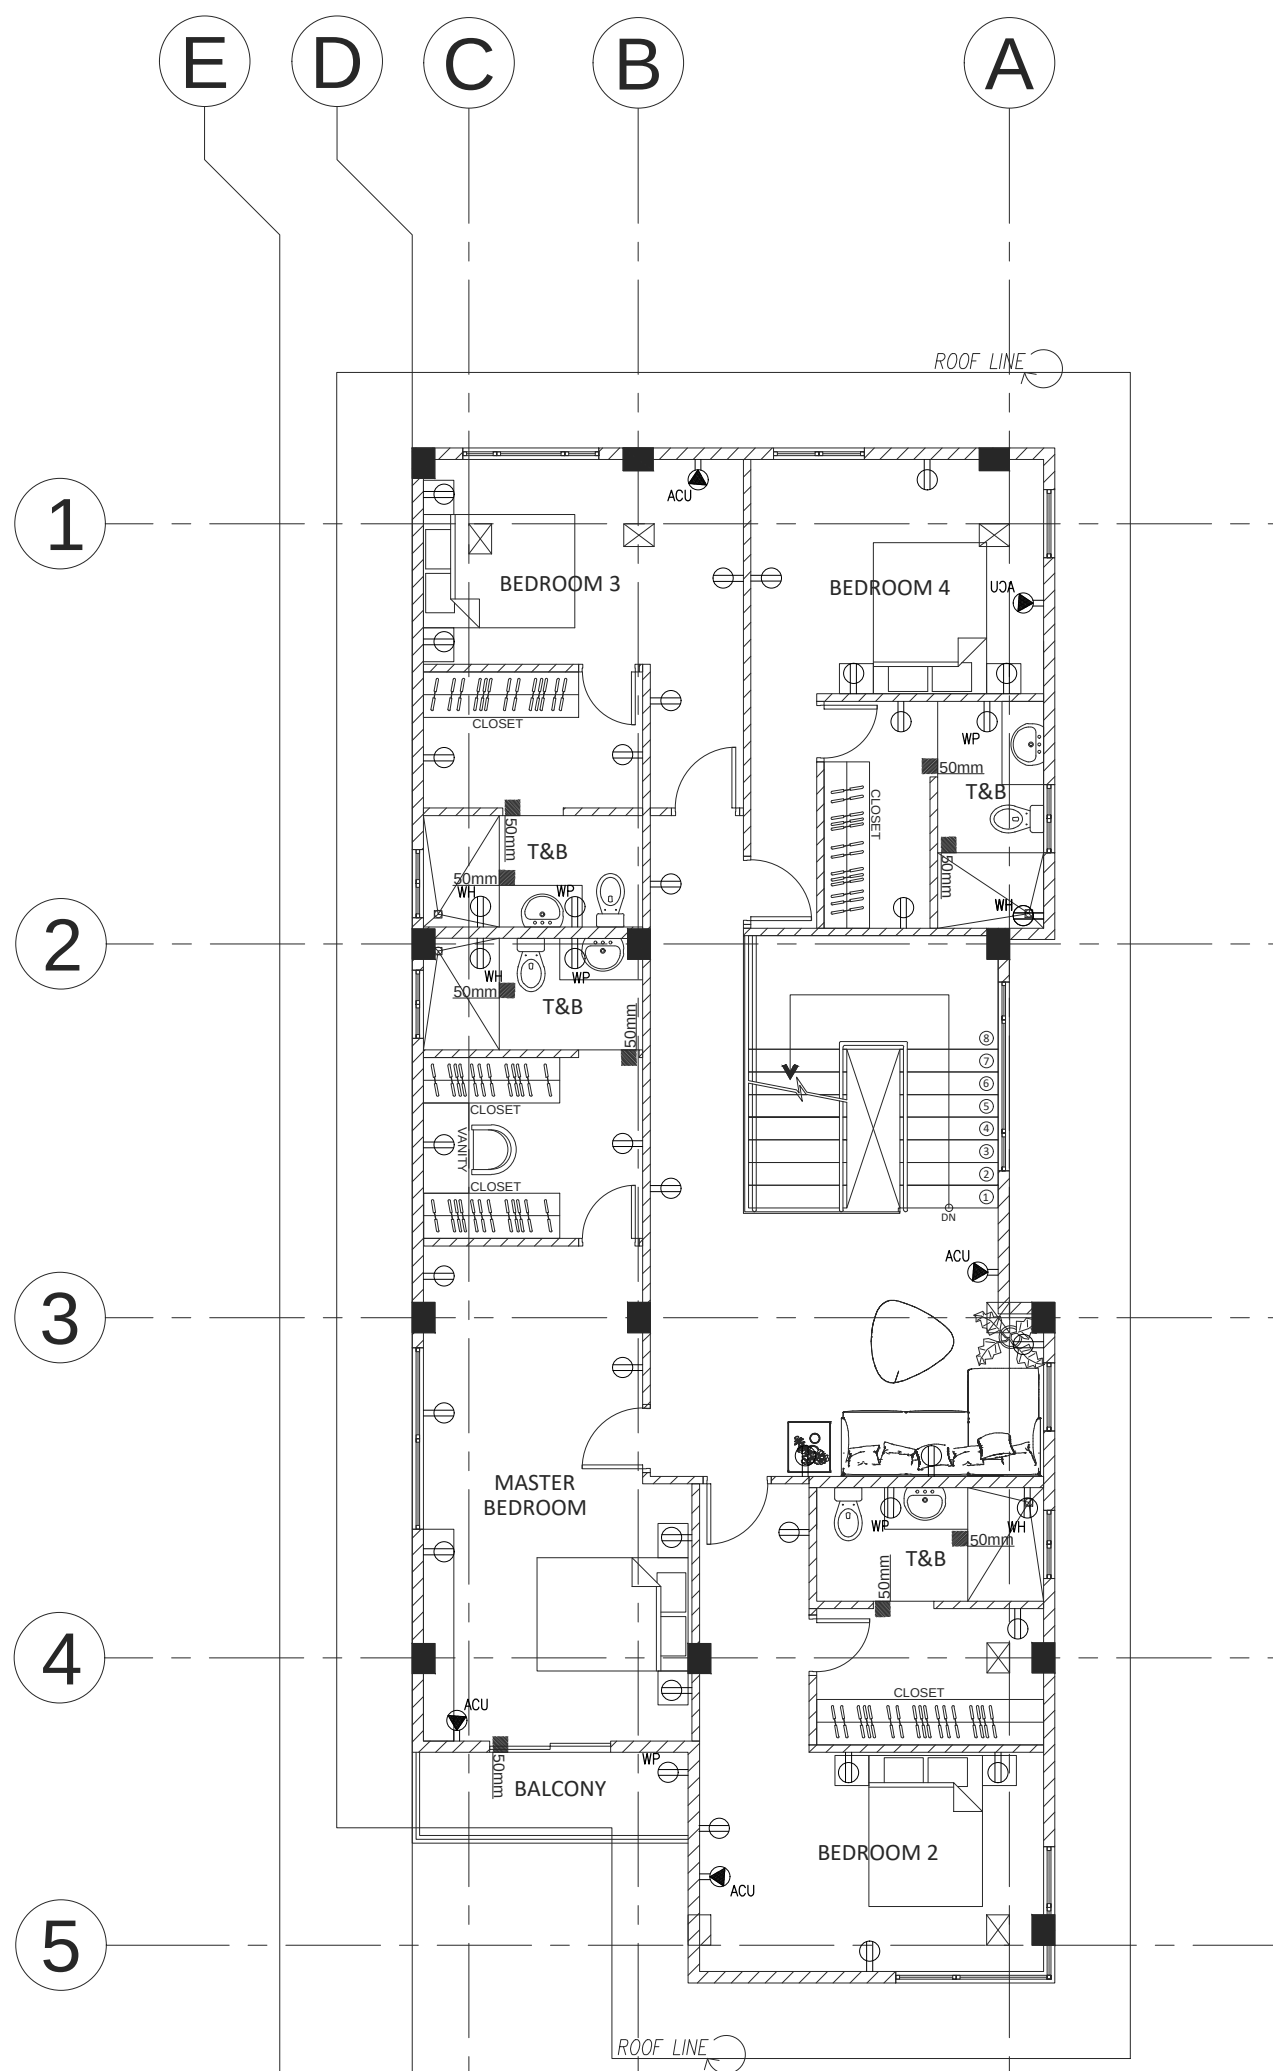

ARANETA RESIDENCE

3
A-00

THIRD POWER LAYOUT

SCALE: 1:100 MTS.

NO.	REVISIONS	DATE
-----	-----------	------

ALL WORKS SHALL BE CARRIED OUT IN ACCORDANCE WITH ALL BY LAWS AND CODES HAVING JURISDICTION OVER THIS SITE LOCATION. ALL DIMENSIONS AND INFORMATION SHALL BE CHECKED AND VERIFIED ON THE JOB AND ANY VARIANCES TO THE ARCHITECT.

THESE DRAWINGS MUST NOT BE SCALED. THE DESIGN AND CONTRACT DOCUMENTS ARE THE COPYRIGHT PROPERTY OF THE ARCHITECT AND MAY NOT BE REPRODUCED, ALTERED OR REUSED WITHOUT THE ARCHITECT'S WRITTEN AUTHORITY.

SANITARY

PRC. NO.	T.J.N.	DATE:
----------	--------	-------

MECHANICAL

PRC. NO.	T.J.N.	DATE:
----------	--------	-------

ELECTRICAL

PRC. NO.	T.J.N.	DATE:
----------	--------	-------

STRUCTURAL

PRC. NO.	T.J.N.	DATE:
----------	--------	-------

ARCHITECT

REANNE DENISE G. PE

PRC. NO.	T.J.N.	DATE:
----------	--------	-------

OWNER

MS. CINDY DE LUCIA

PROJECT:

PROPOSED
ARANETA RESIDENCE
LOT 16 AND 17, ARANETA VILLAGE,
POTRIERO, MALABON CITY, METRO MANILA.

SHEET CONTENT:

POWER LAYOUT

DESIGN:	SCALE:	SHEET NO.
RDP	1:100	A-00
DRAWN:	DATE:	
RDP	01/02/22	