




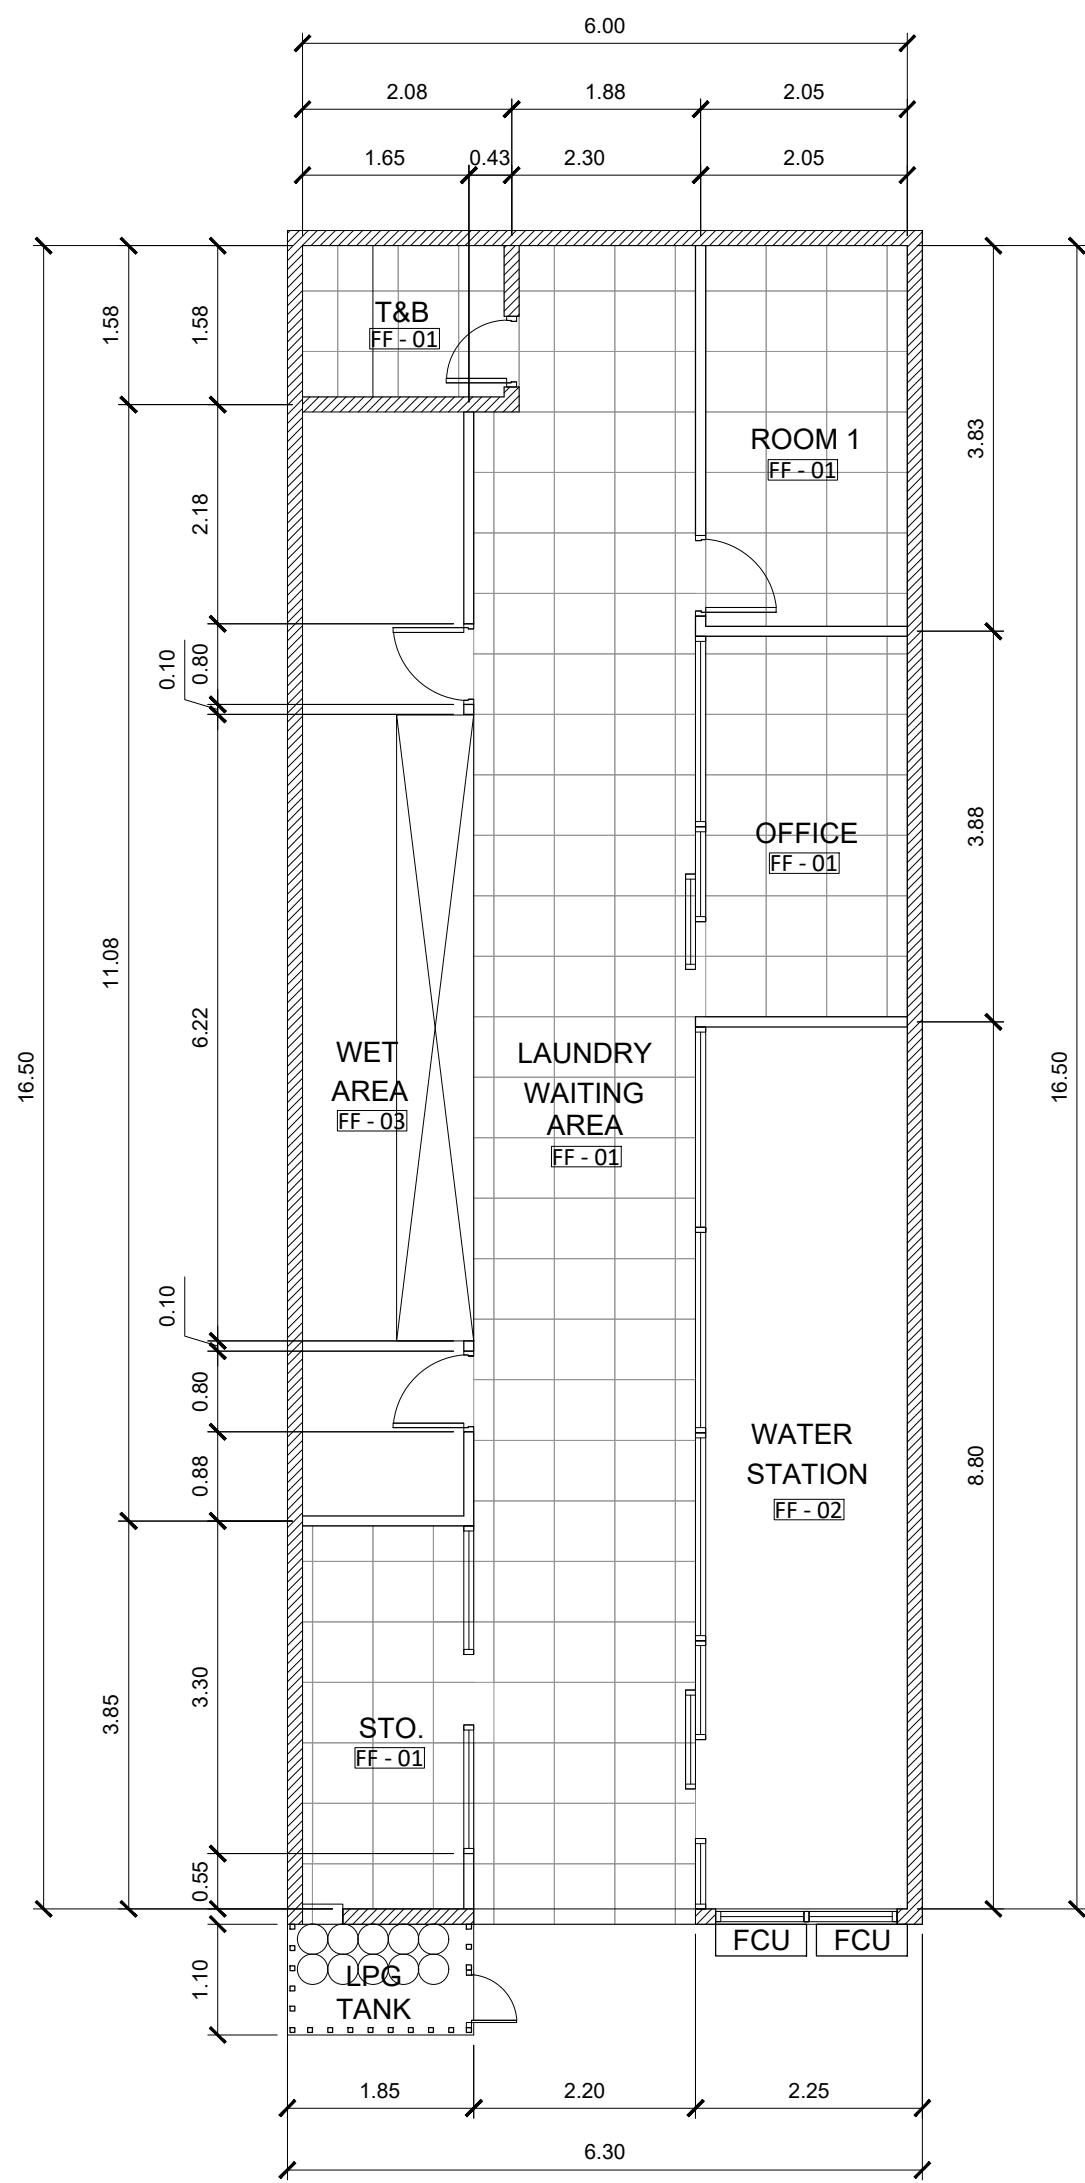


1 FLOOR FINISH LAYOUT
A-02 SCALE: 1:75 MTS.

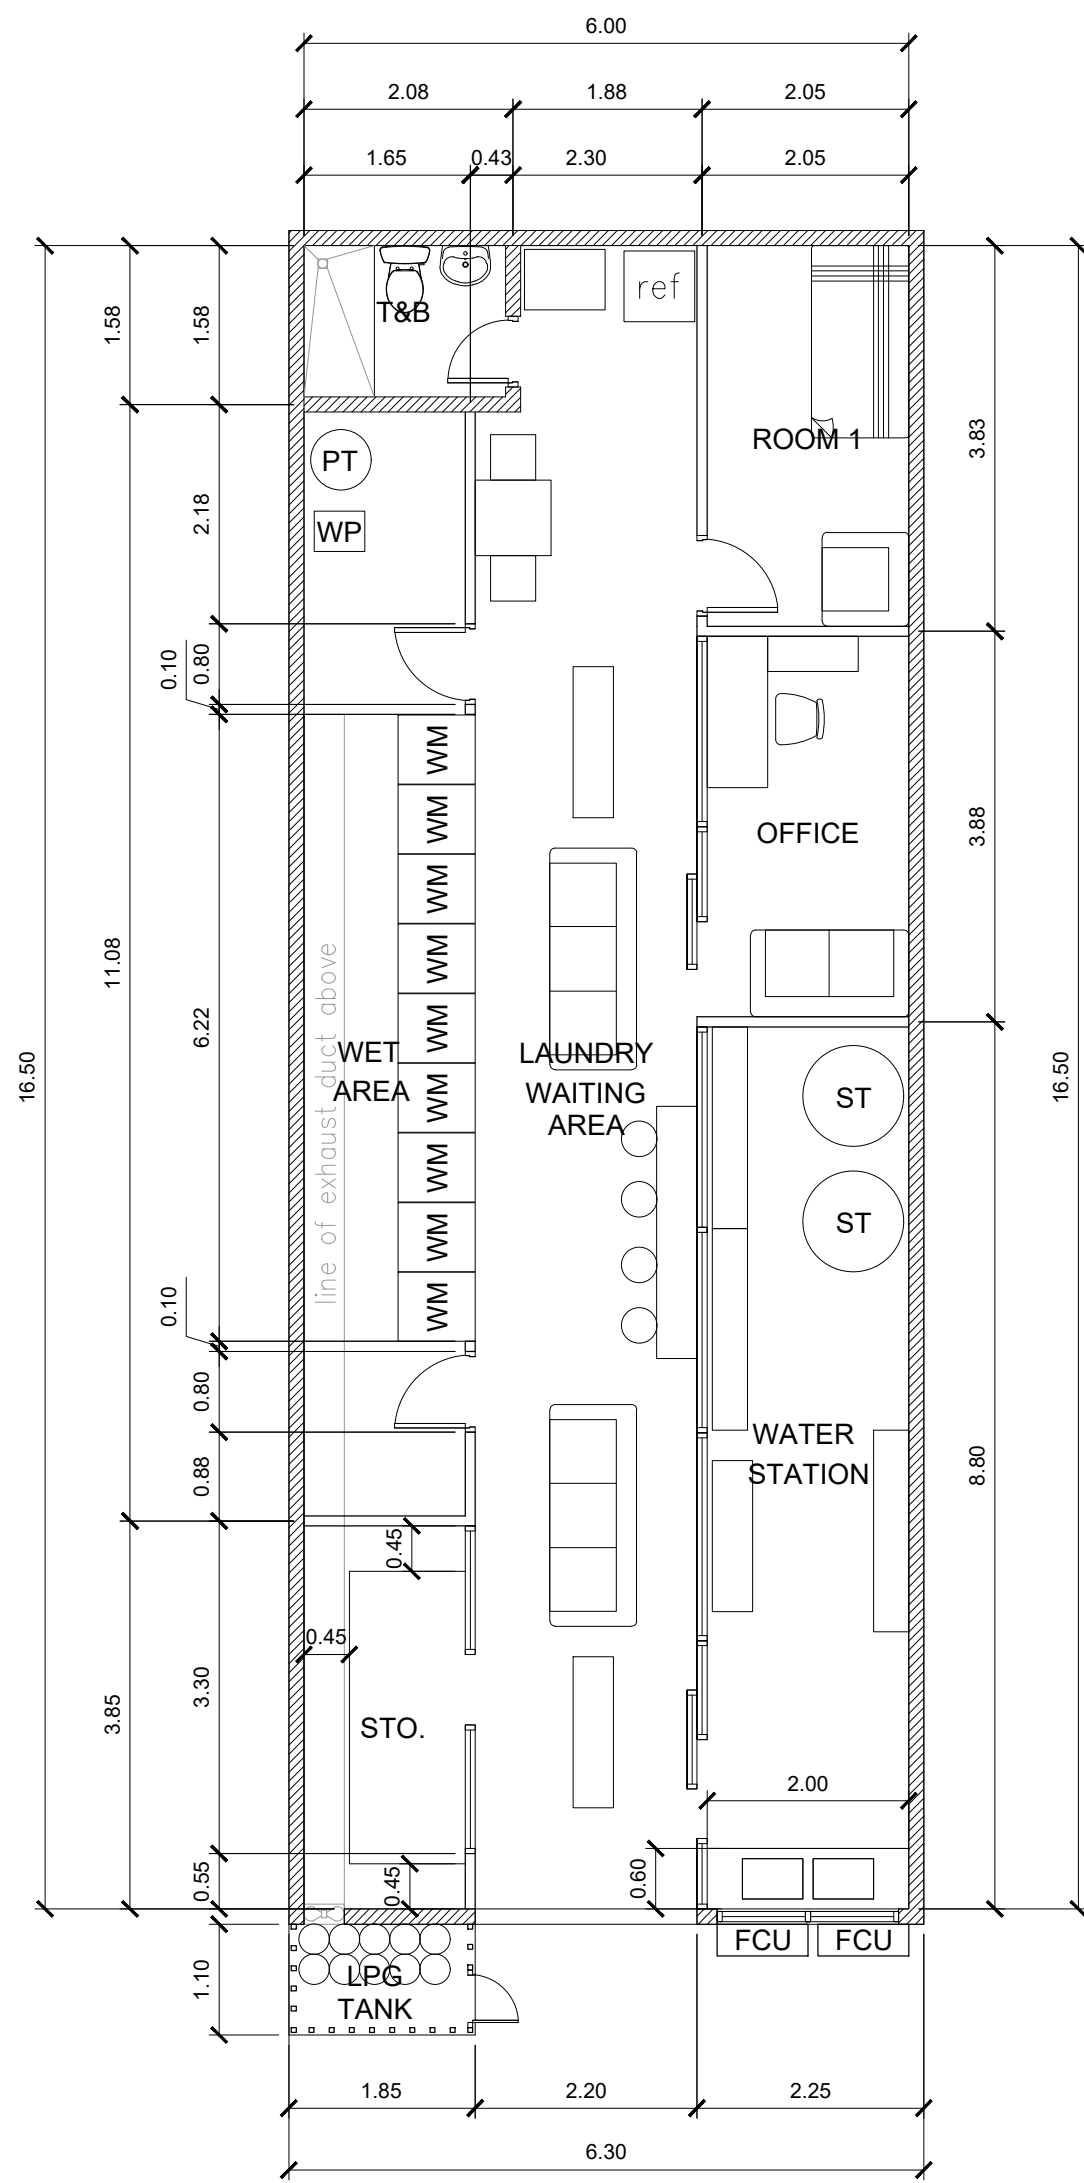

2 FURNITURE LAYOUT
A-02 SCALE: 1:75 MTS.

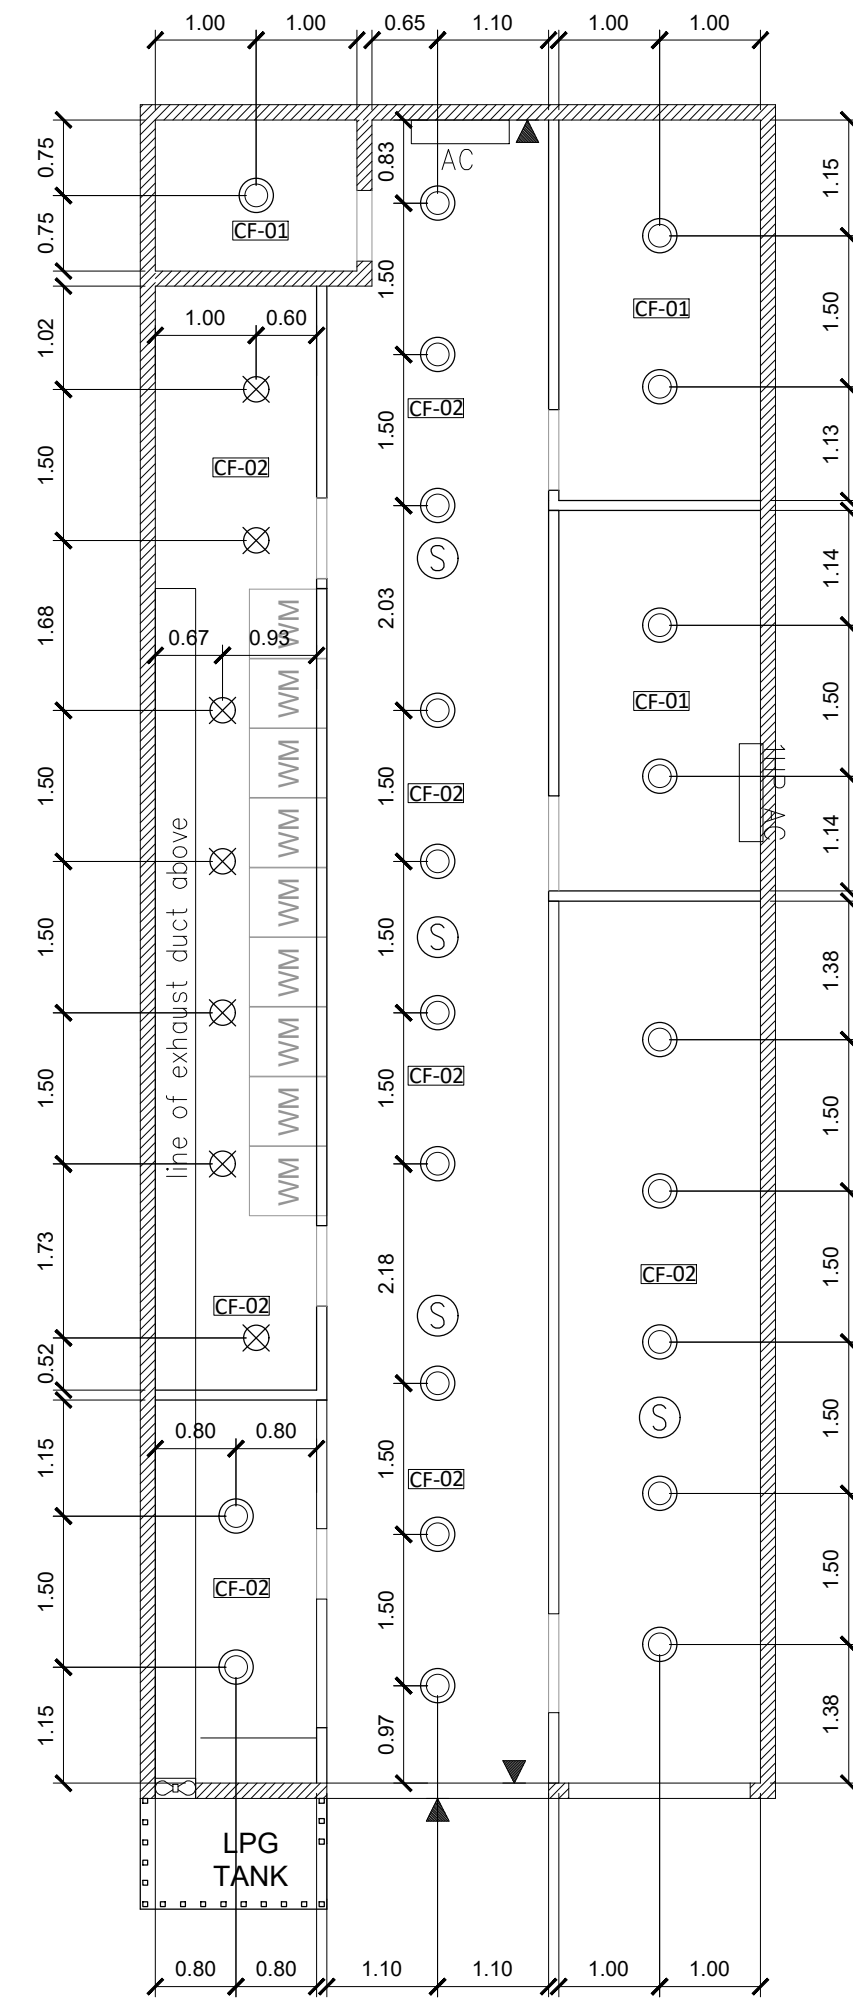

3 REFLECTED CEILING PLAN
A-02 SCALE: 1:75 MTS.

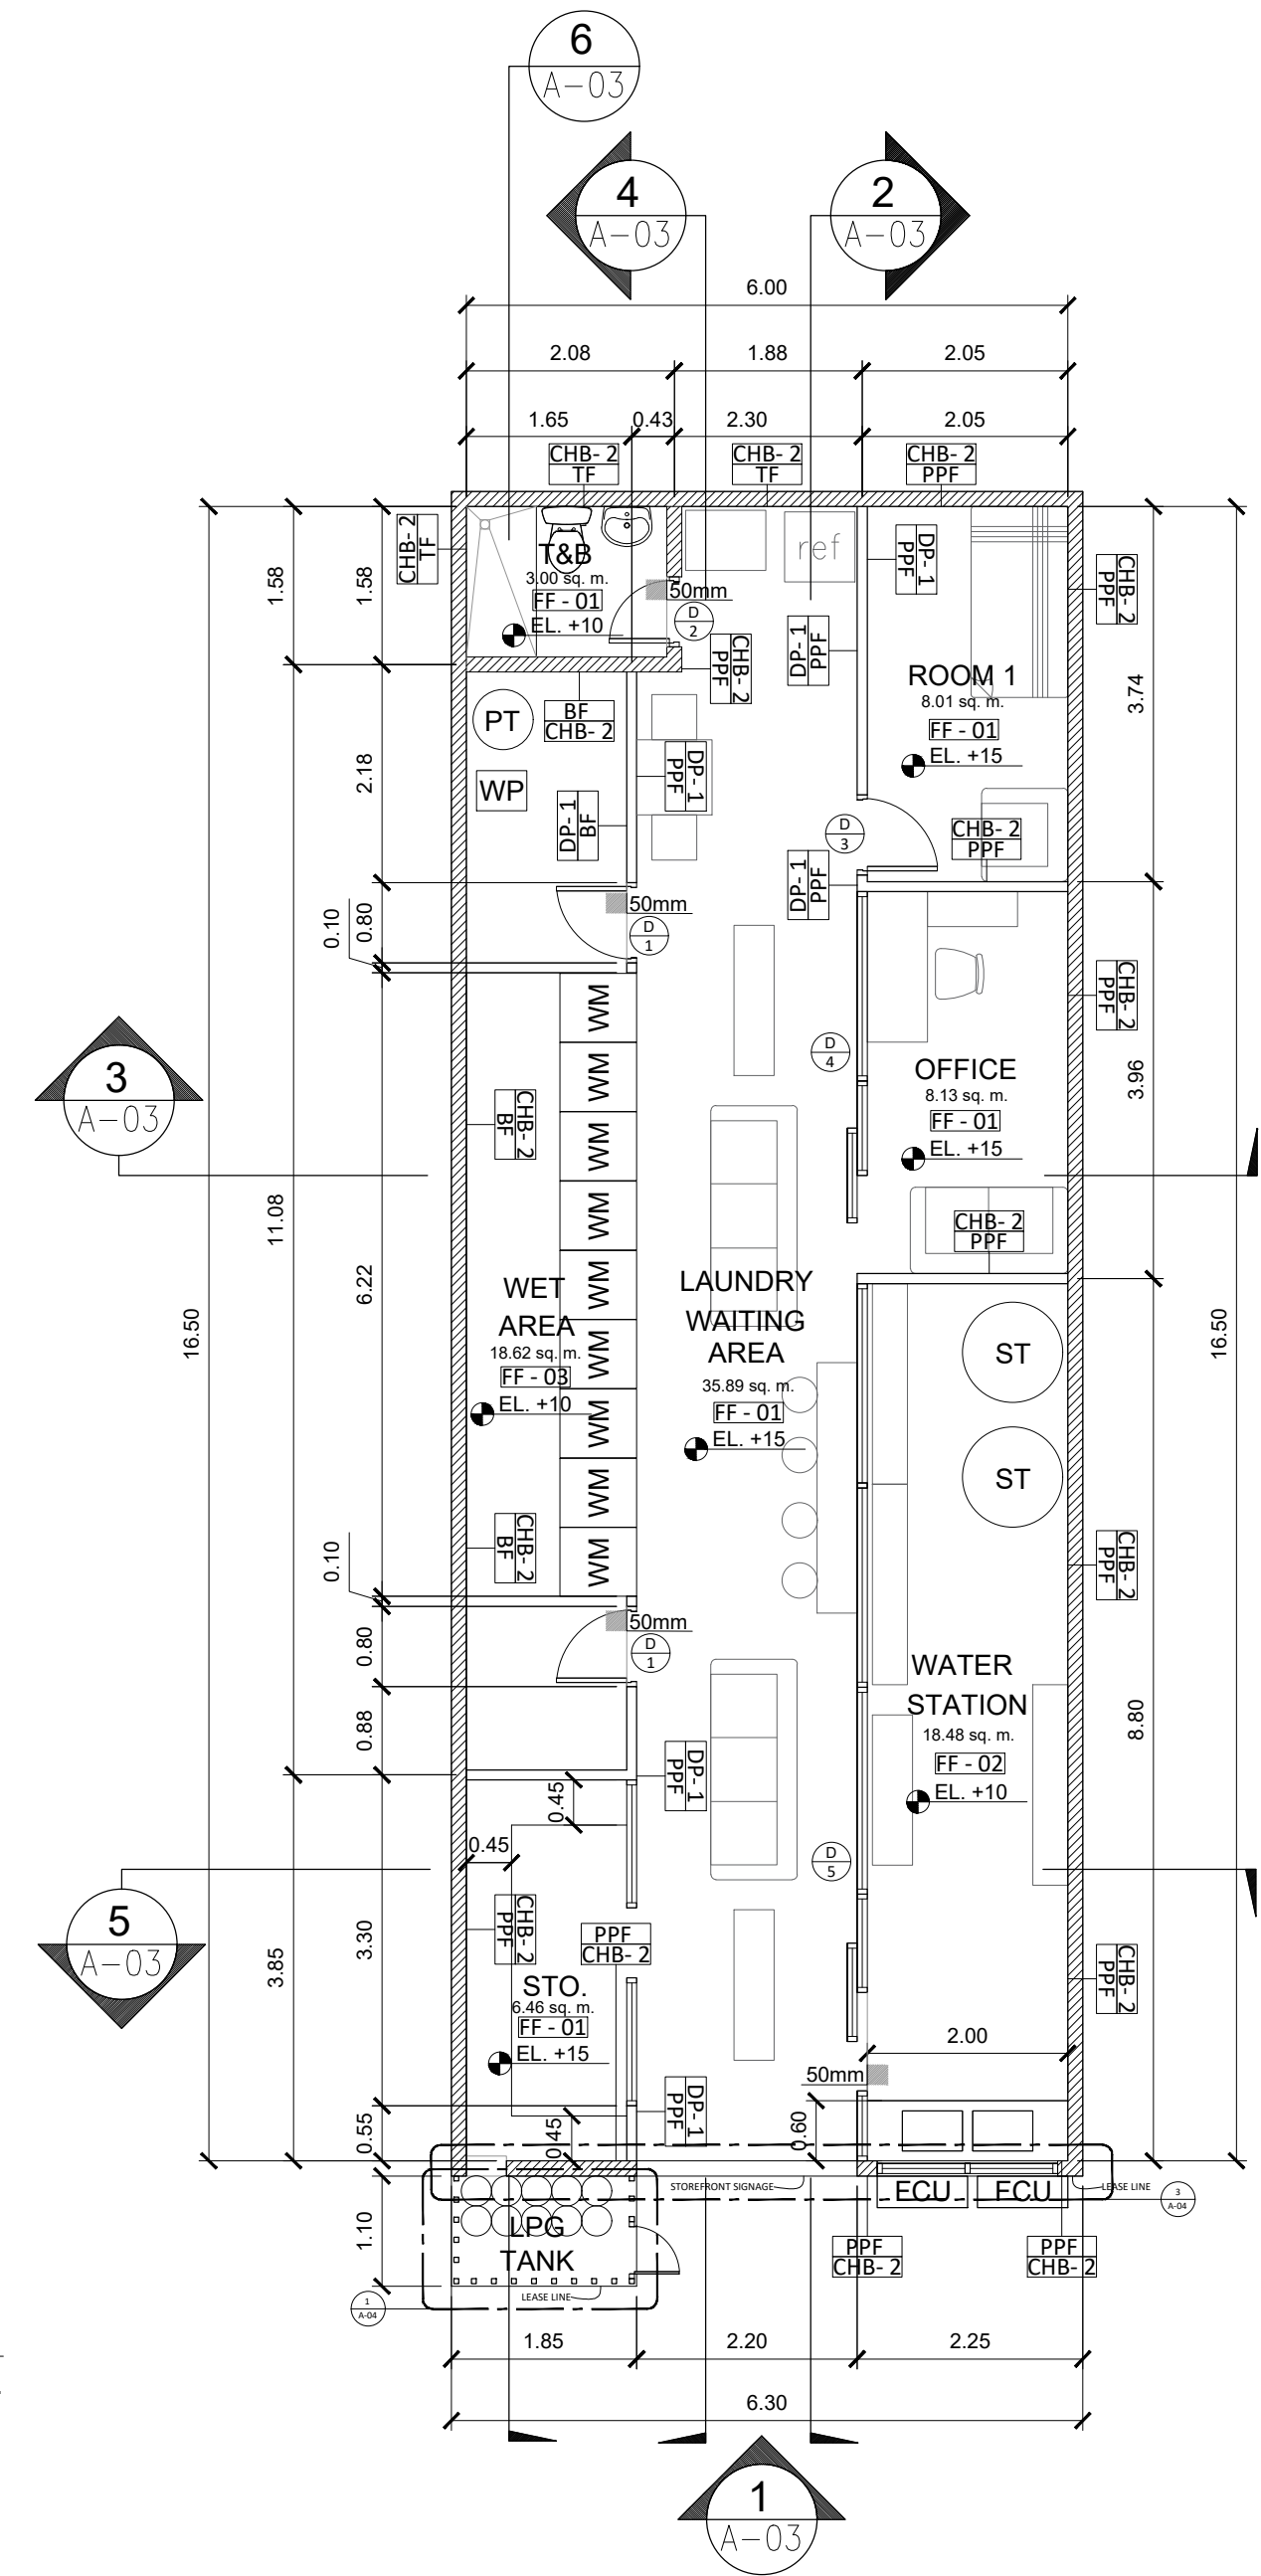

4 GROUND FLOOR PLAN
A-02 SCALE: 1:75 MTS.

LEGEND:

FF - 01	60 CM X 60 CM NON SKID CERAMIC TILE COLOR TO BE VERIFIED
FF - 02	RUBBERIZED PAINT FINISH (WITH WATERPROOFING) COLOR TO BE VERIFIED
FF - 03	BARE CONCRETE FINISH (WITH WATERPROOFING)
CHB- 1	CONCRETE HOLLOW BLOCK 4"
CHB- 2	CONCRETE HOLLOW BLOCK 6"
DP- 1	DRYWALL 4"
TF	TILED FINISH
BF	BARE FINISH
WPF	WALLPAPER FINISH
PPF	PLAIN PAINT FINISH

CEILING FINISHES:

CF-01	GYPSUM BOARD, PAINTED FINISH.
CF-02	EXPOSED SLAB AND BEAM, PAINTED FINISH.

LIGHTING FIXTURES:

⊙	RECESSED: 200 mm. Ø DOWN LIGHT,
⊗	SURFACED: 200 mm. Ø DOWN LIGHT

⊙	SPRINKLER
---	-----------